




REVISION HISTORY		
REV	DESCRIPTION	DATE
	FIRST ISSUE	03/23/2026

FOR APPROVAL






PROJECT:	STW2732	
TITLE:	JXX - ARCH WALL PANEL	
DETAILS:	RENDERING	
DATE:	03/23/2026	
SHEET:	1 OF 3	
DRAWN:	JPO	
CHECK:	ACA	
SCALE:	AS SHOWN @ A1	
DRAWING N°:	REVISION:	
STW2732– JXX– 01	00	

REVISION HISTORY		
REV	DESCRIPTION	DATE
	FIRST ISSUE	03/23/2026




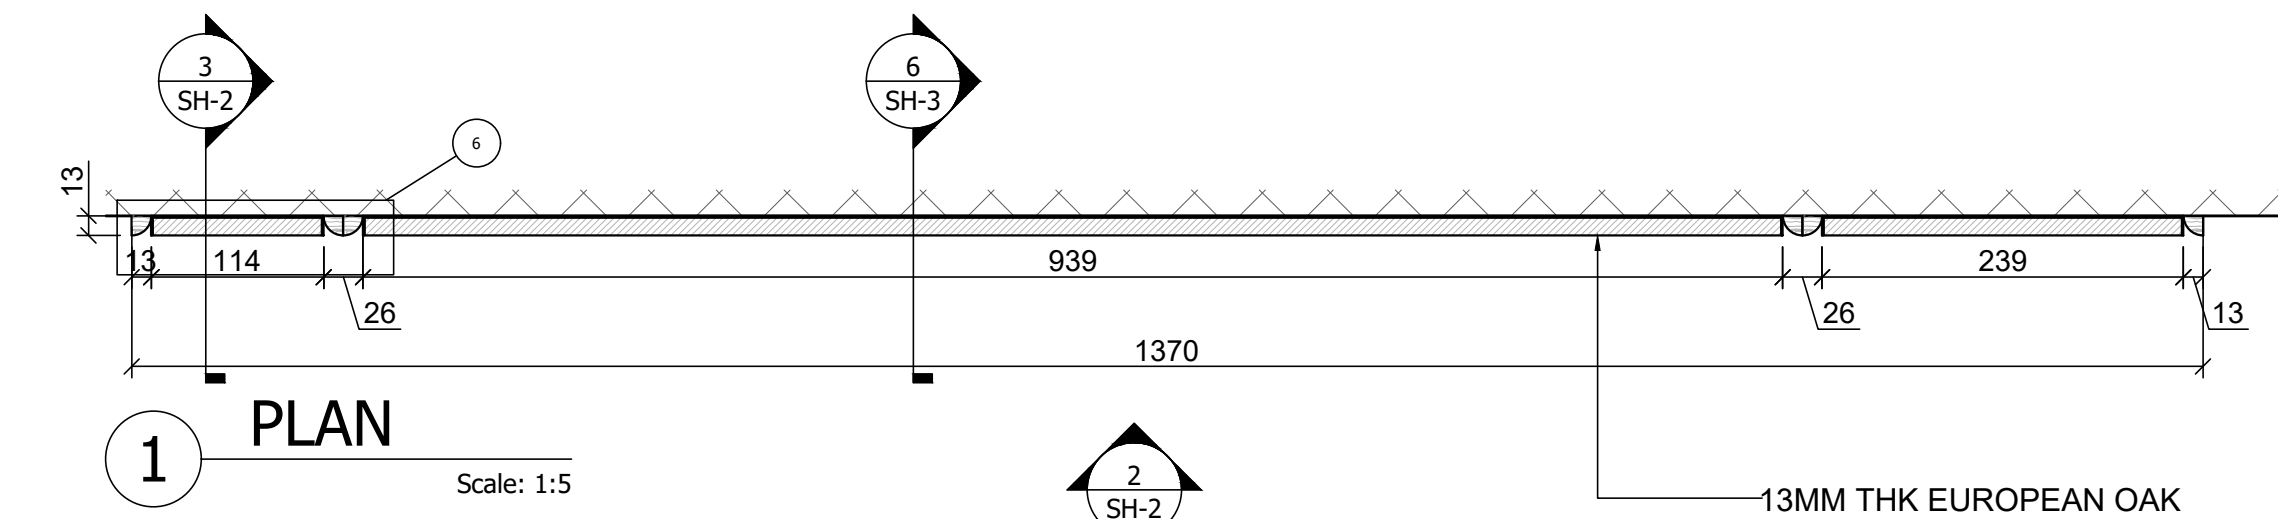


13MM THK EUROPEAN OAK
PRE-VENEERED MDF
PANEL, 1 MM SOLID OAK
EDGING, STAINED AND
LACQUERED TO MATCH
CONTROL SAMPLE

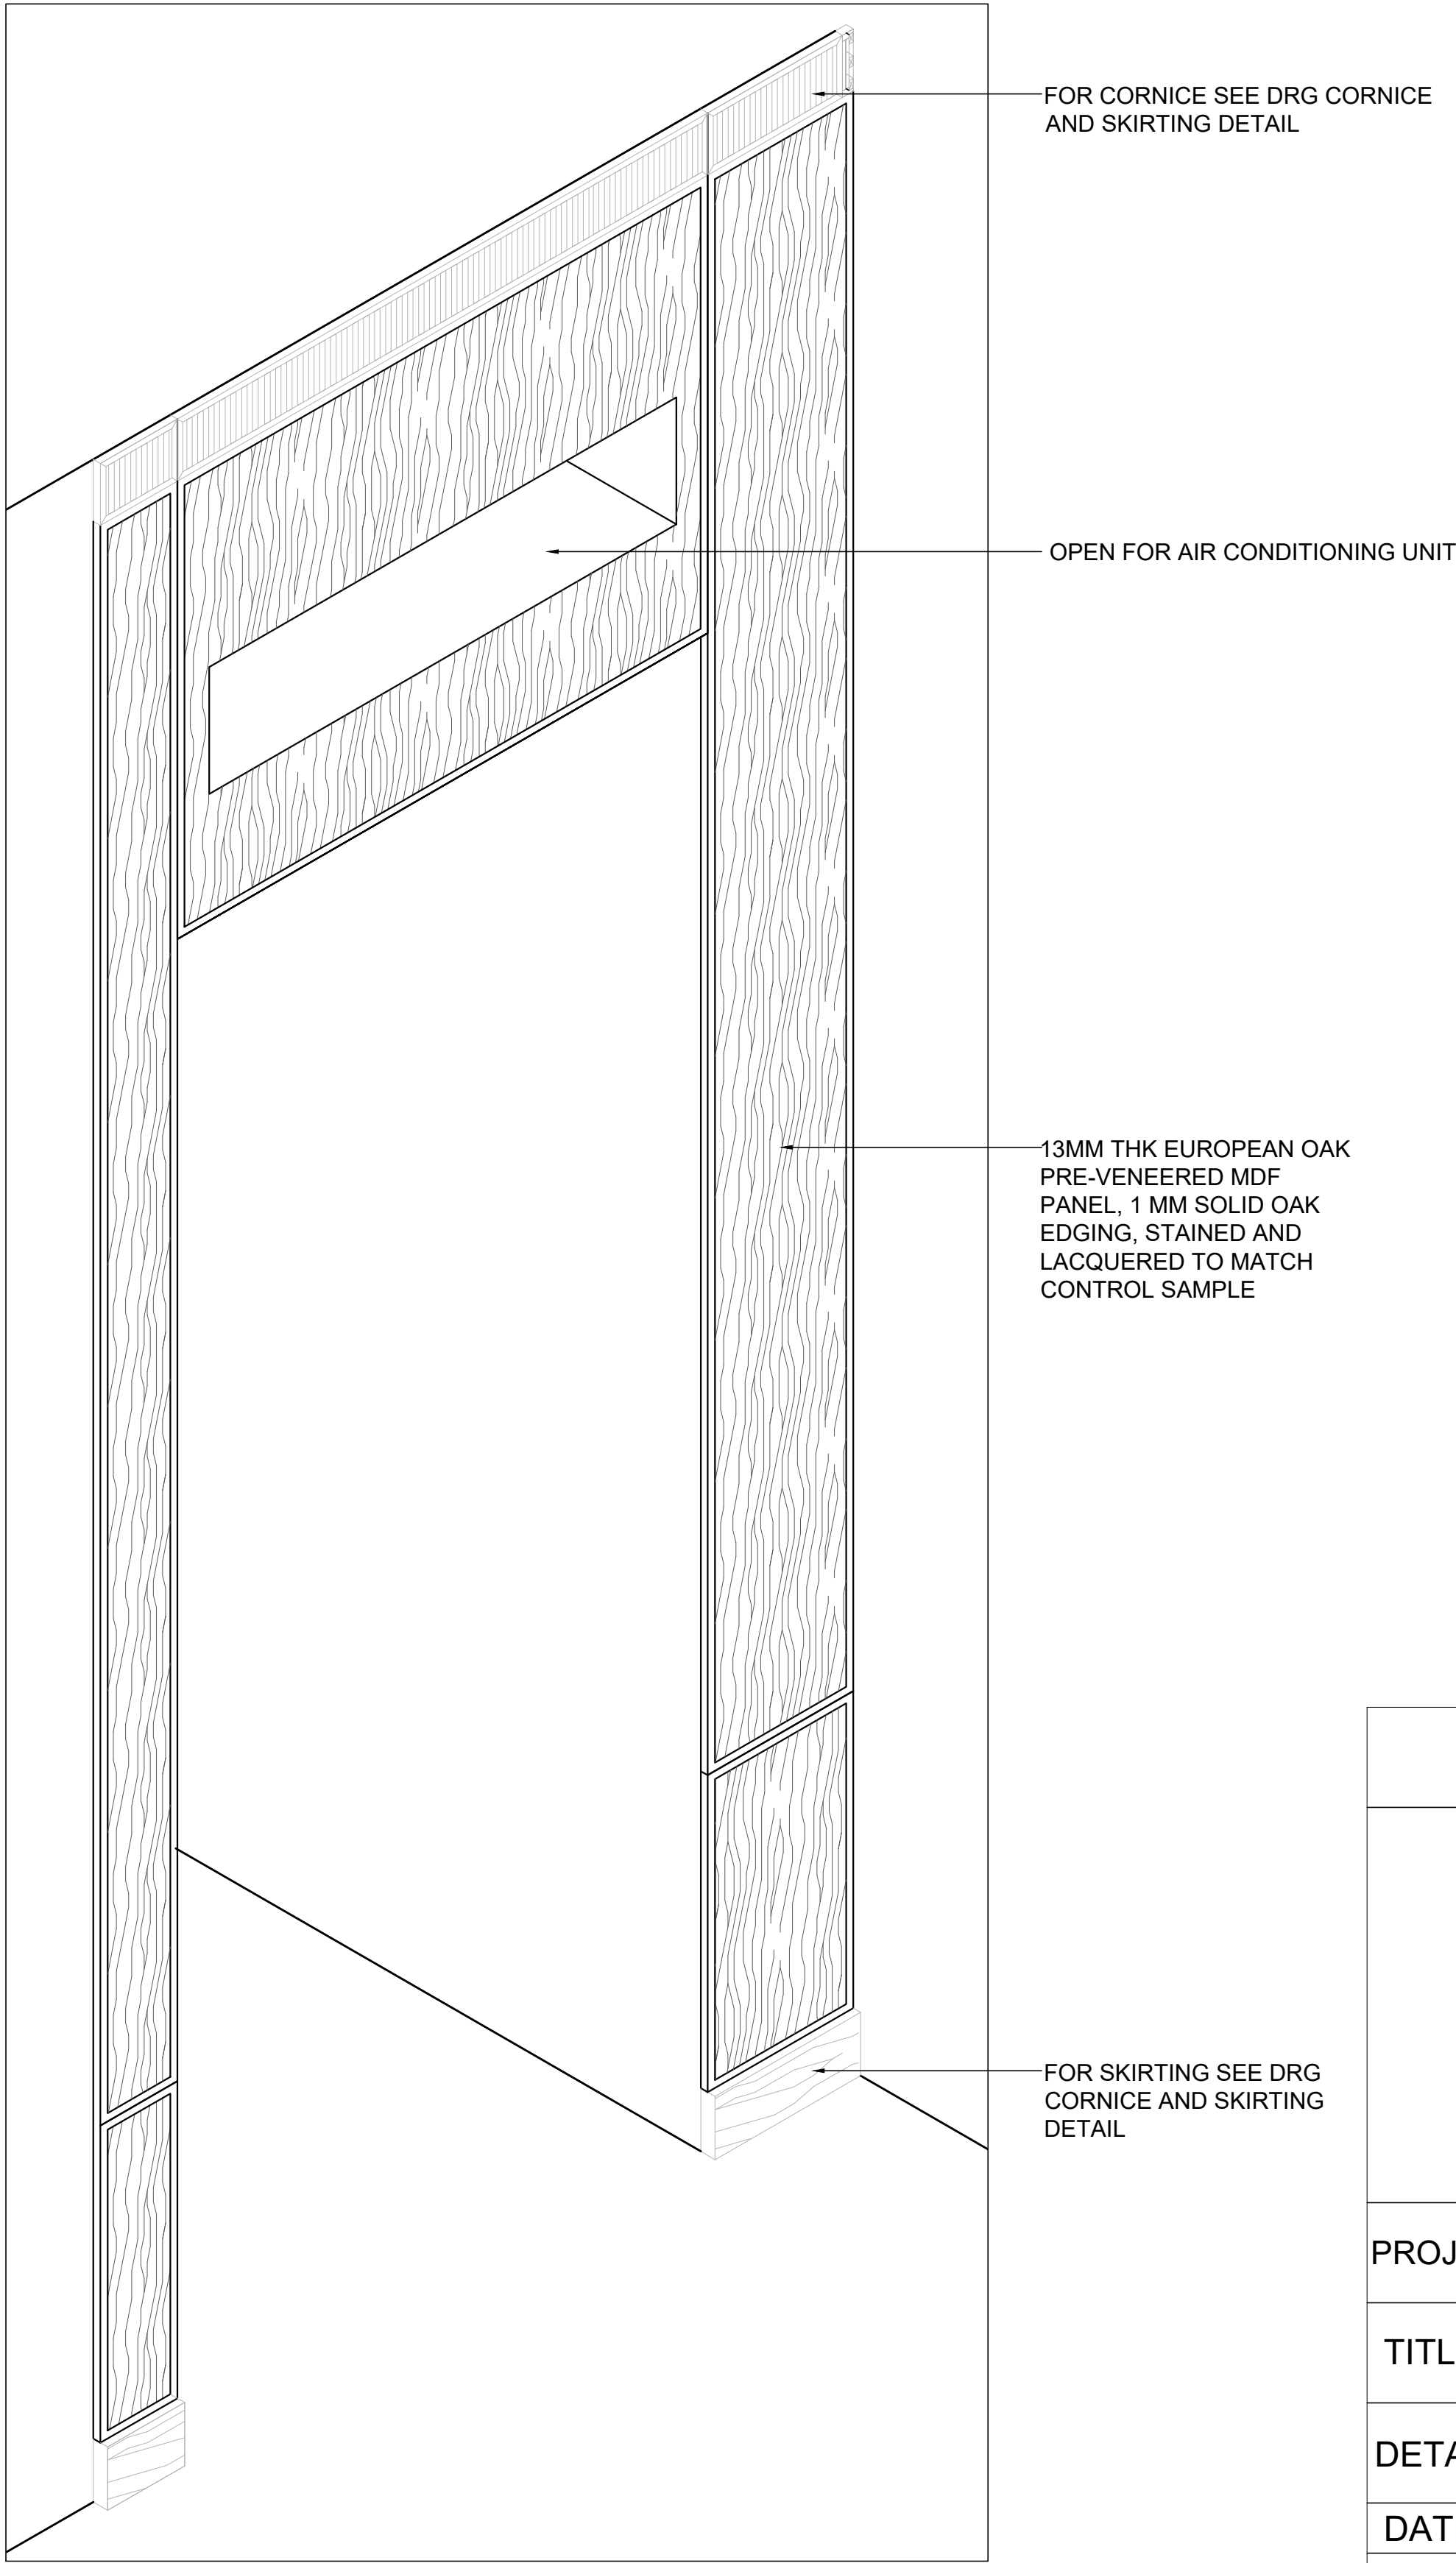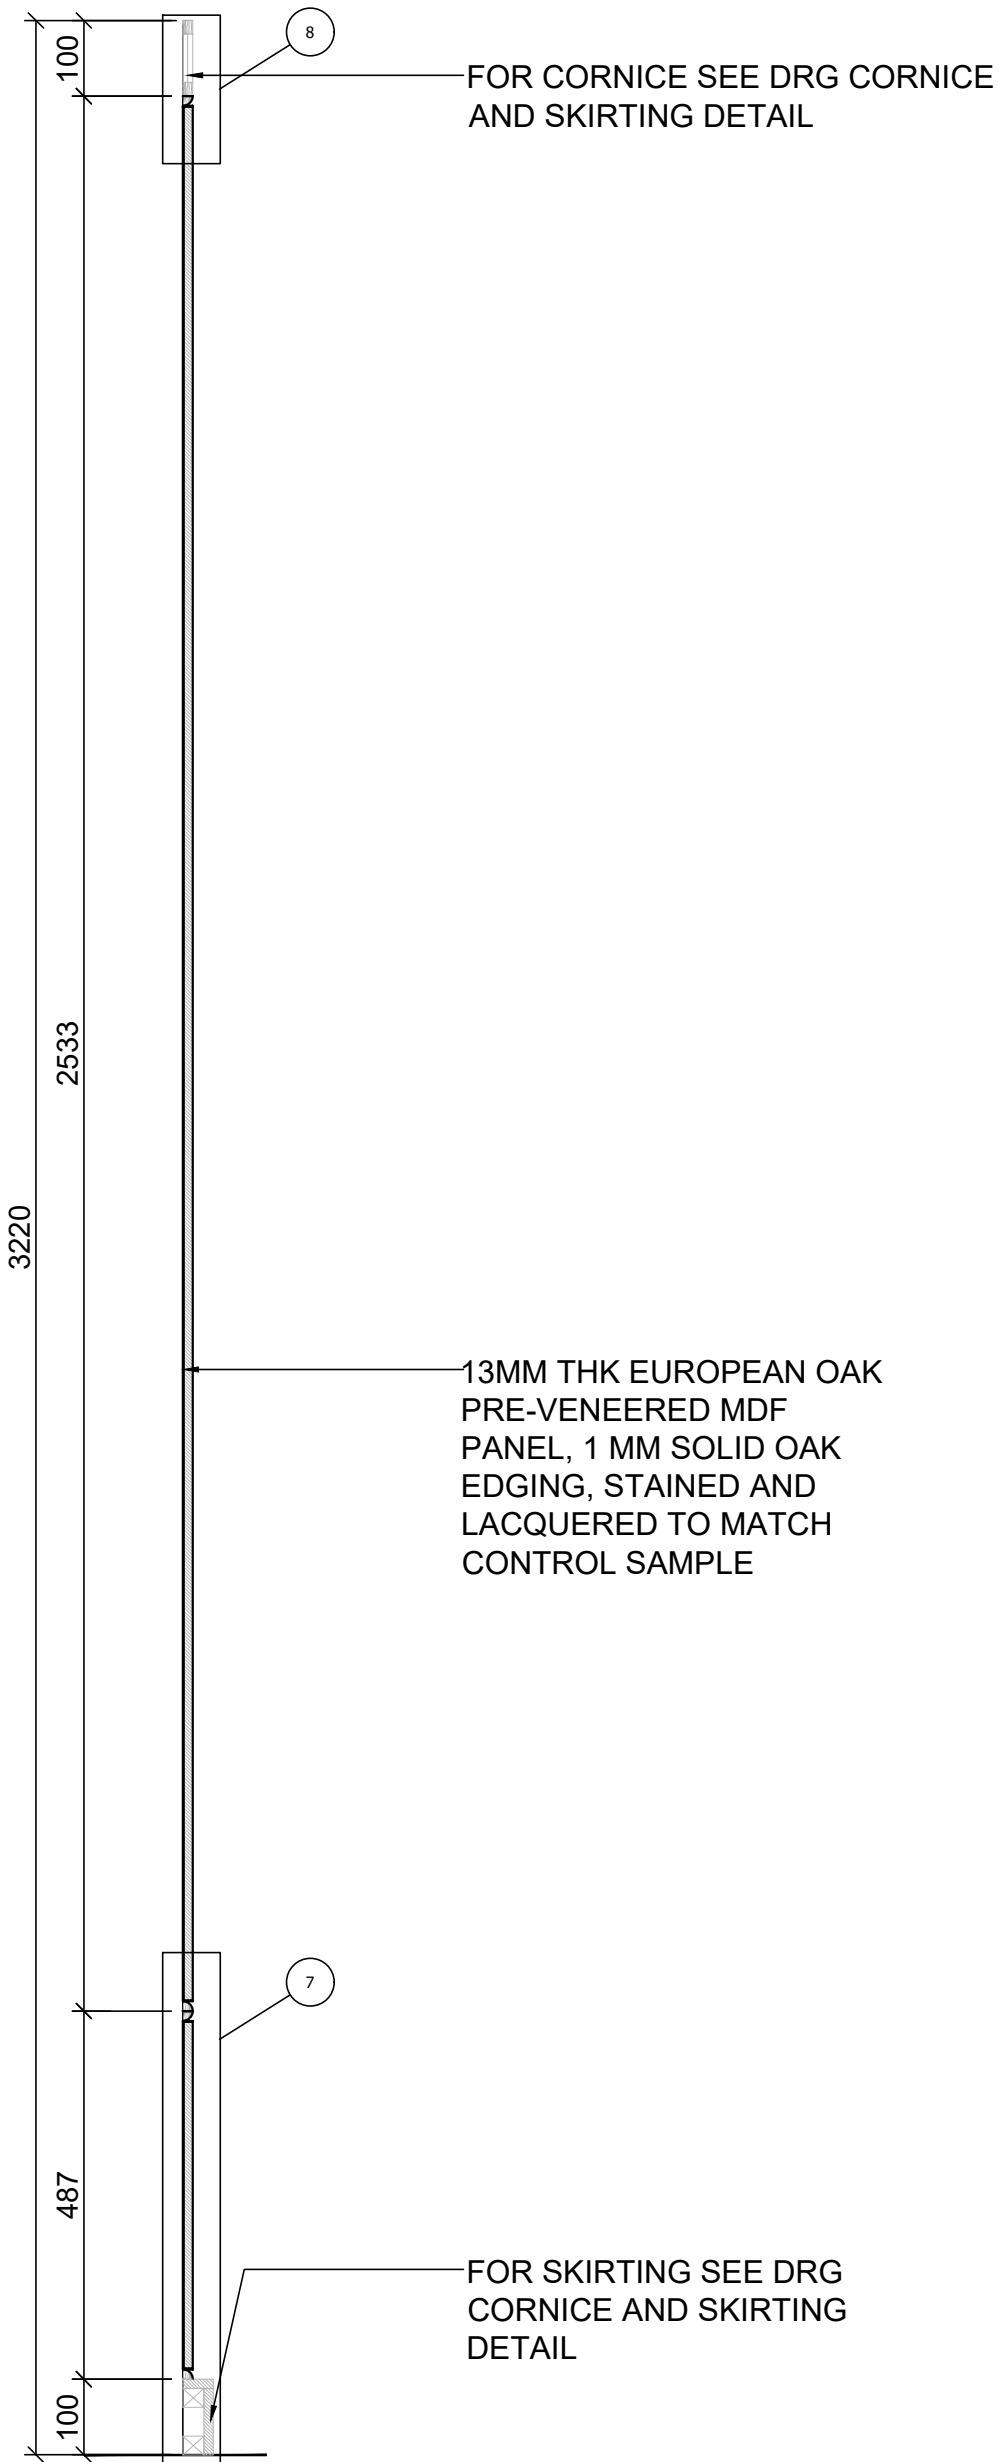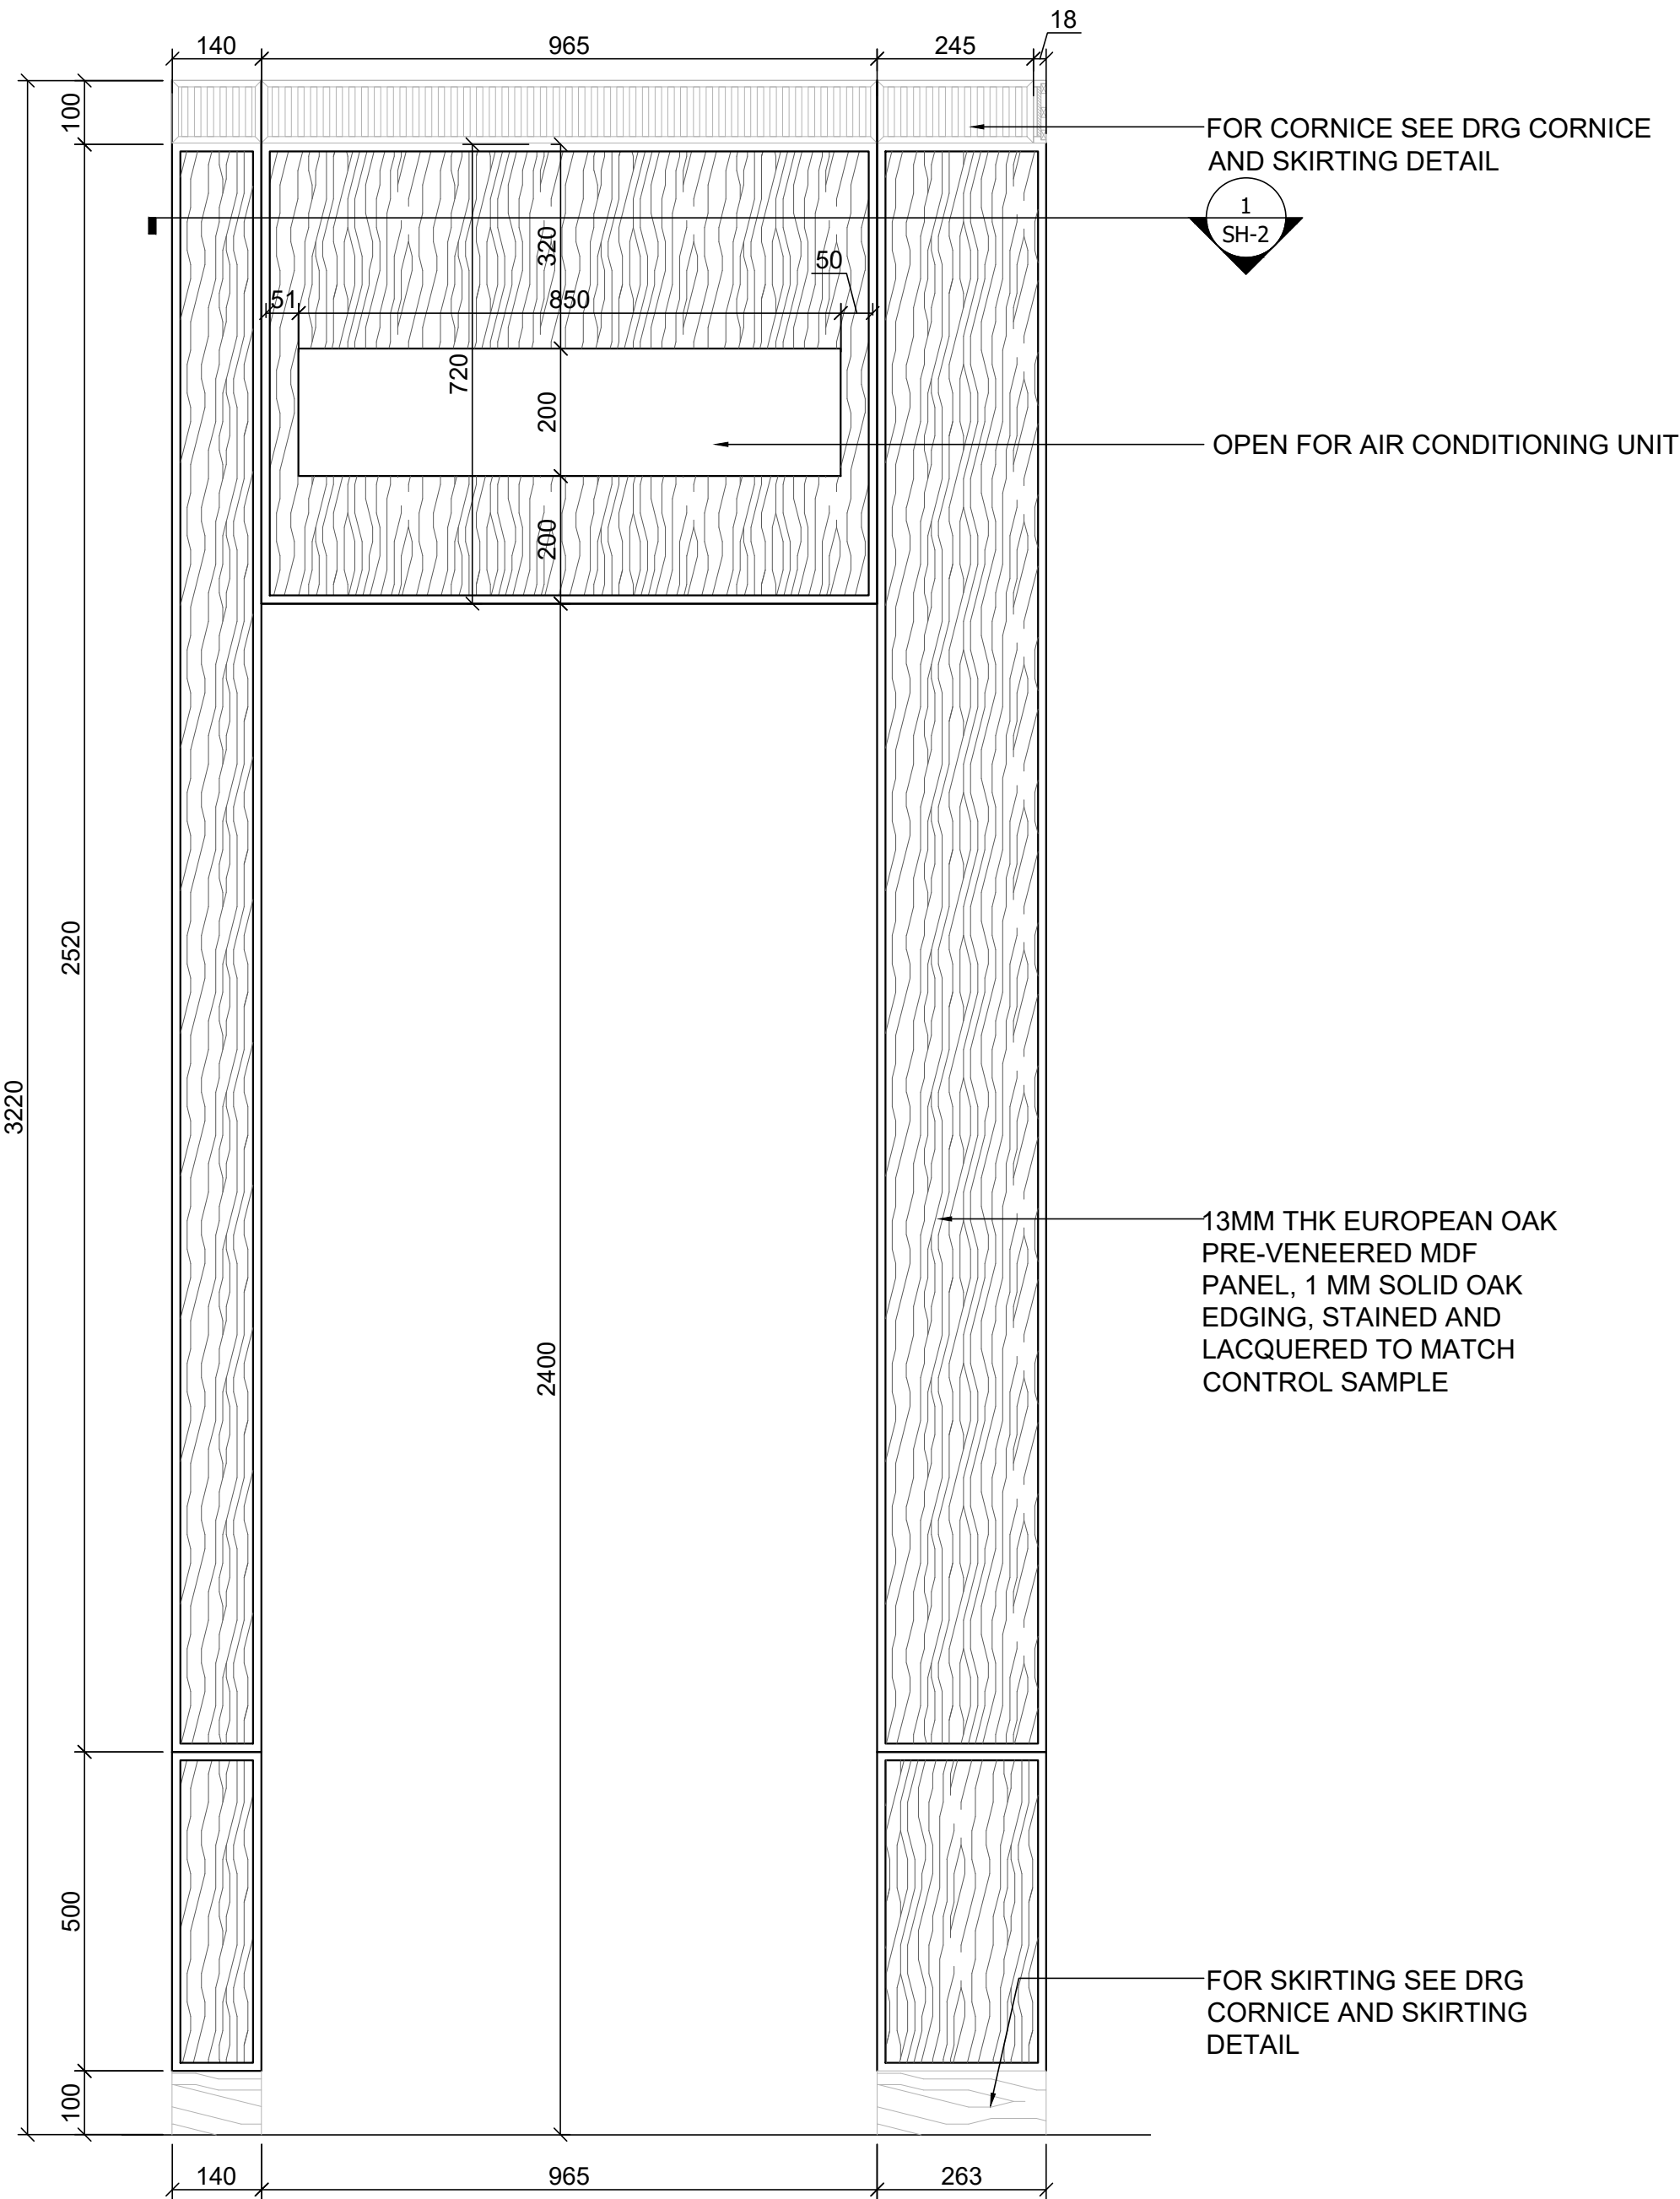

FOR APPROVAL	
PROJECT:	STW2732
TITLE:	JXX - ARCH WALL PANEL
DETAILS:	PLAN, ELEV. & SECTION
DATE:	03/23/2026
SHEET:	2 OF 3
DRAWN:	JPO
CHECK:	ACA
SCALE:	AS SHOWN @ A1
DRAWING N°:	STW2732- JXX- 02
REVISION:	00

REVISION HISTORY		
REV	DESCRIPTION	DATE
	FIRST ISSUE	03/23/2026

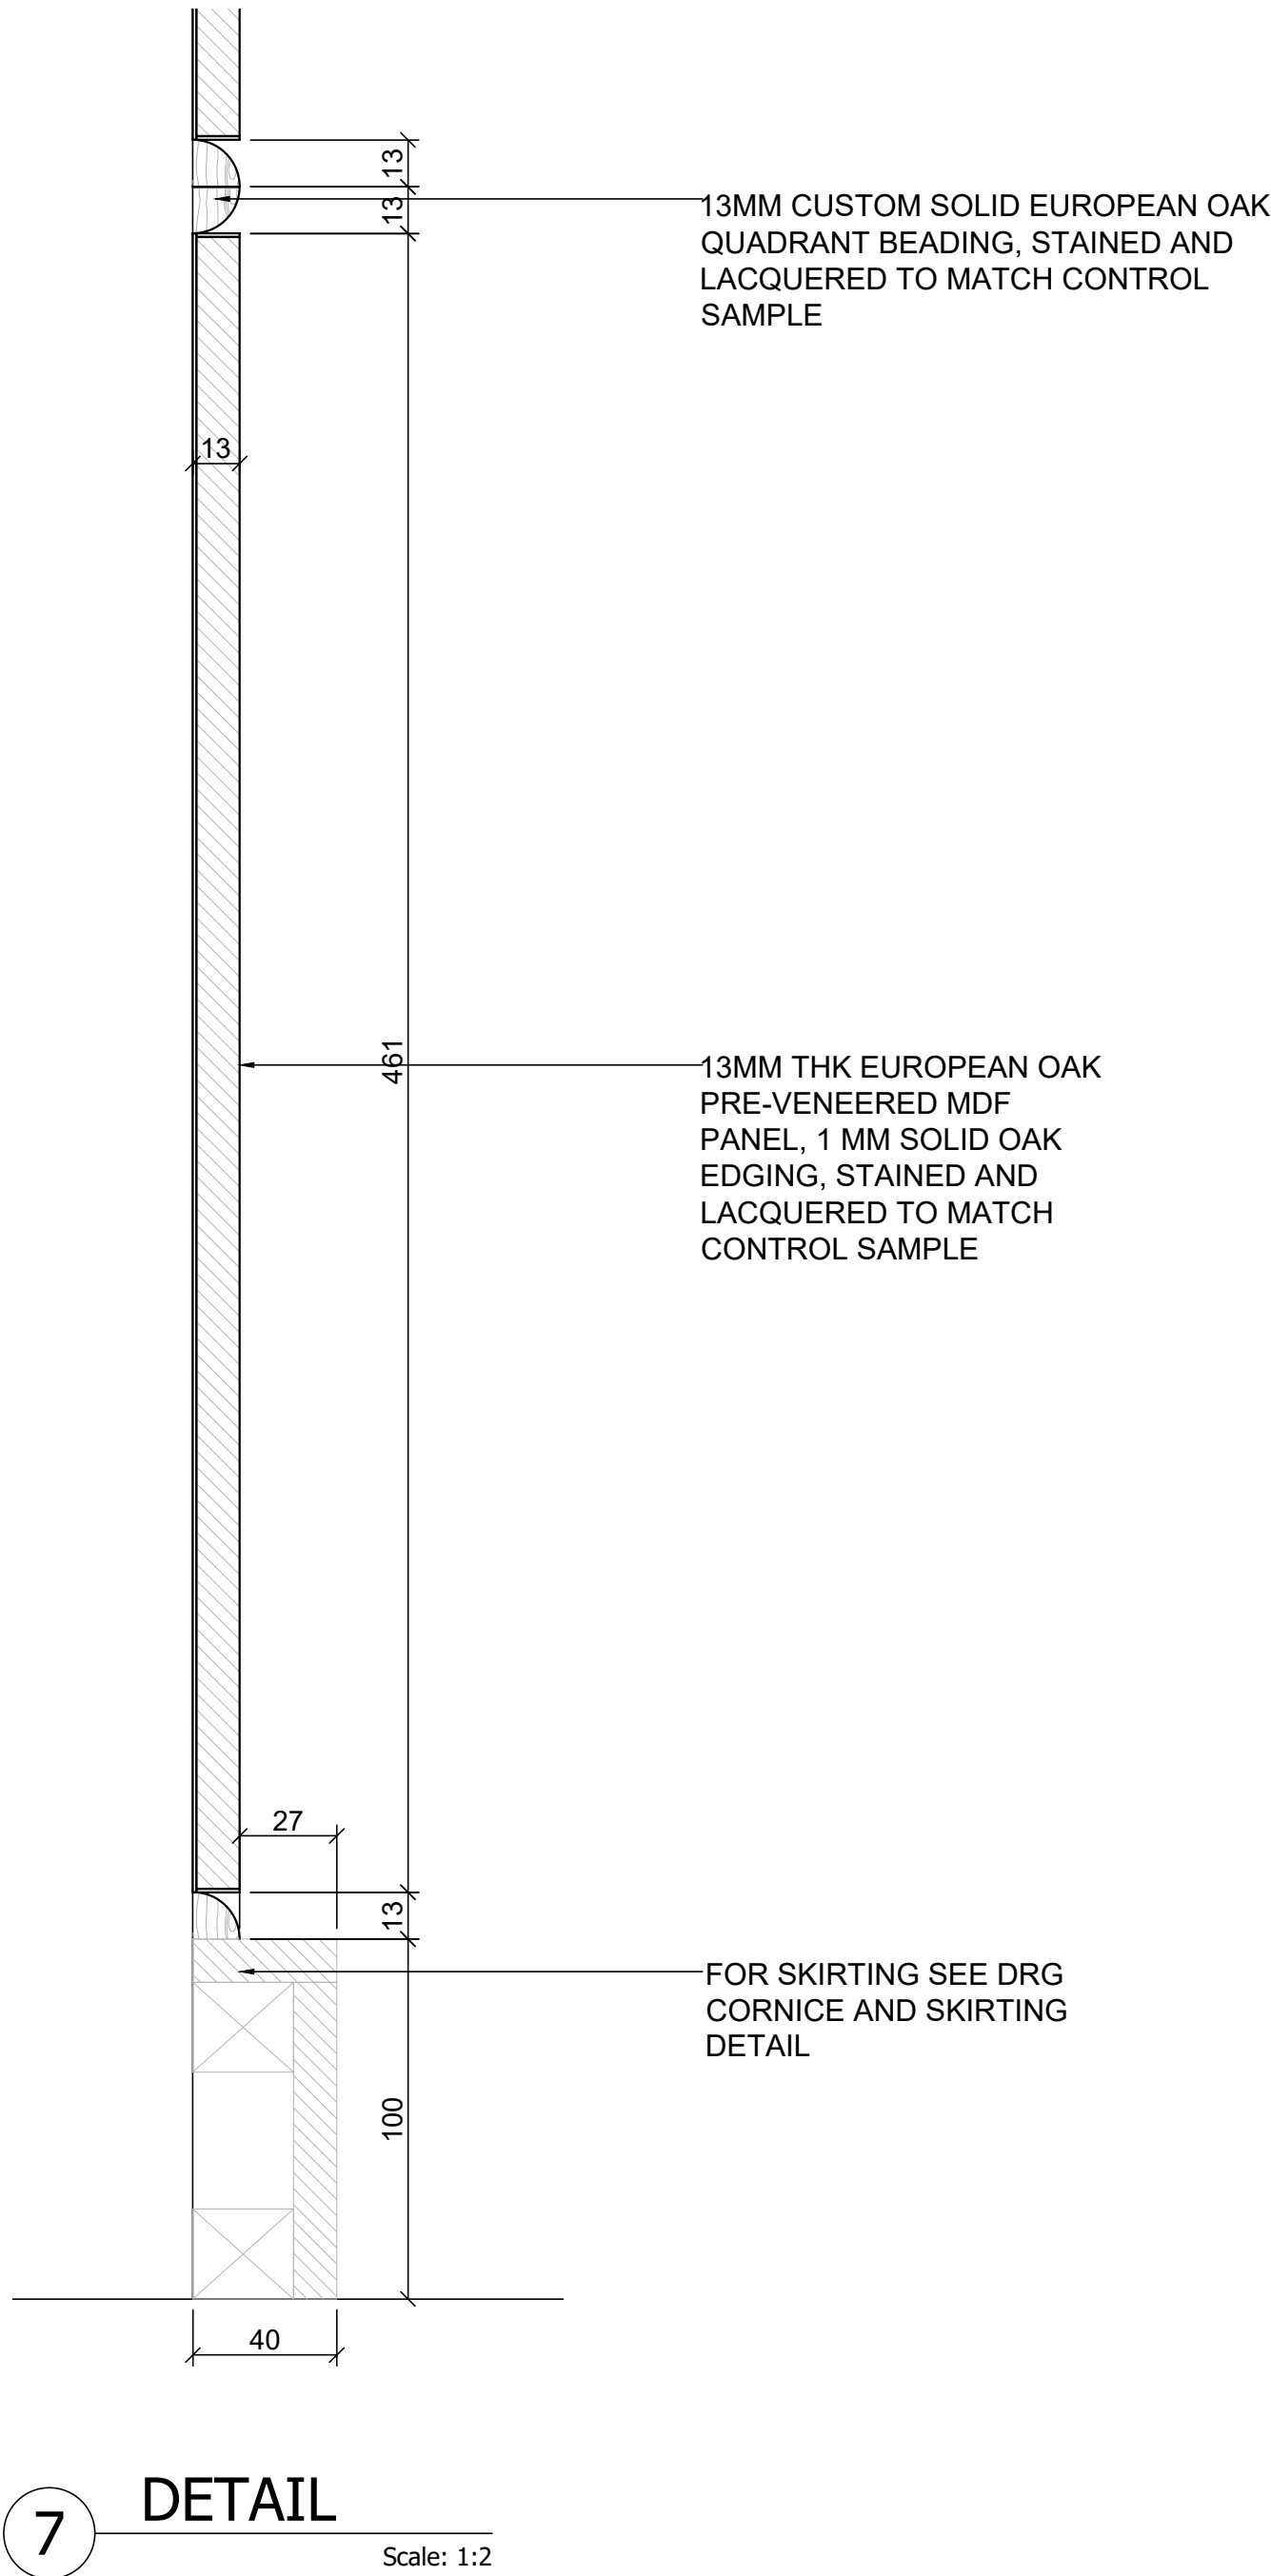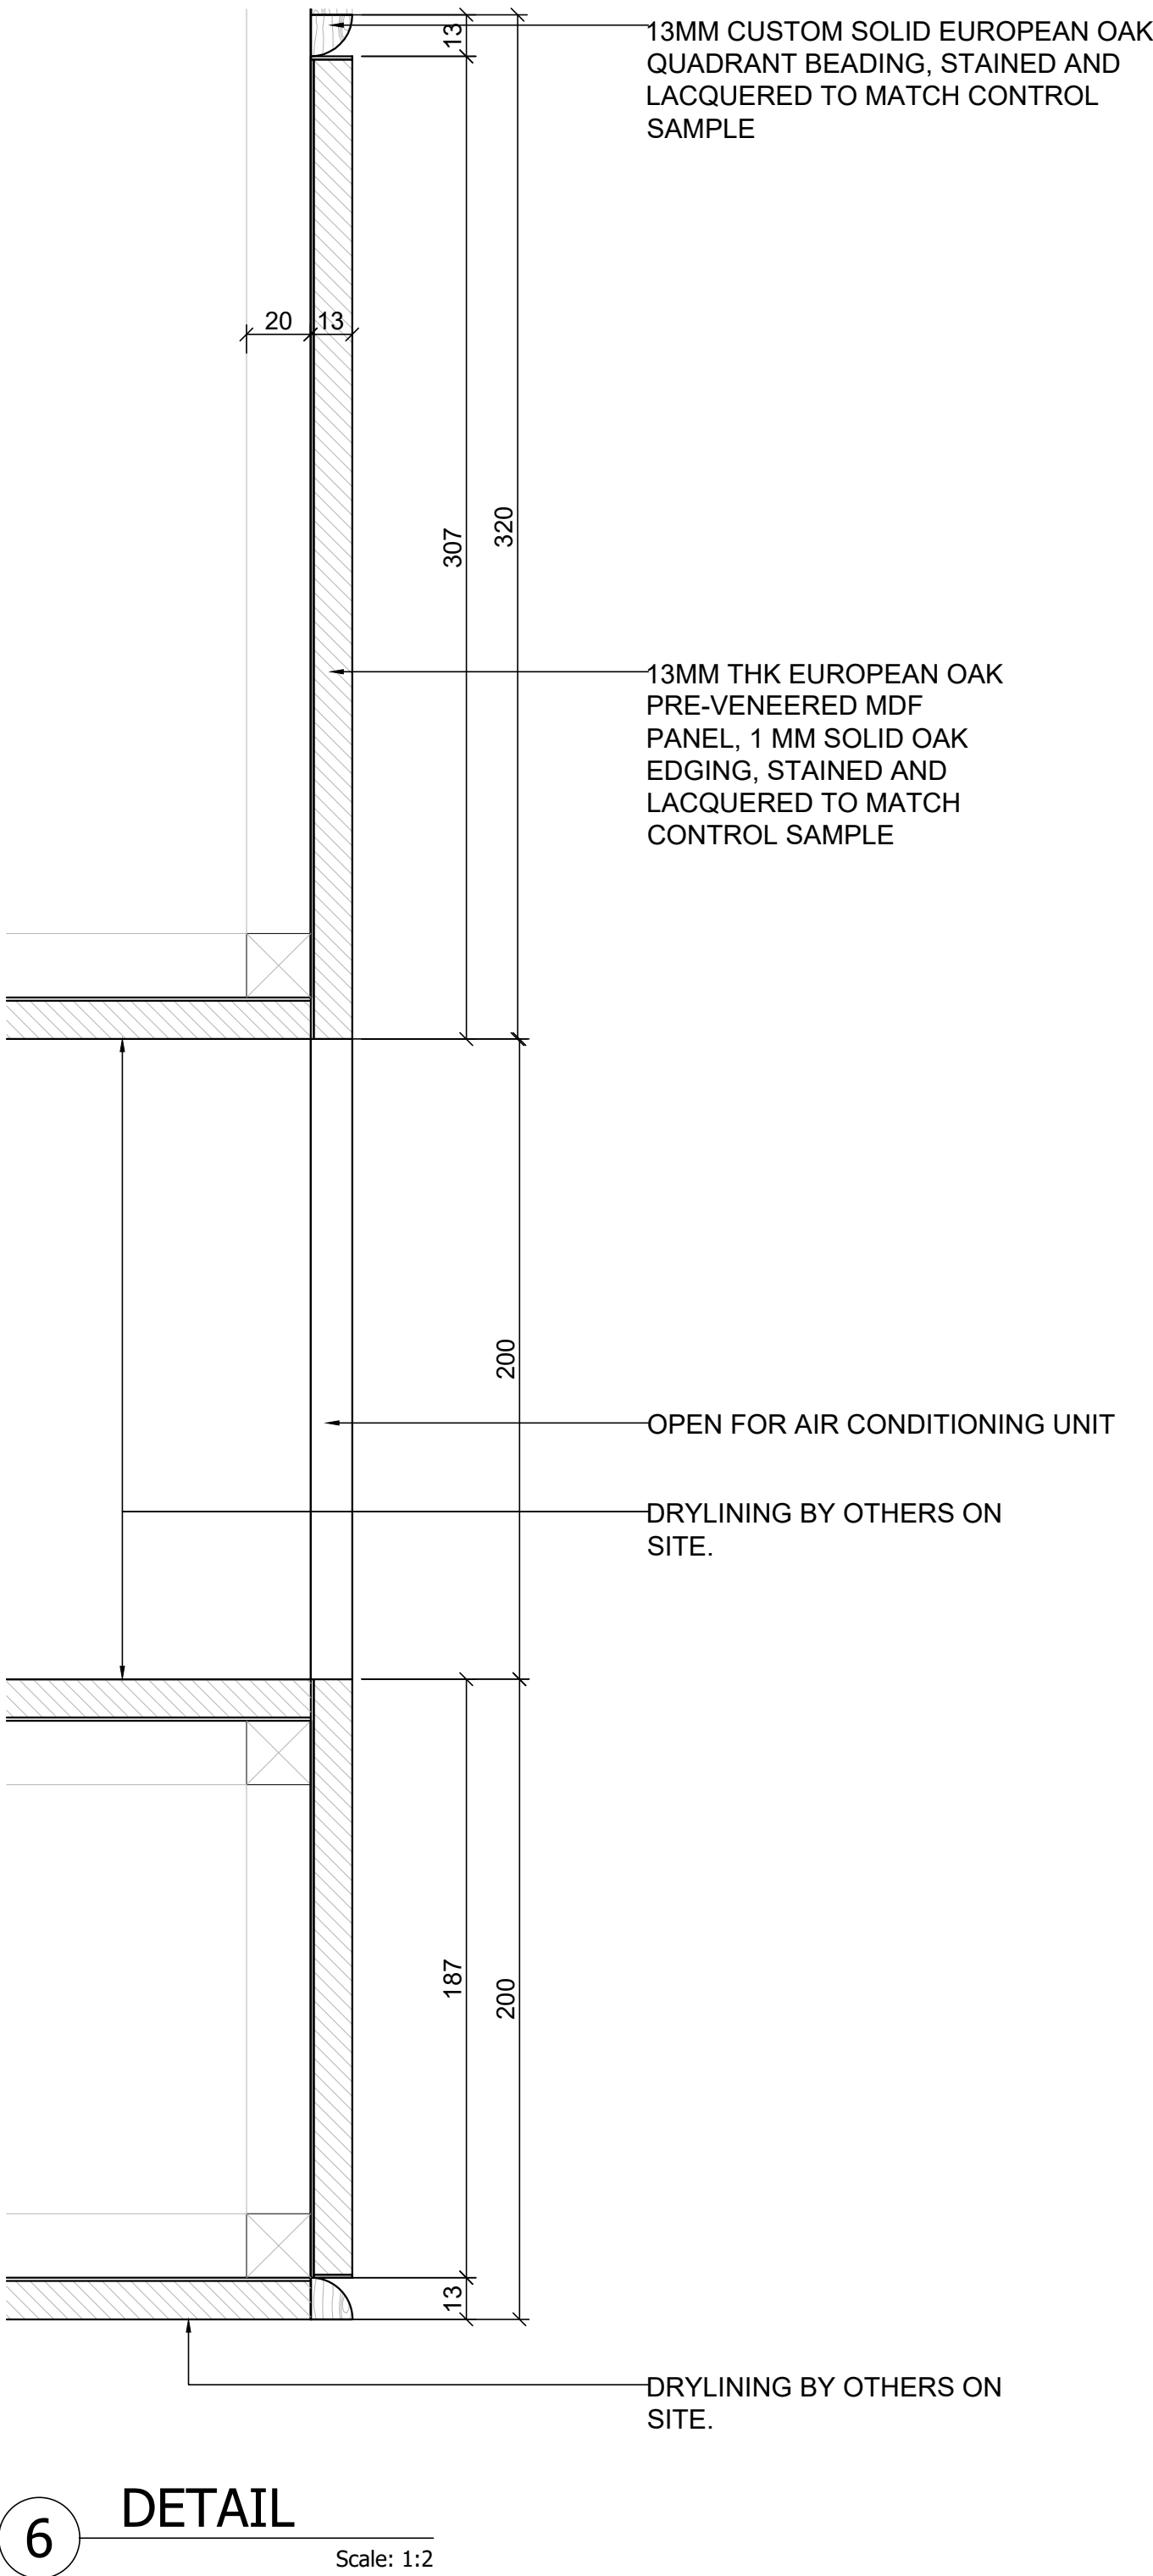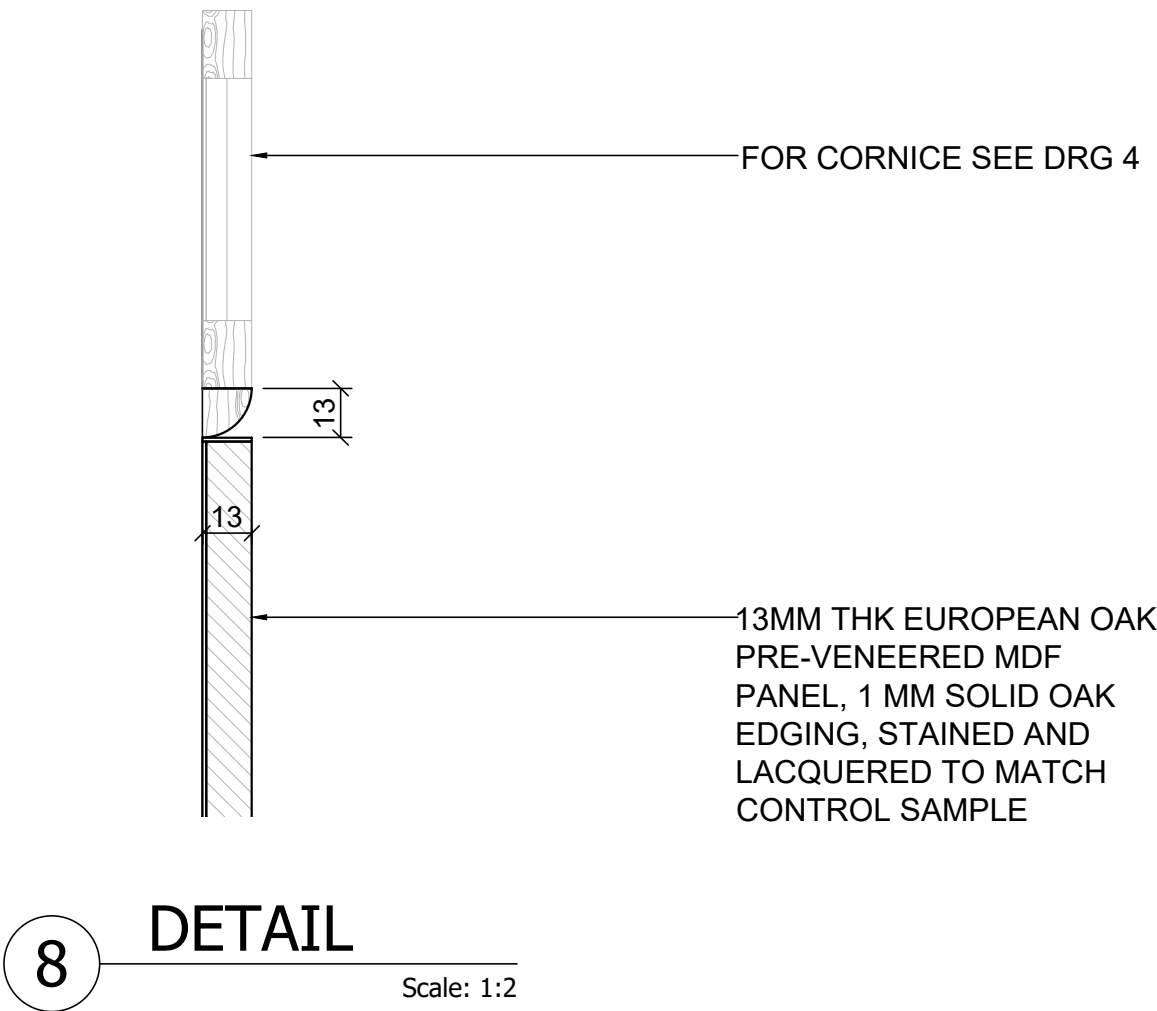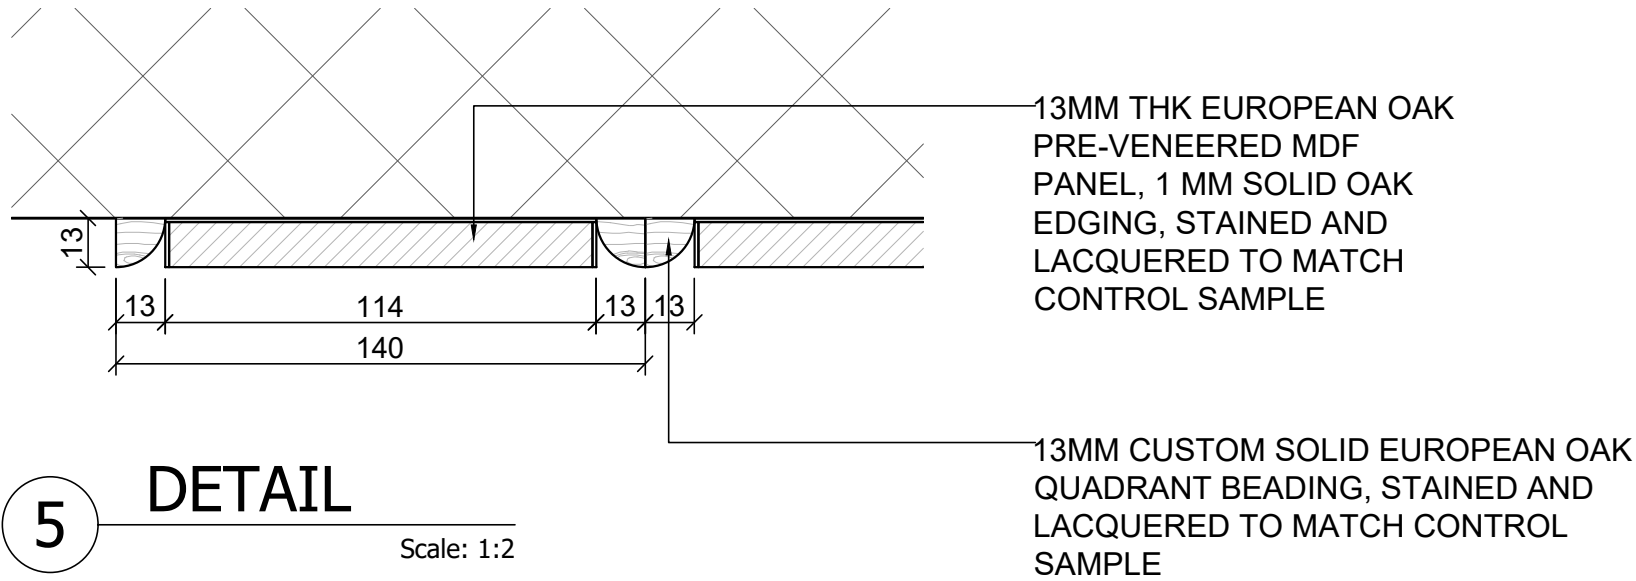

FOR APPROVAL	
PROJECT:	STW2732
TITLE:	JXX - ARCH WALL PANEL
DETAILS:	DETAILS
DATE:	03/23/2026
SHEET:	3 OF 3
DRAWN:	JPO
CHECK:	ACA
SCALE:	AS SHOWN @ A1
DRAWING N°:	REVISION:
STW2732- JXX- 03	00