




REVISION HISTORY		
REV	DESCRIPTION	DATE
	FIRST ISSUE	04/30/2026

FOR APPROVAL



PROJECT:	STW2872	
TITLE:	JXX - CAFE BAR	
DETAILS:	RENDERING	
DATE:	04/30/2026	
SHEET:	1 OF 5	
DRAWN:	JPO	
CHECK:	ACA	
SCALE:	AS SHOWN @ A1	
DRAWING N°:	REVISION:	
STW2872– JXX– 01	00	

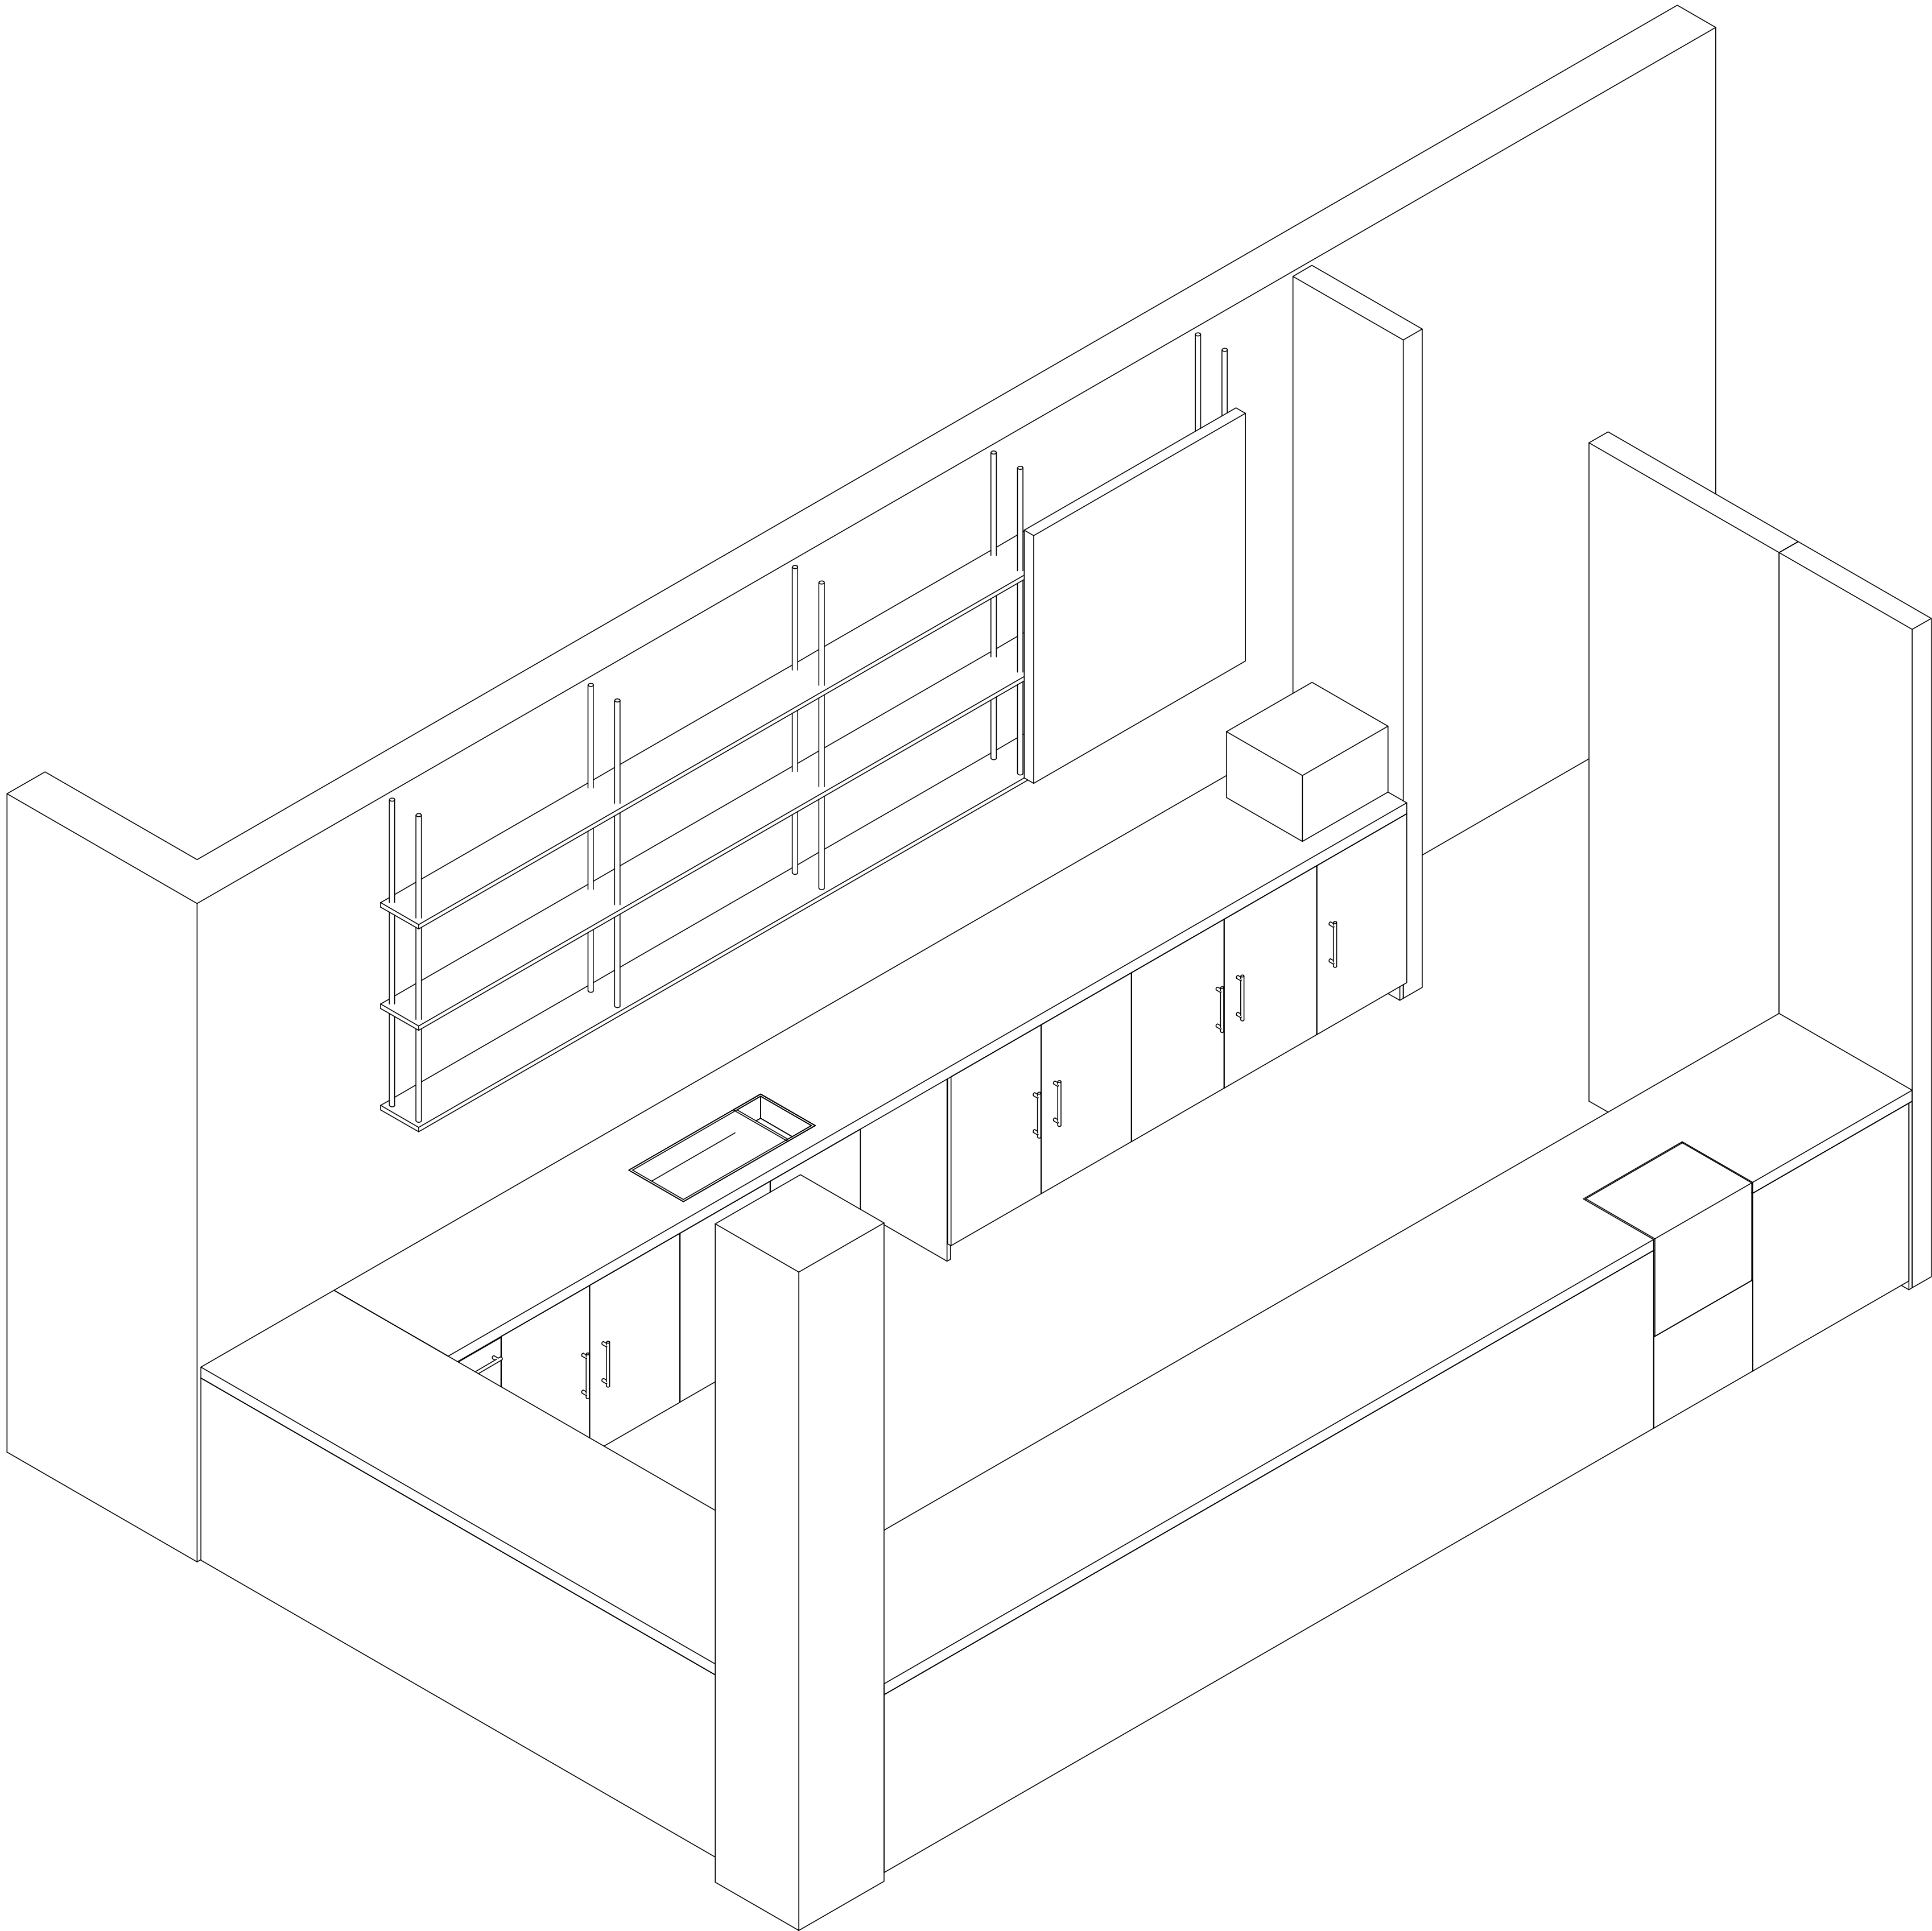


REVISION HISTORY		
REV	DESCRIPTION	DATE
	FIRST ISSUE	04/30/2026

FOR APPROVAL




PROJECT:	STW2872	
TITLE:	JXX - CAFE BAR	
DETAILS:	ISOMETRIC	
DATE:	04/30/2026	
SHEET:	2 OF 5	
DRAWN:	JPO	
CHECK:	ACA	
SCALE:	AS SHOWN @ A1	
DRAWING N°:	REVISION:	
STW2872– JXX– 02	00	


REVISION HISTORY		
REV	DESCRIPTION	DATE
	FIRST ISSUE	04/30/2026

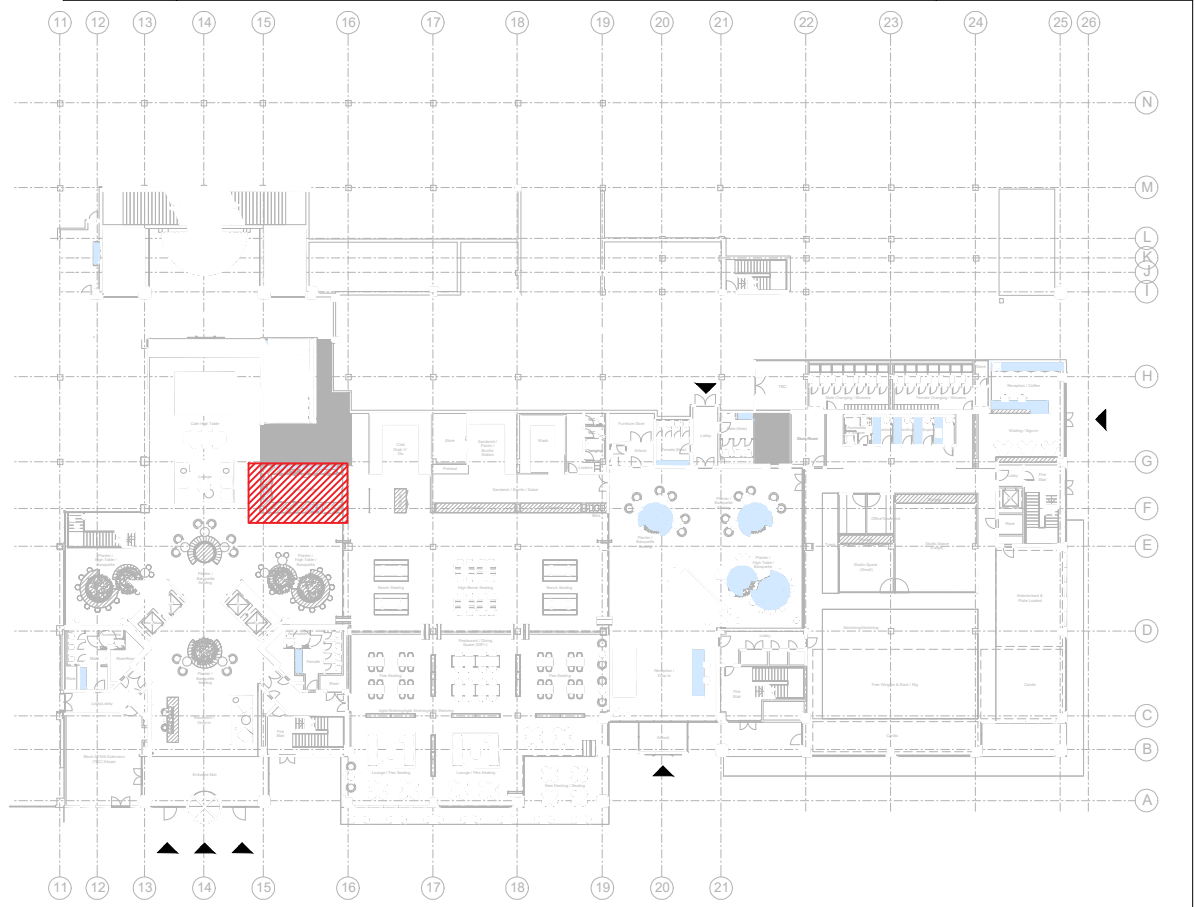


KEYPLAN

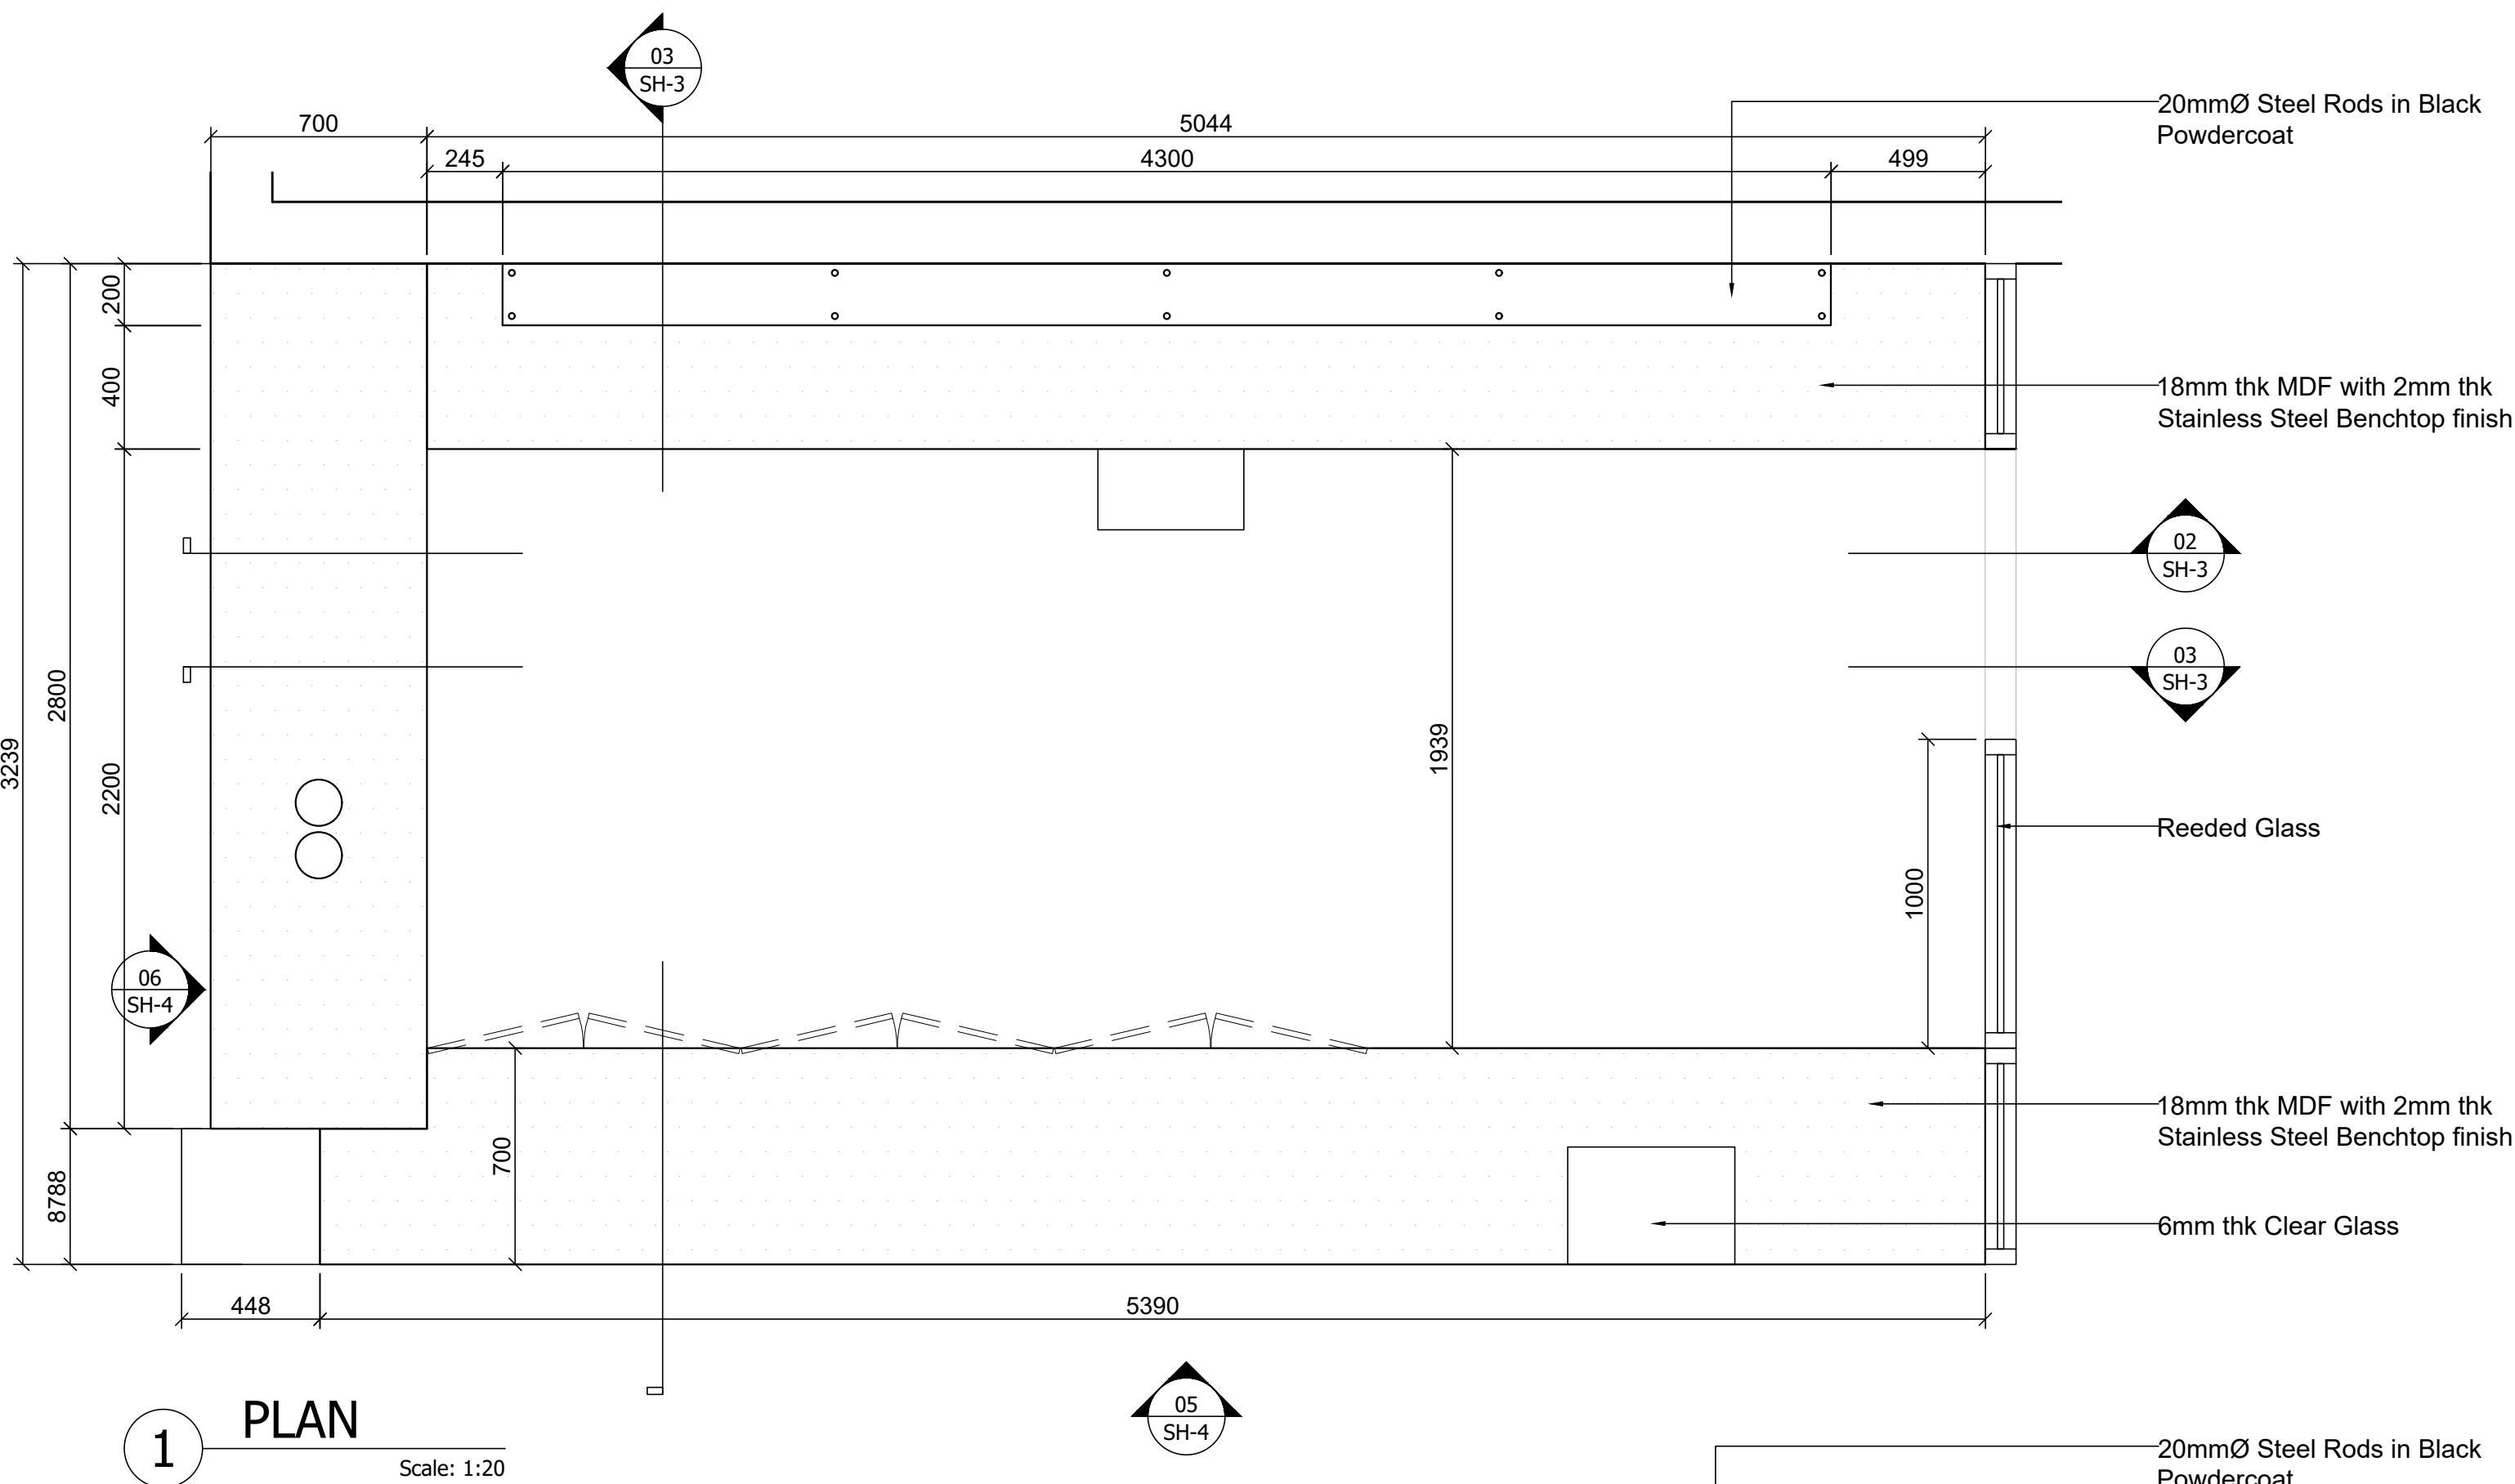


1 PLAN
Scale: 1:20

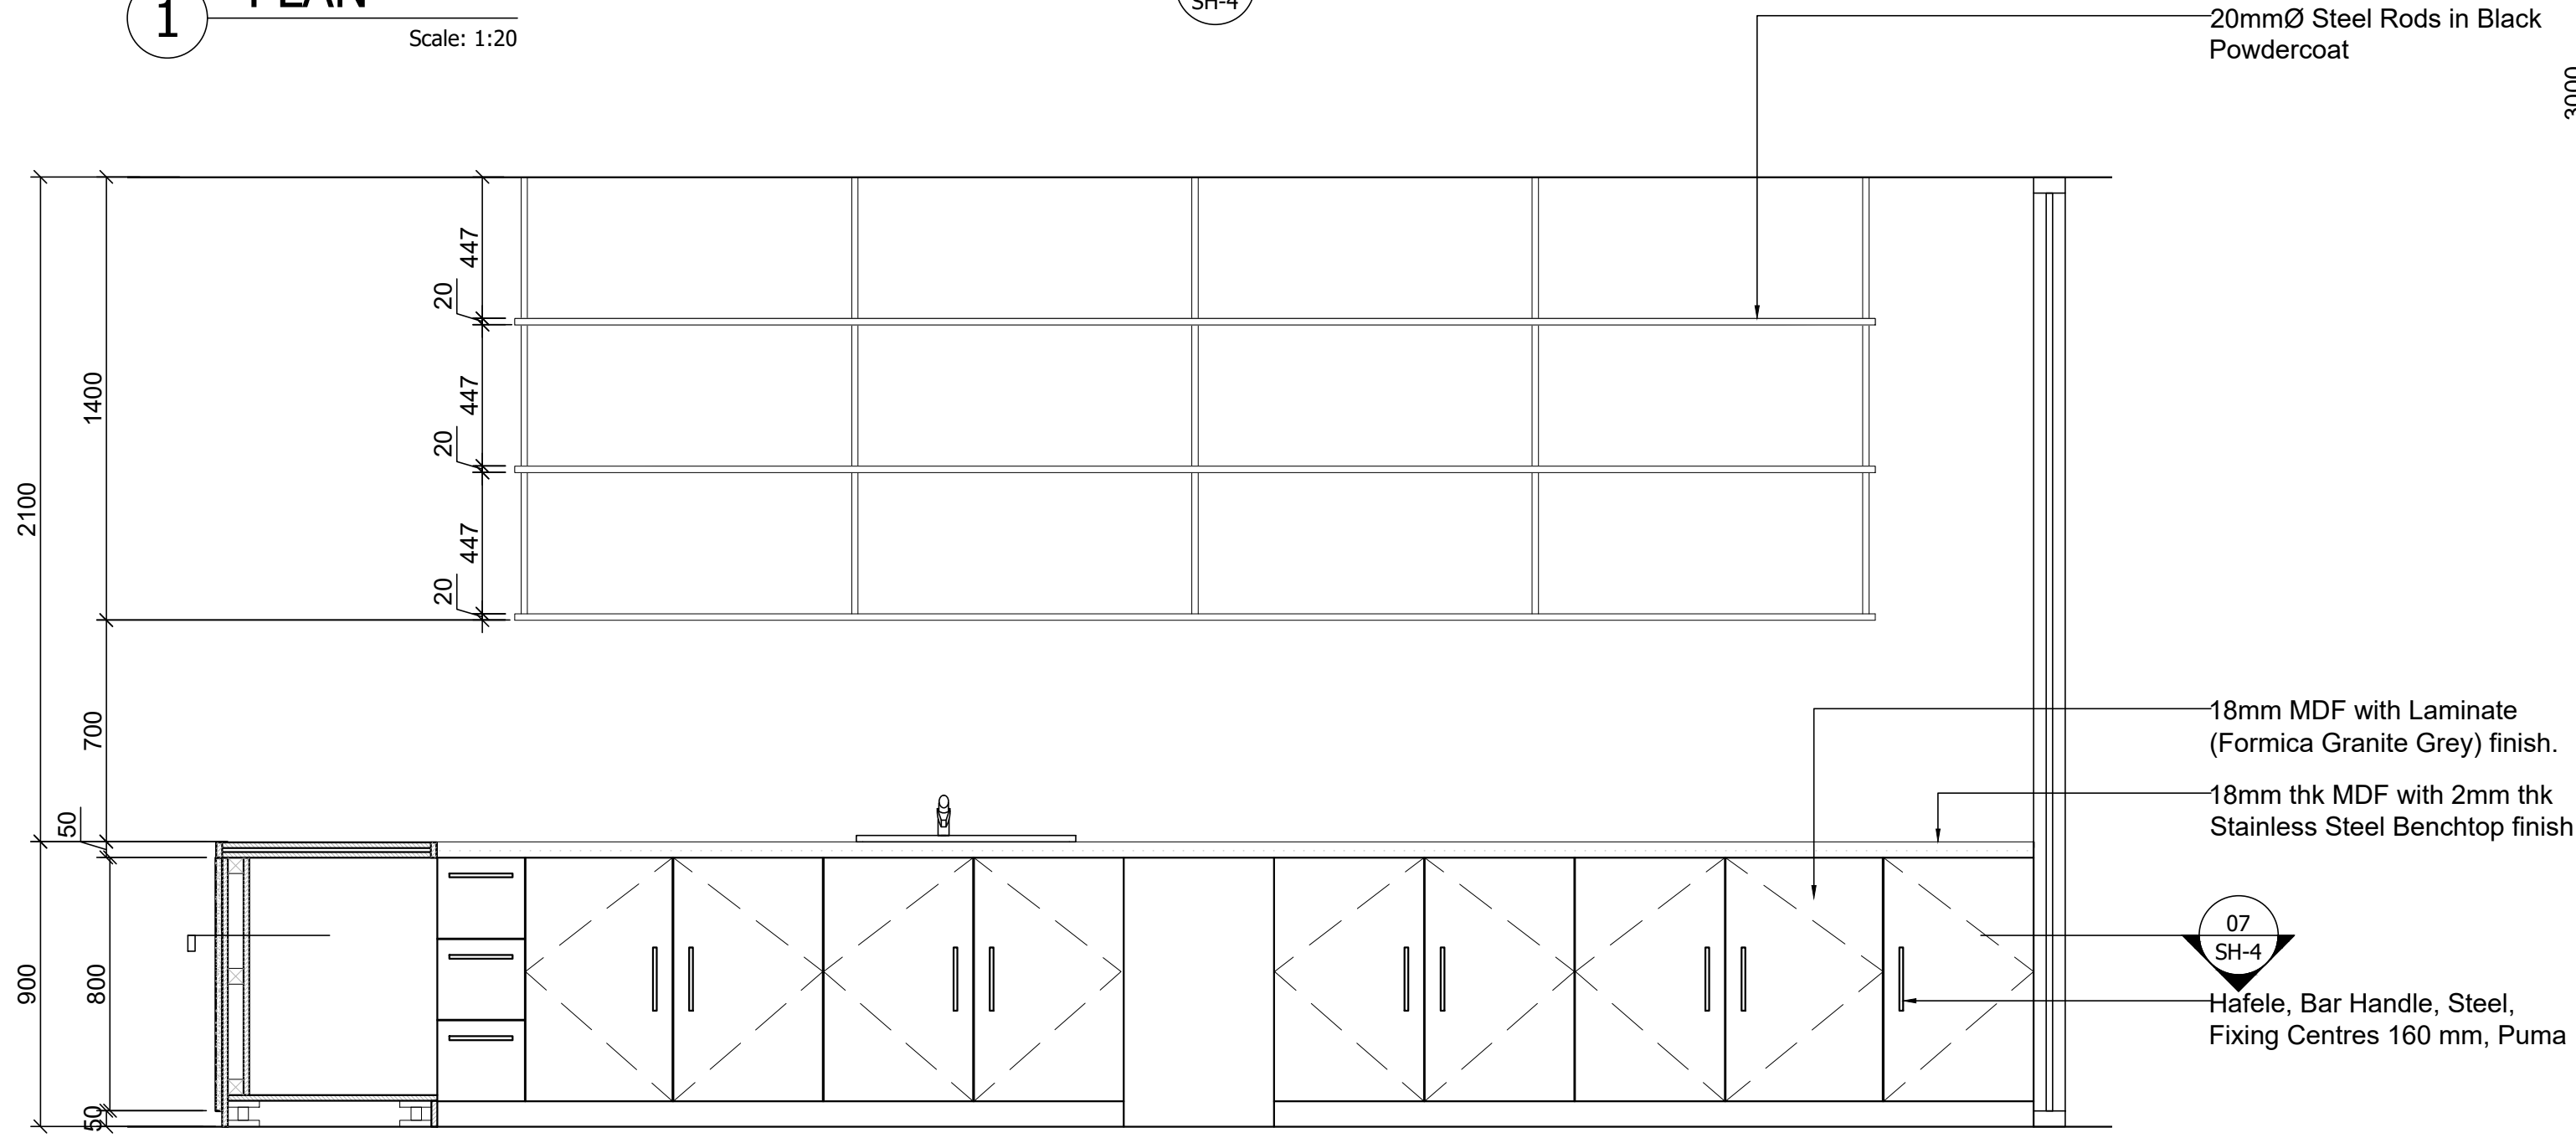

2 ELEVATION
Scale: 1:20

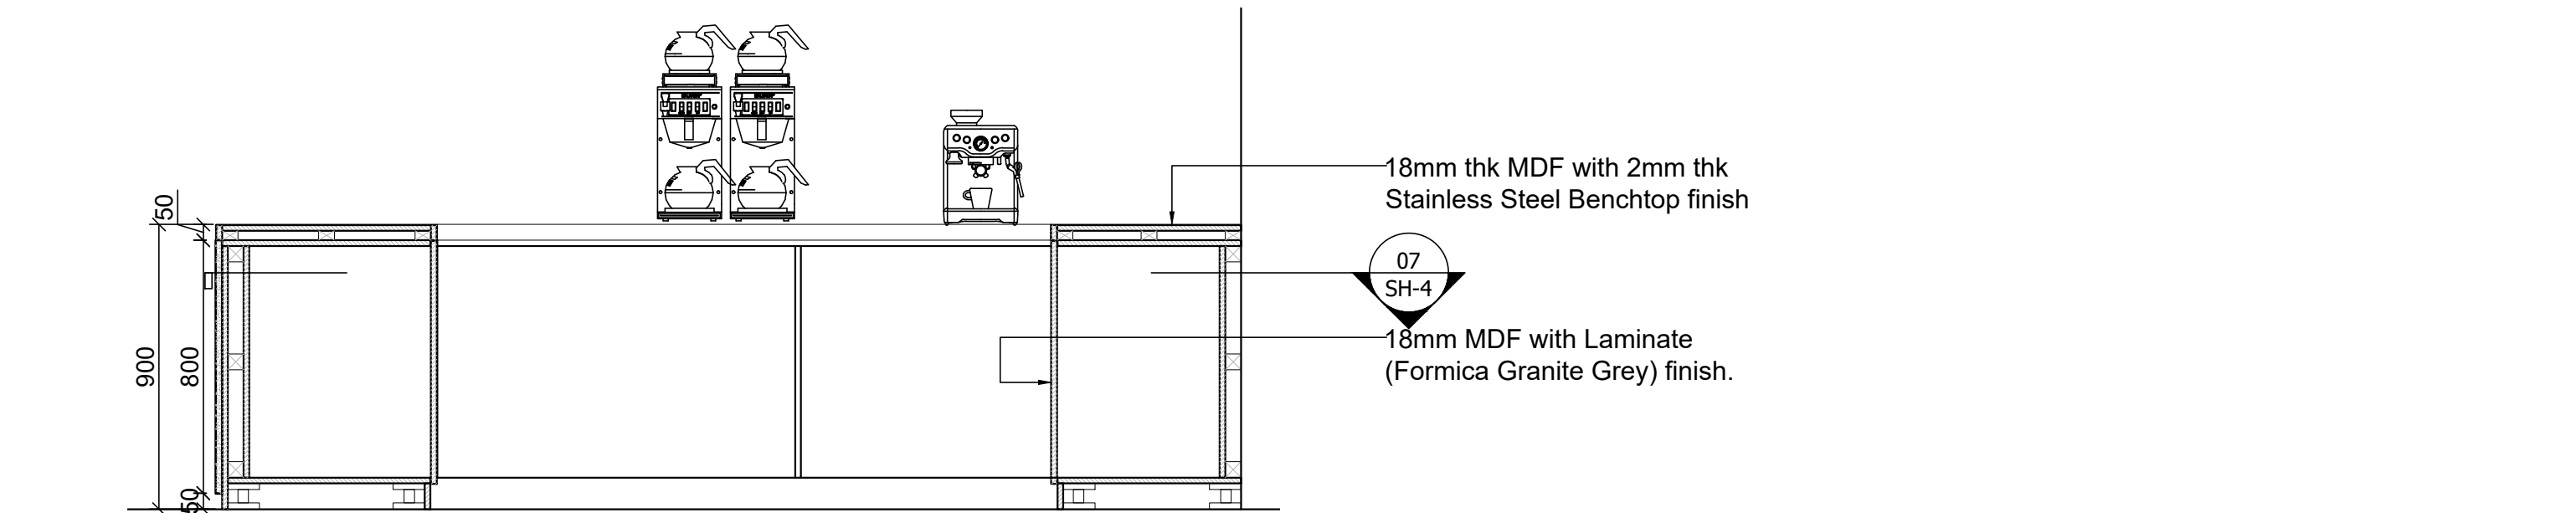

3 ELEVATION
Scale: 1:20

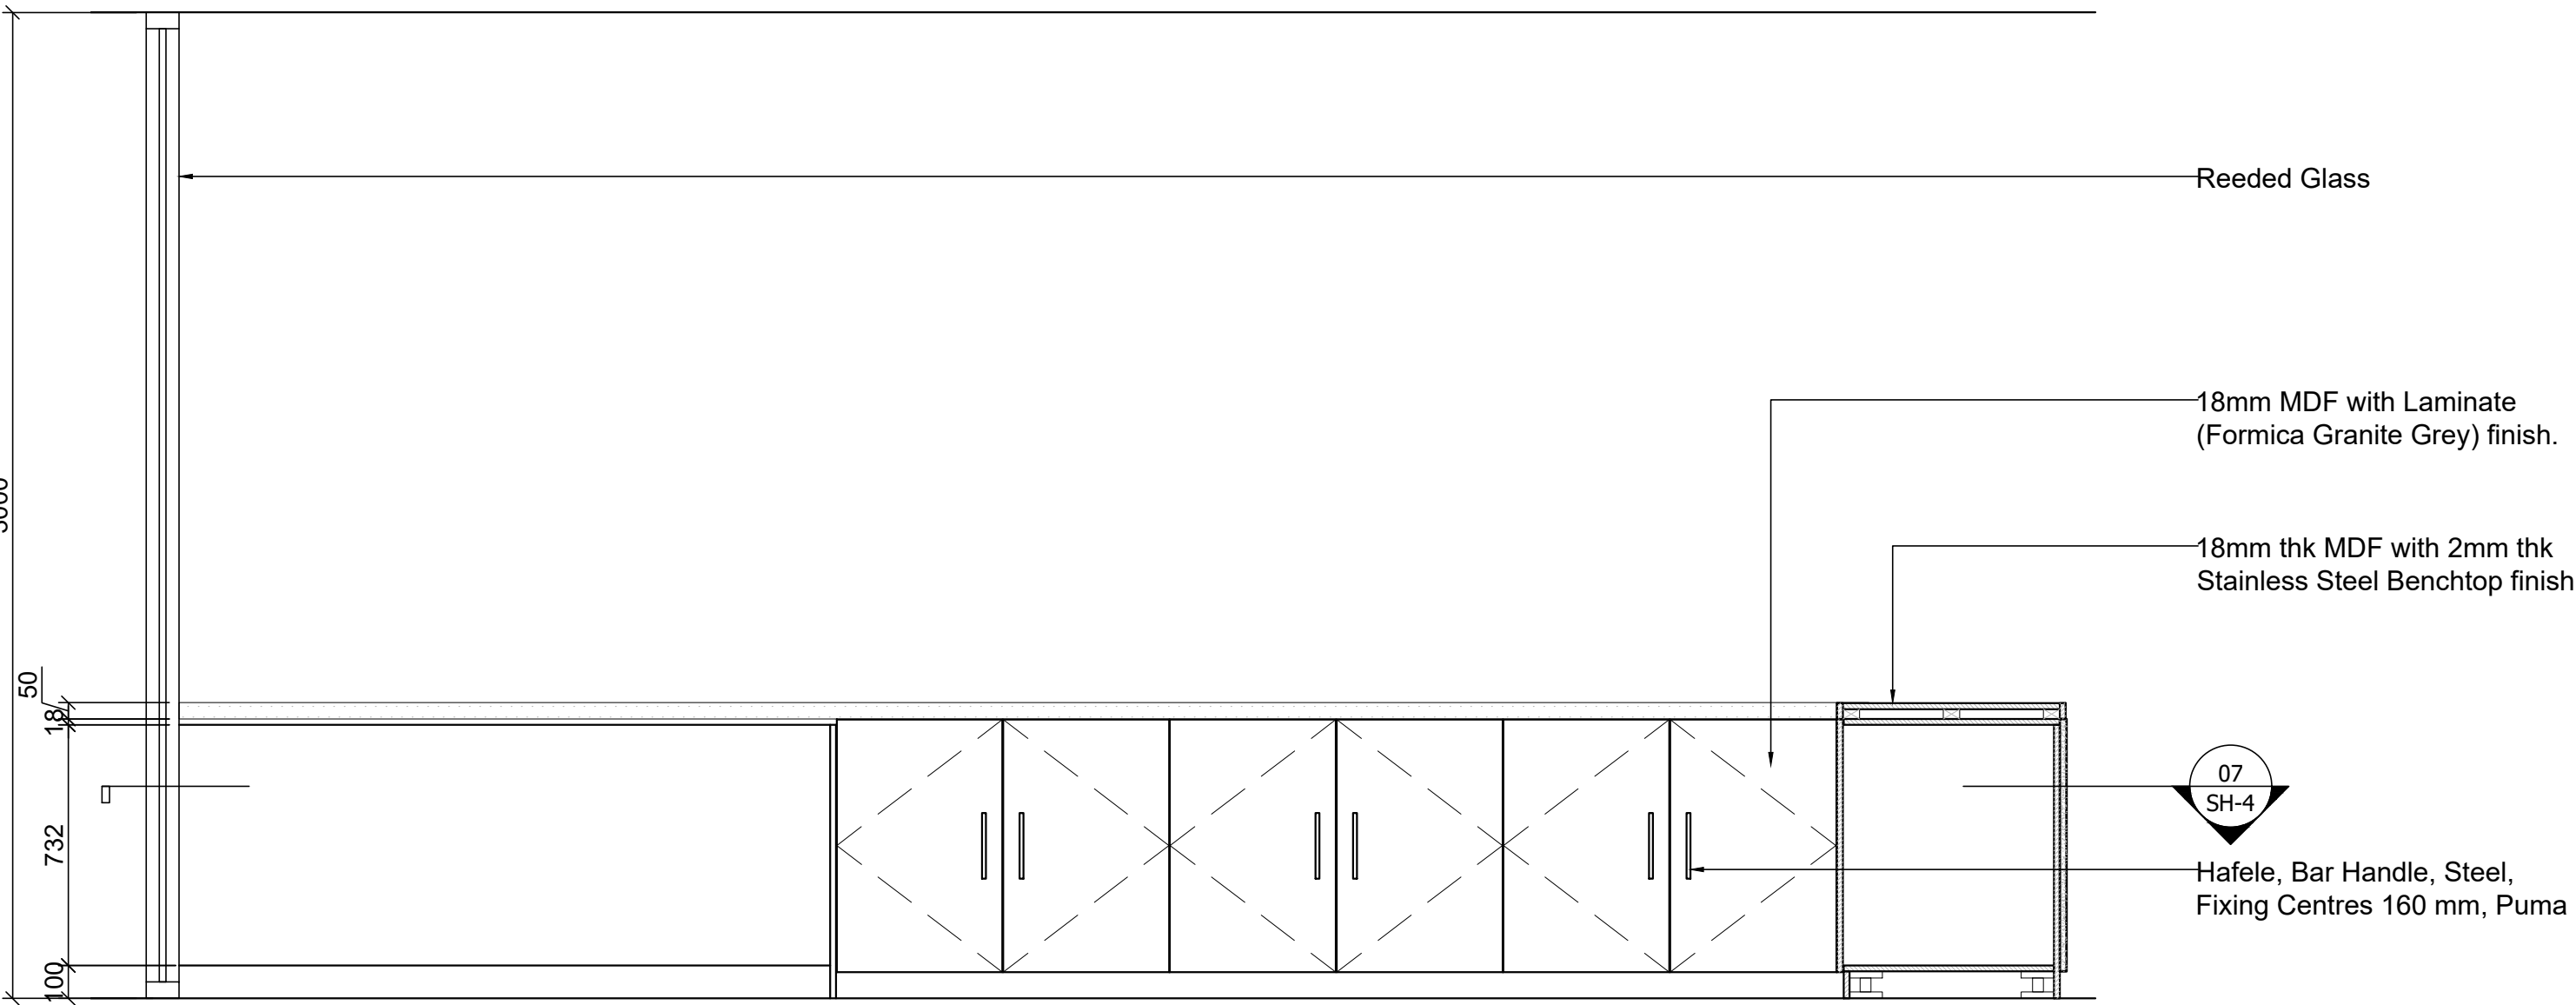


4 ELEVATION
Scale: 1:20

FOR APPROVAL




PROJECT:	STW2872
TITLE:	JXX - CAFE BAR
DETAILS:	ELEVATIONS
DATE:	04/30/2026
SHEET:	3 OF 5
DRAWN:	JPO
CHECK:	ACA
SCALE:	AS SHOWN @ A1
DRAWING N°:	STW2872- JXX- 03
REVISION:	00

REVISION HISTORY		
REV	DESCRIPTION	DATE
	FIRST ISSUE	04/30/2026

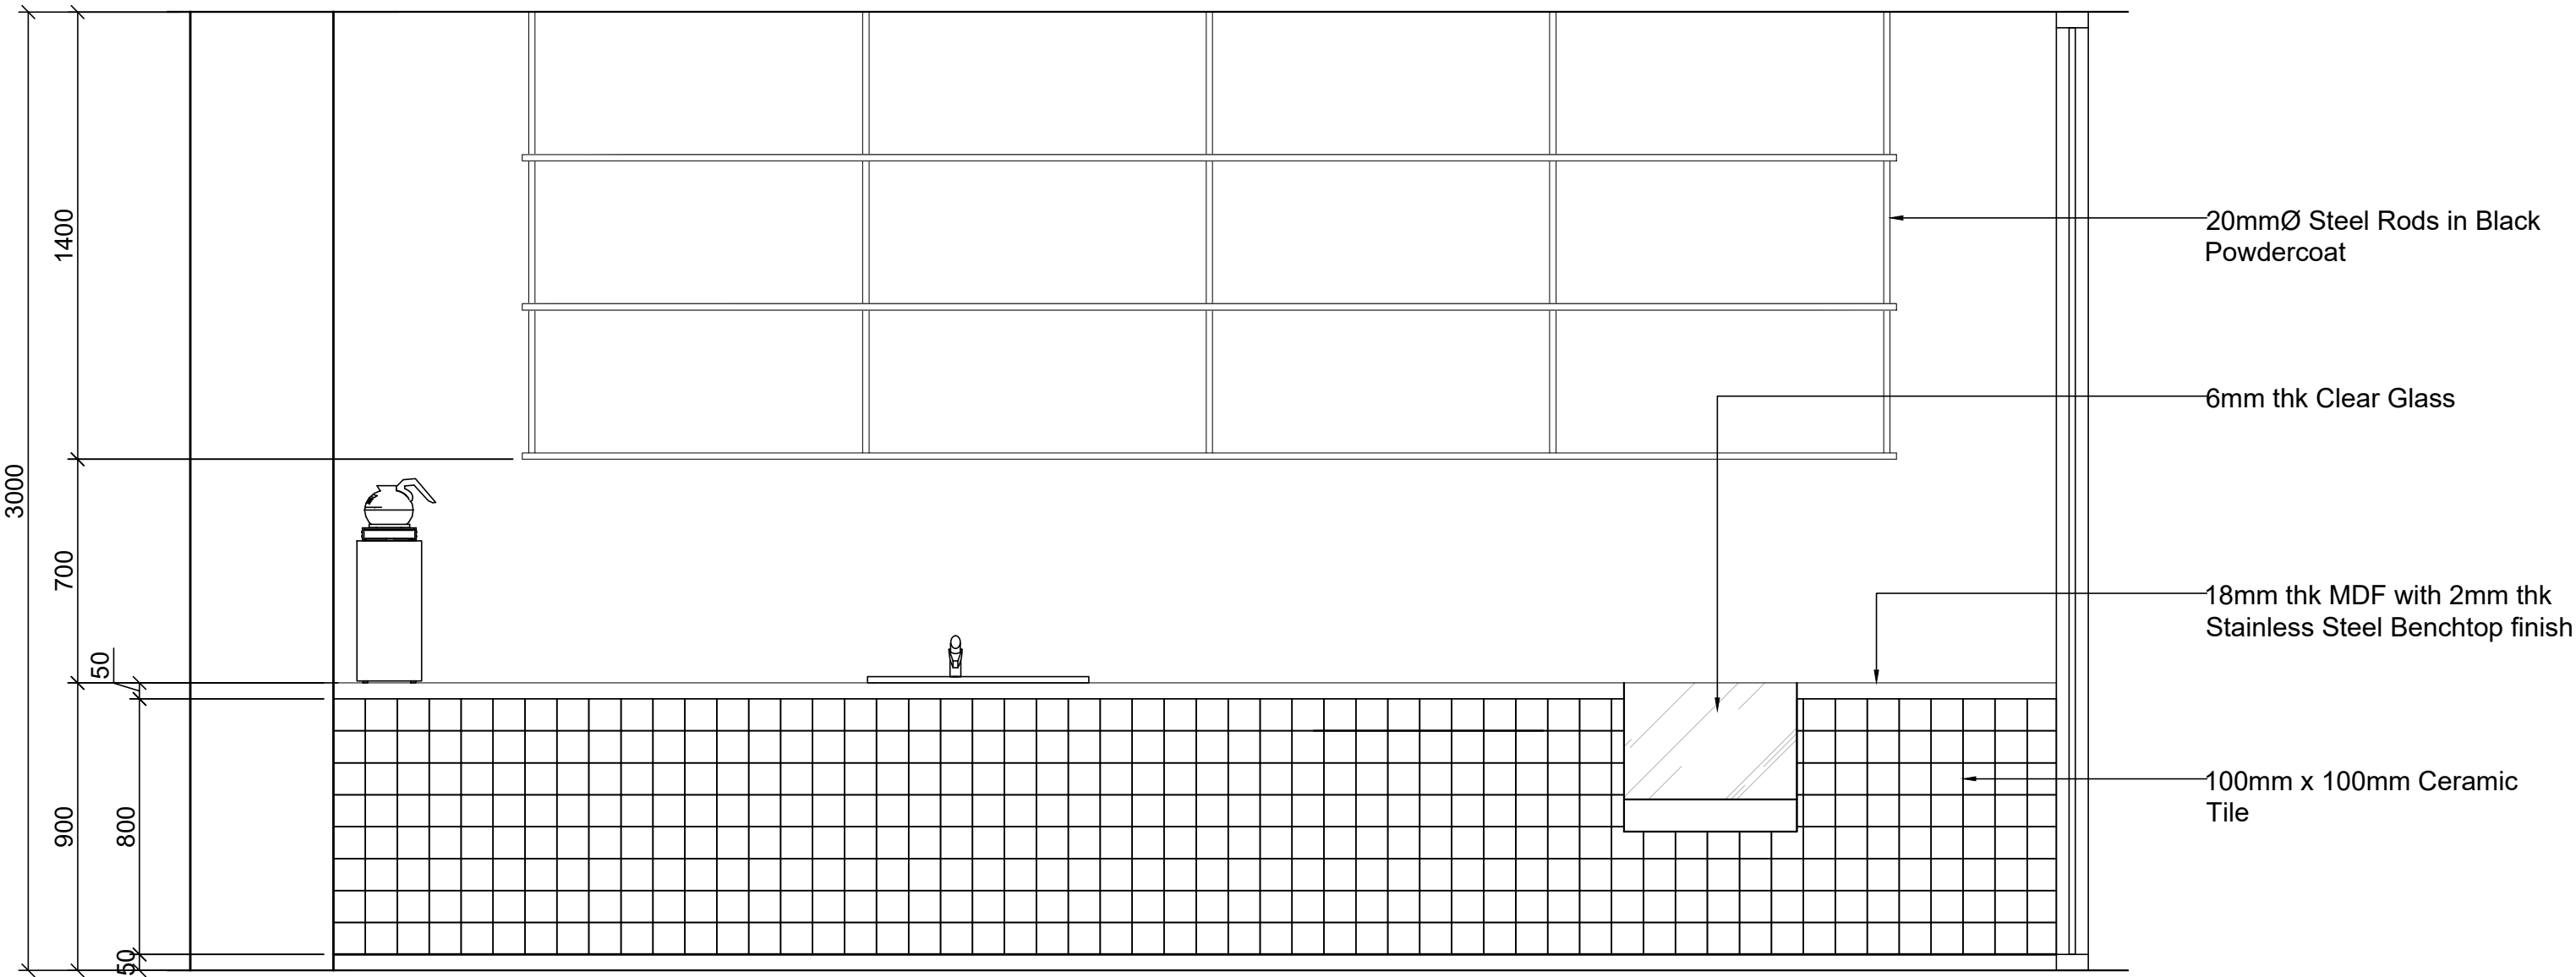


5 ELEVATION

Scale: 1:20

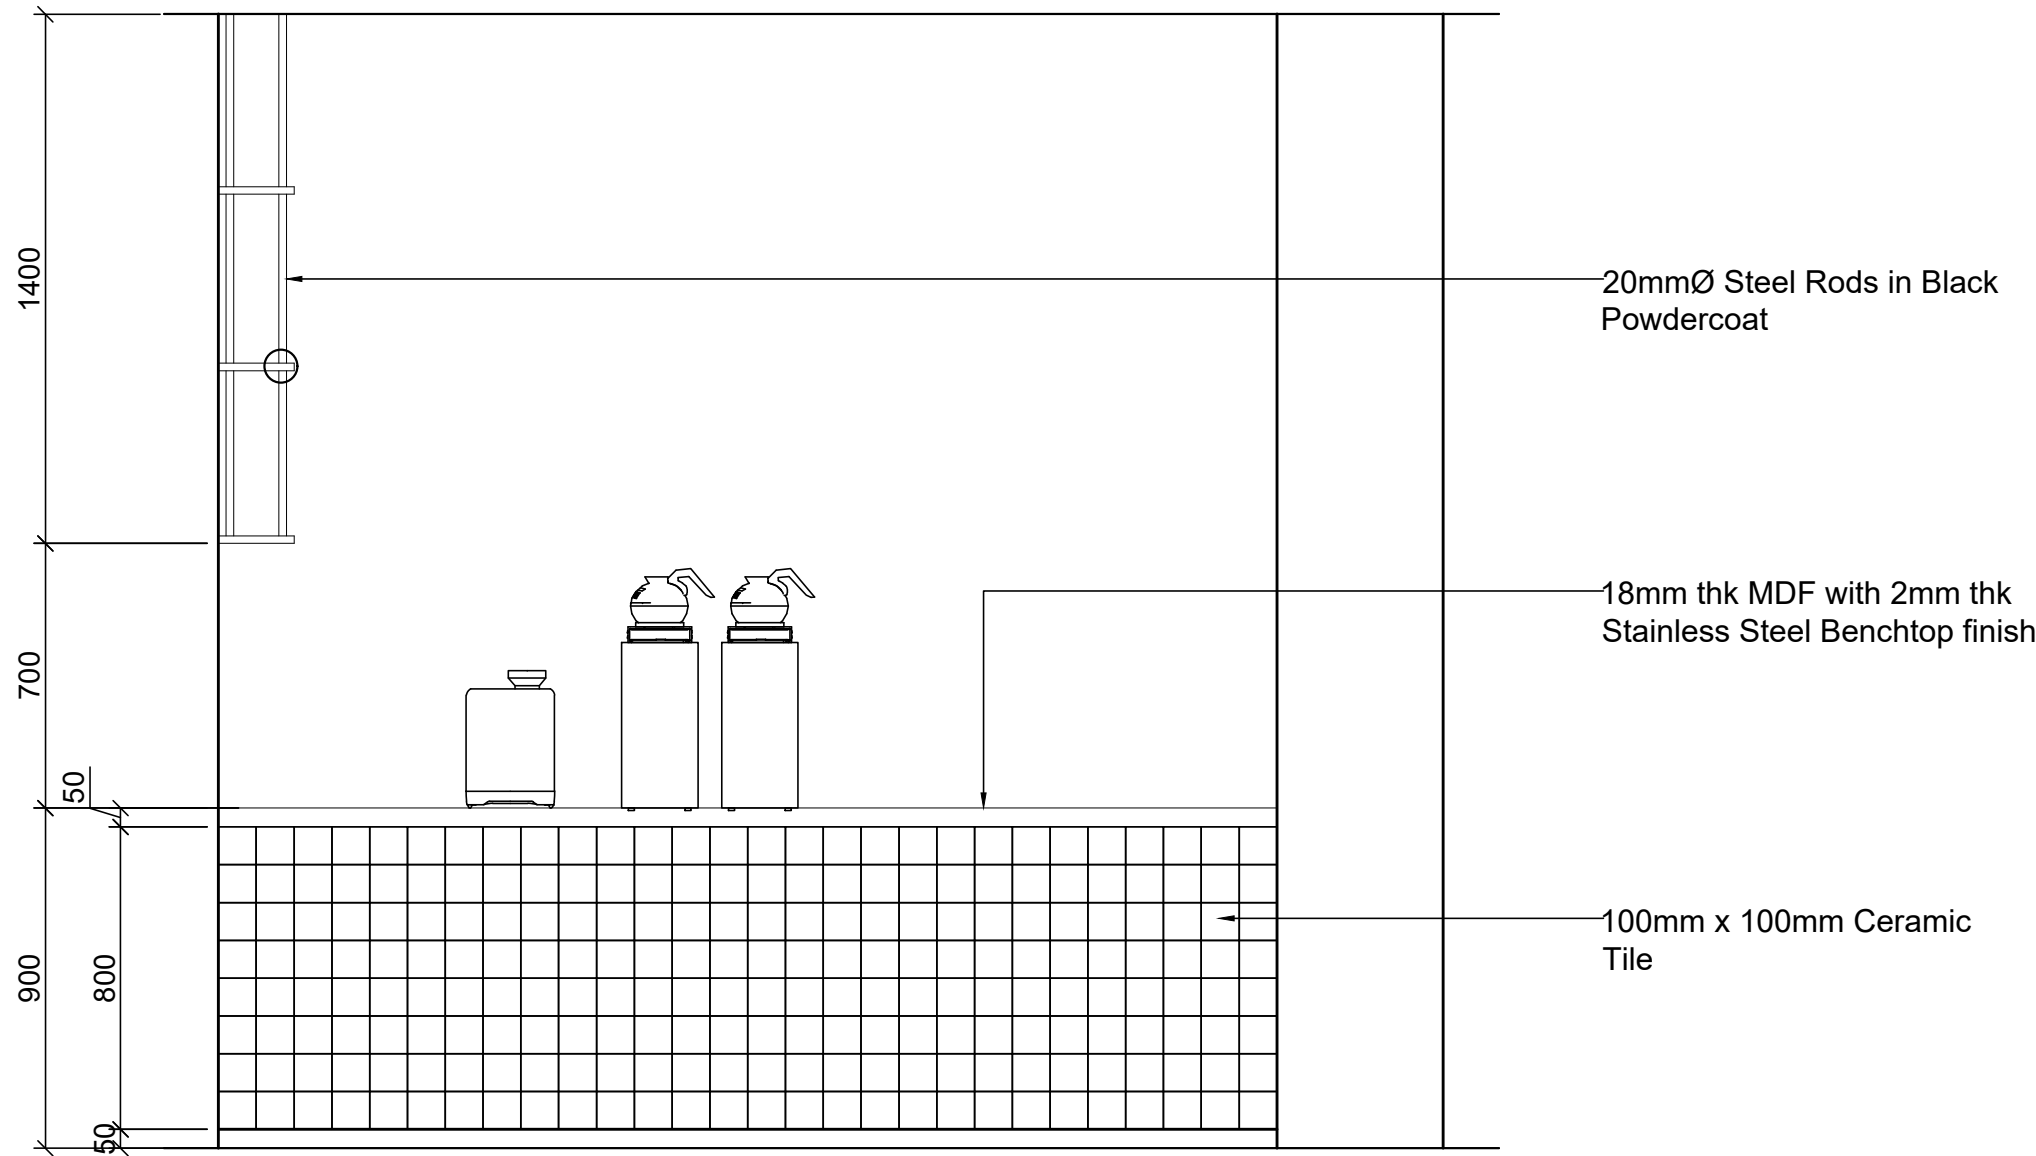


6 ELEVATION

Scale: 1:20

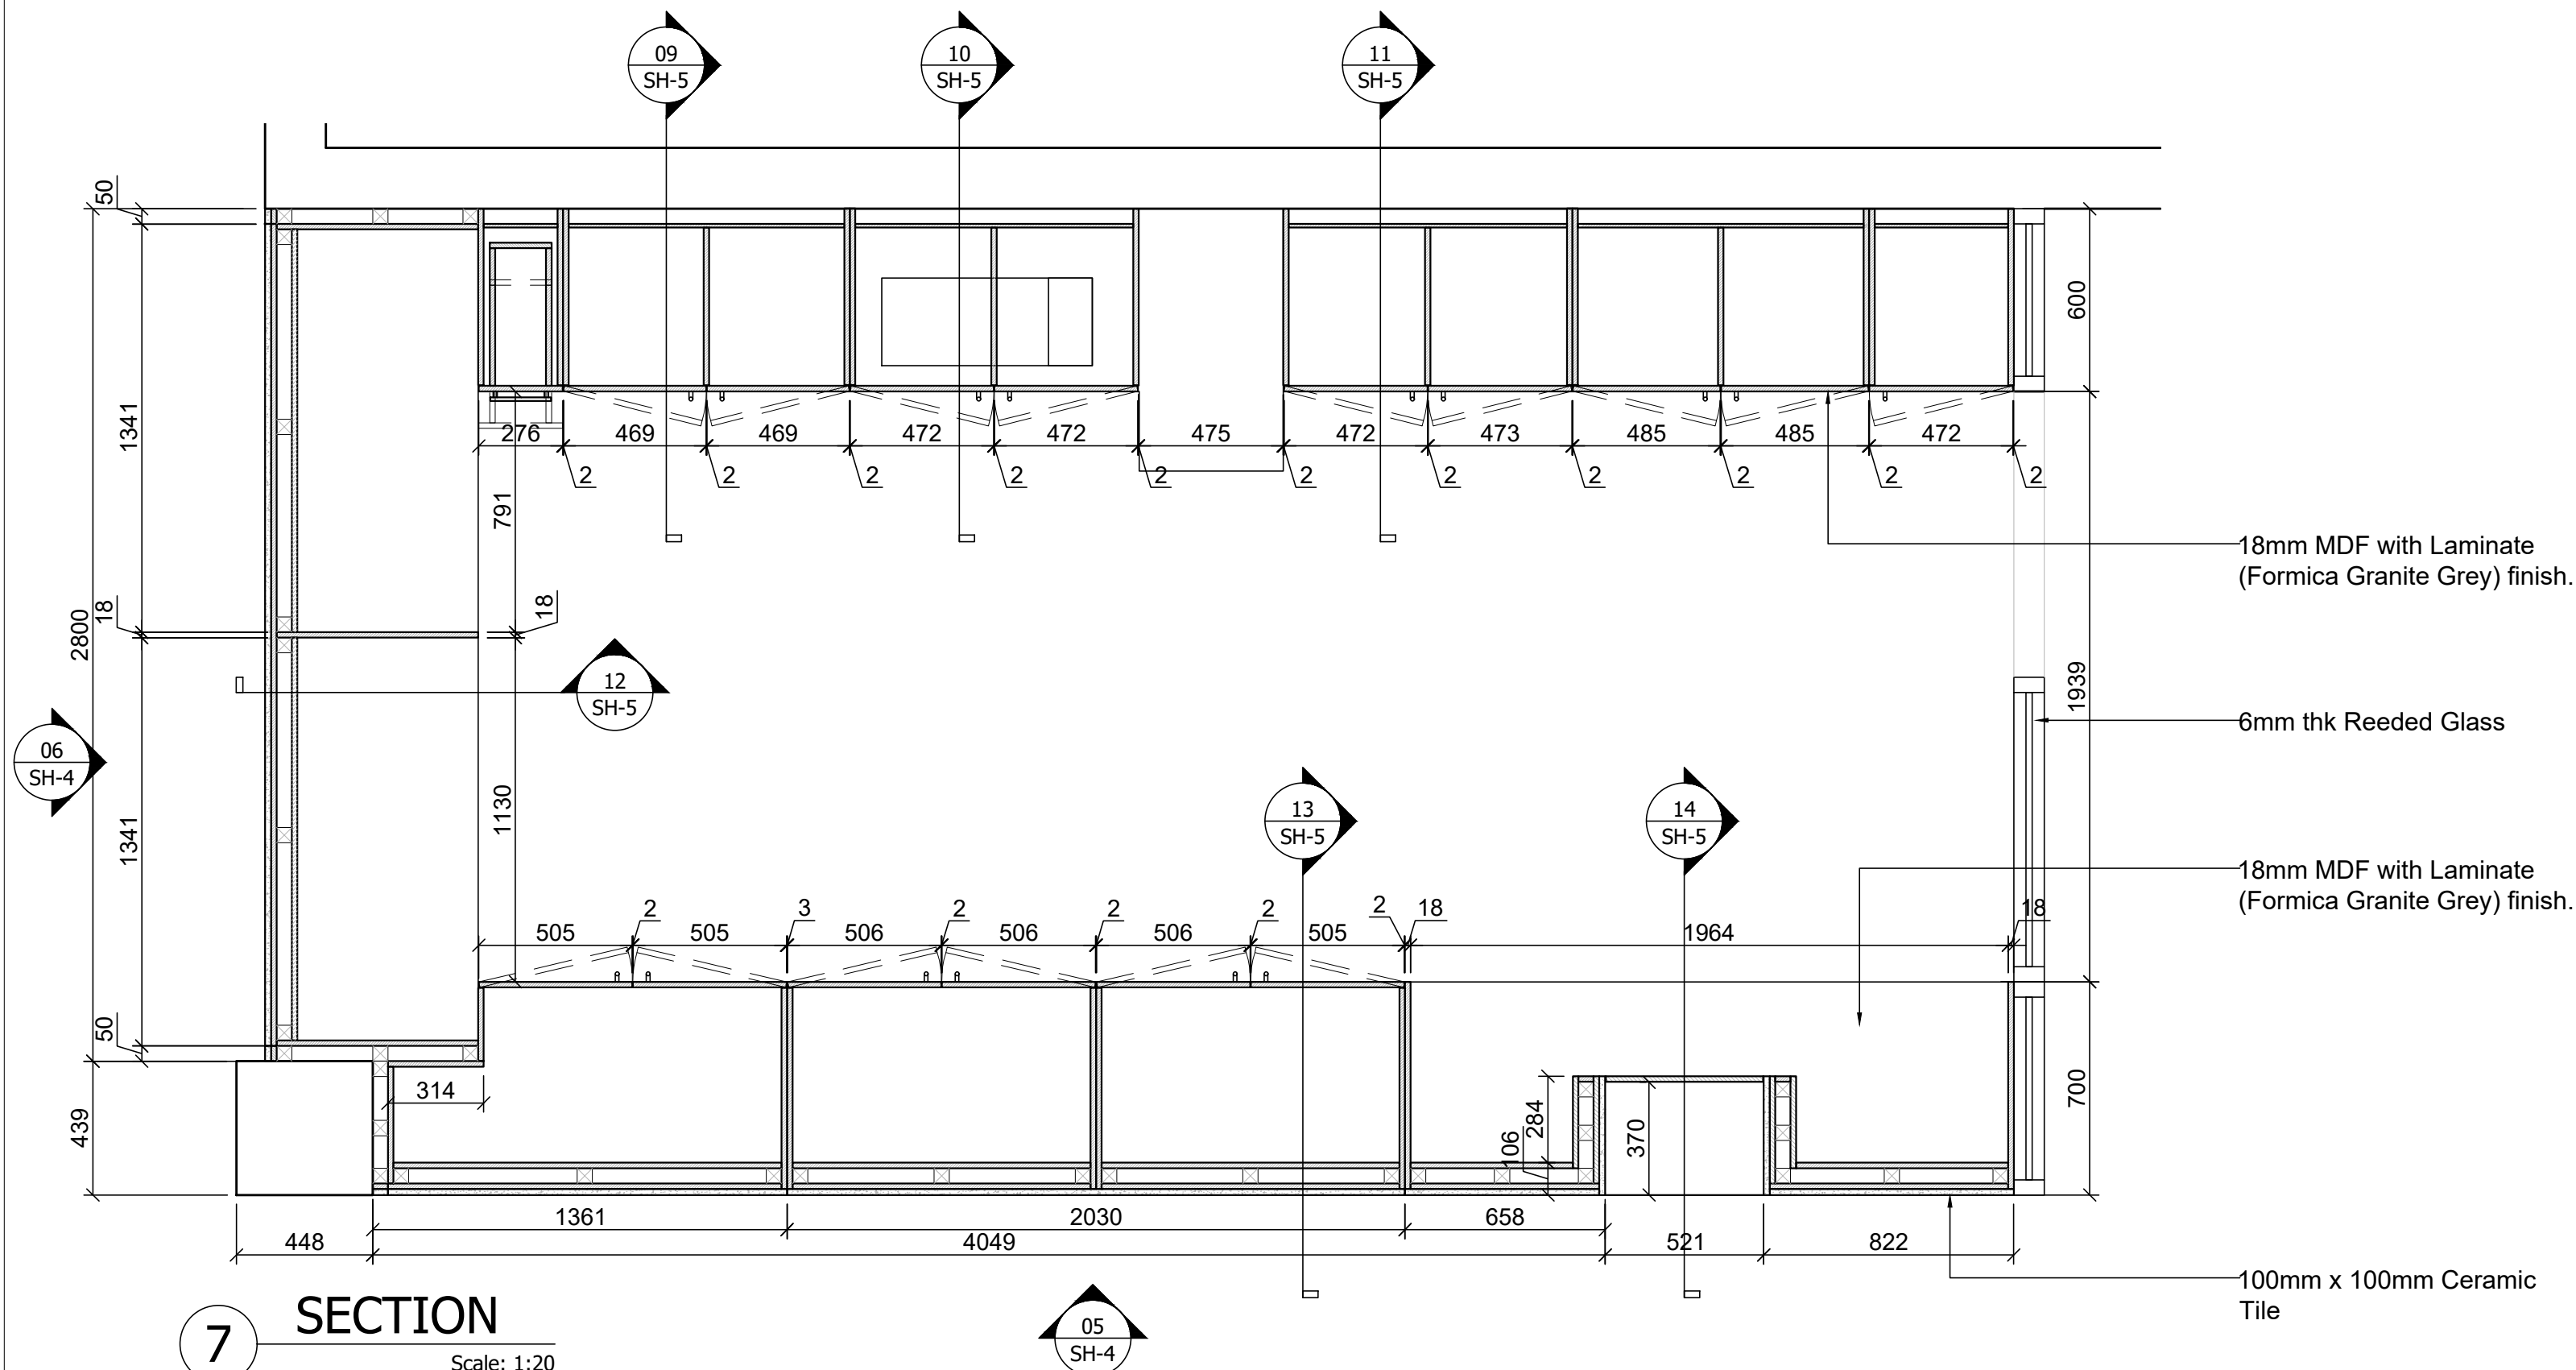

7 SECTION

Scale: 1:20

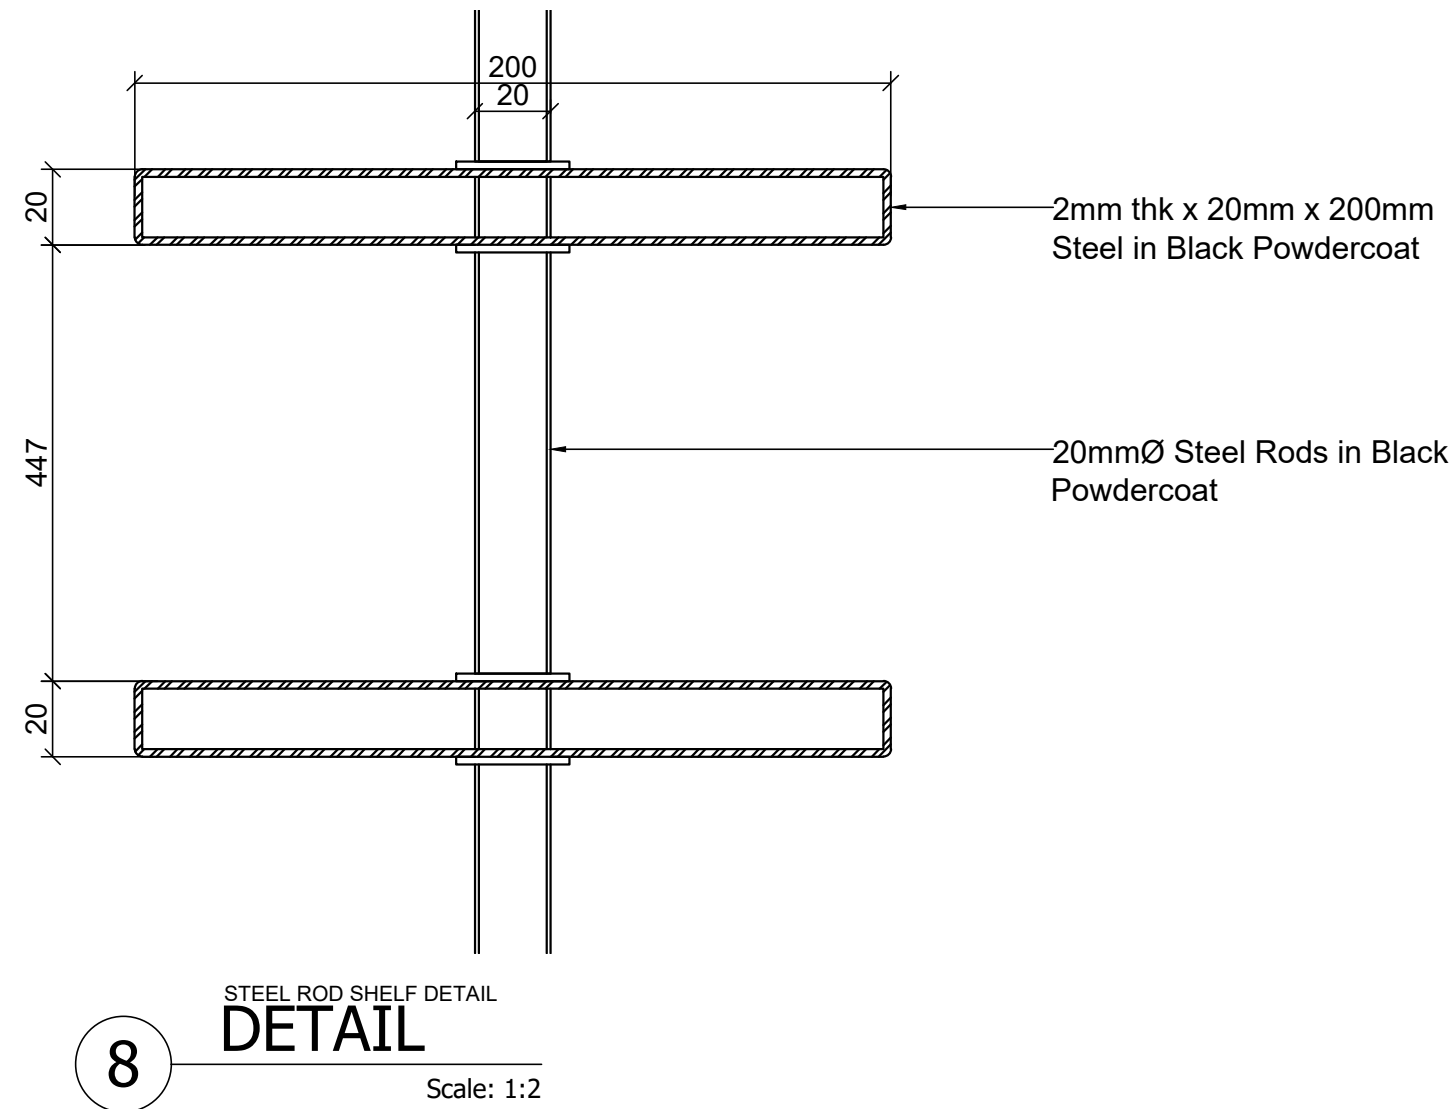

FOR APPROVAL



PROJECT: STW2872

TITLE: JXX - CAFE BAR

DETAILS: ELEVATIONS & SECTIONS

DATE: 04/30/2026

SHEET: 4 OF 5

DRAWN: JPO

CHECK: ACA


SCALE: AS SHOWN @ A1

DRAWING N°: REVISION:


STW2872- JXX- 04

00


REVISION HISTORY		
REV	DESCRIPTION	DATE
	FIRST ISSUE	04/30/2026

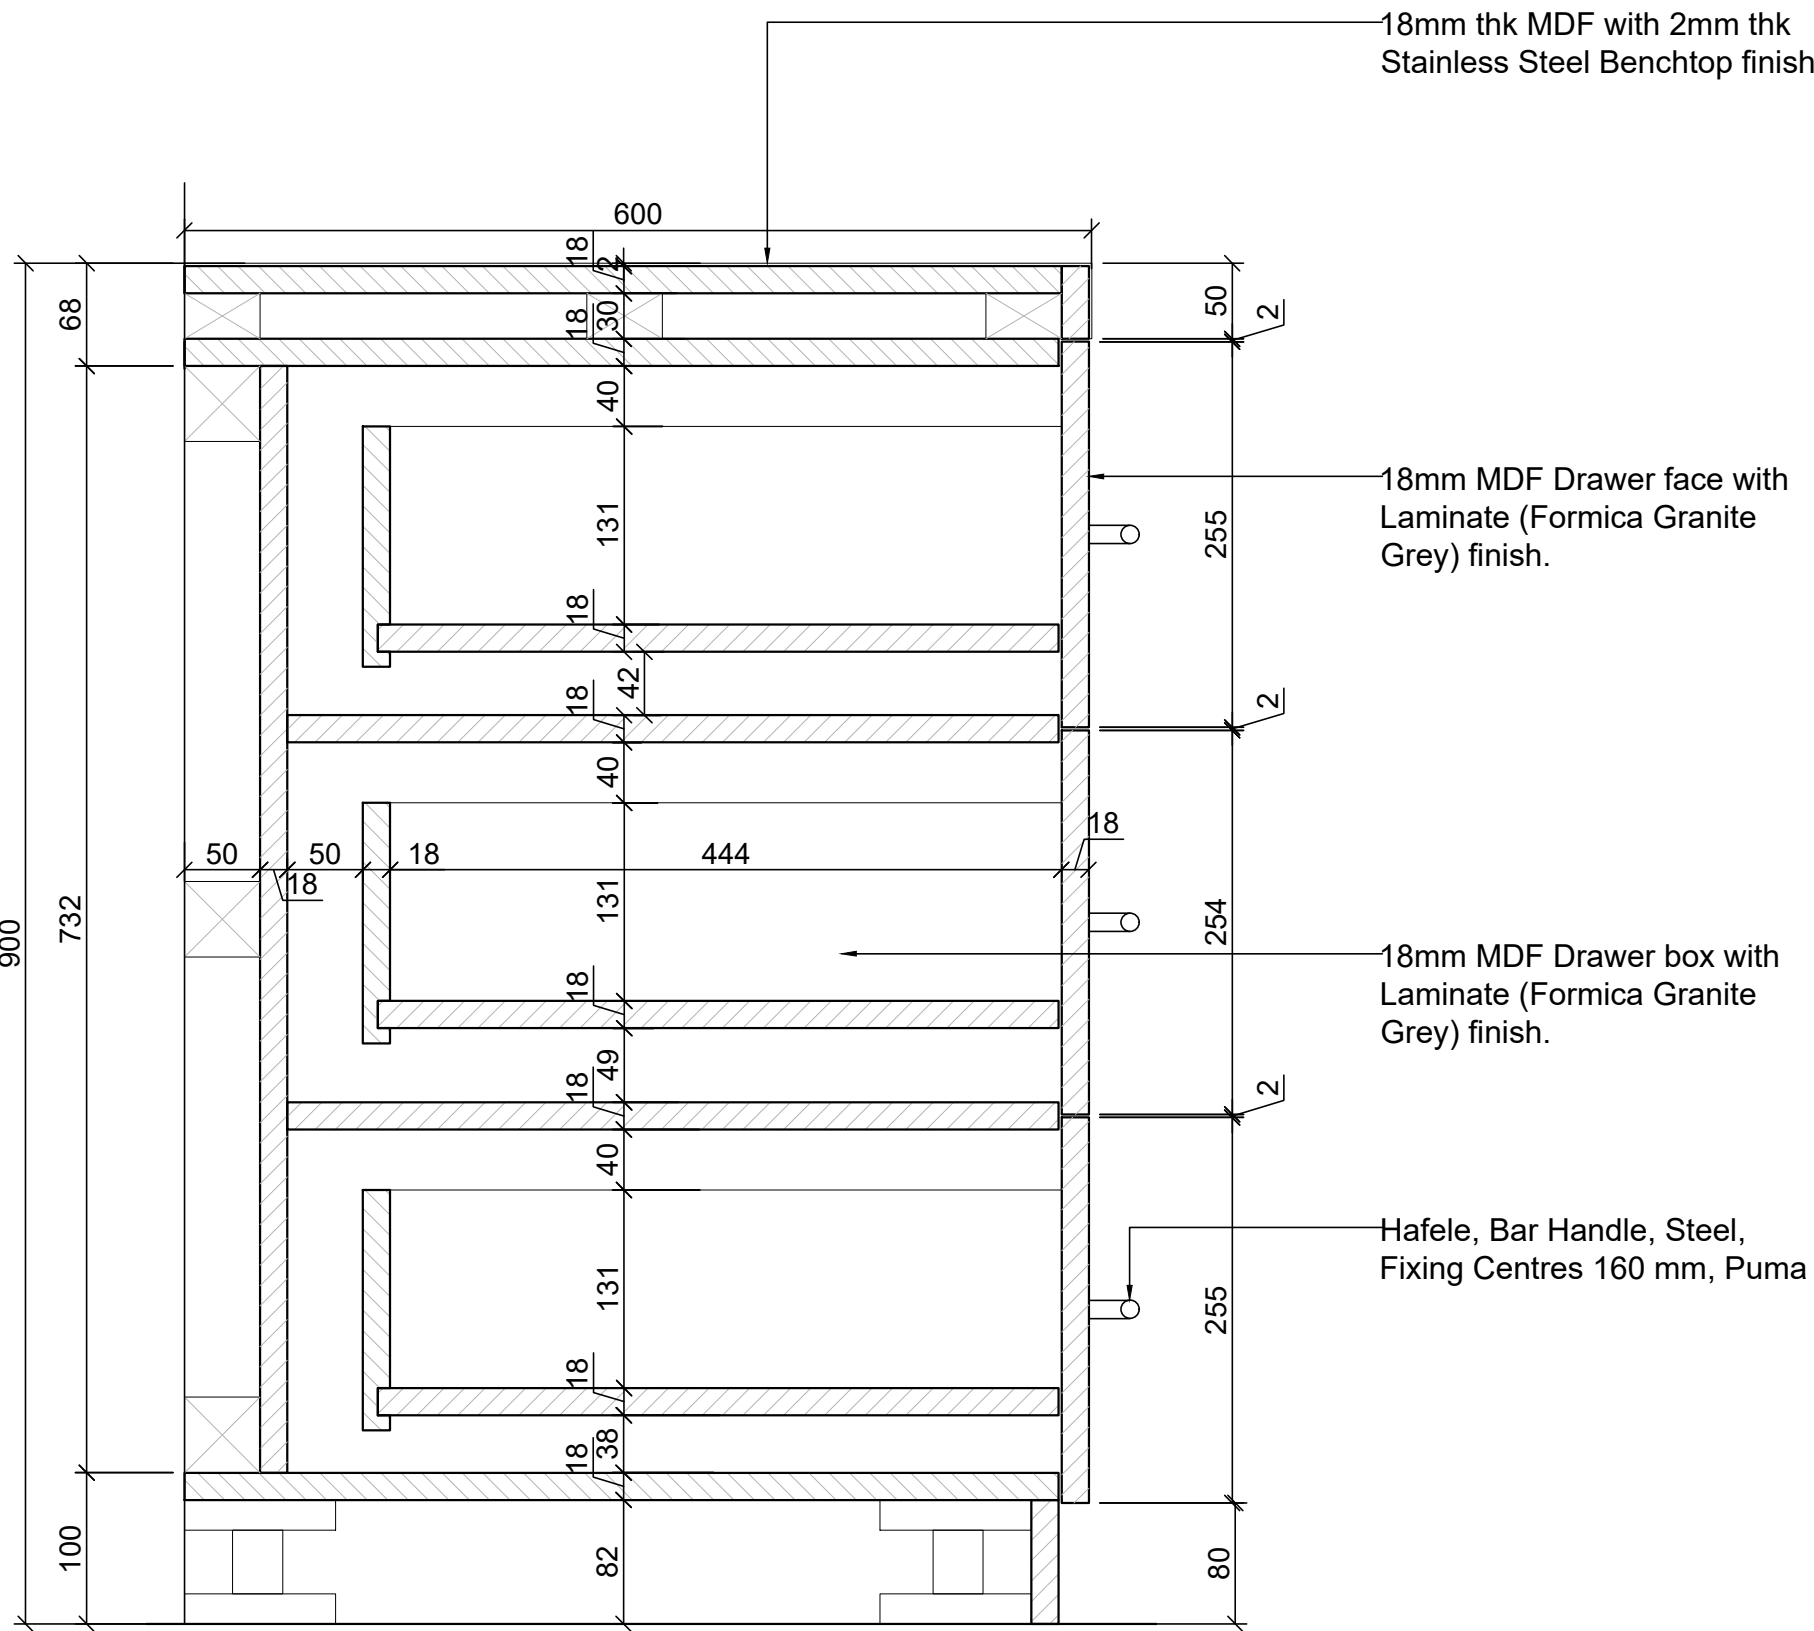


09 DETAIL
Scale: 1:5

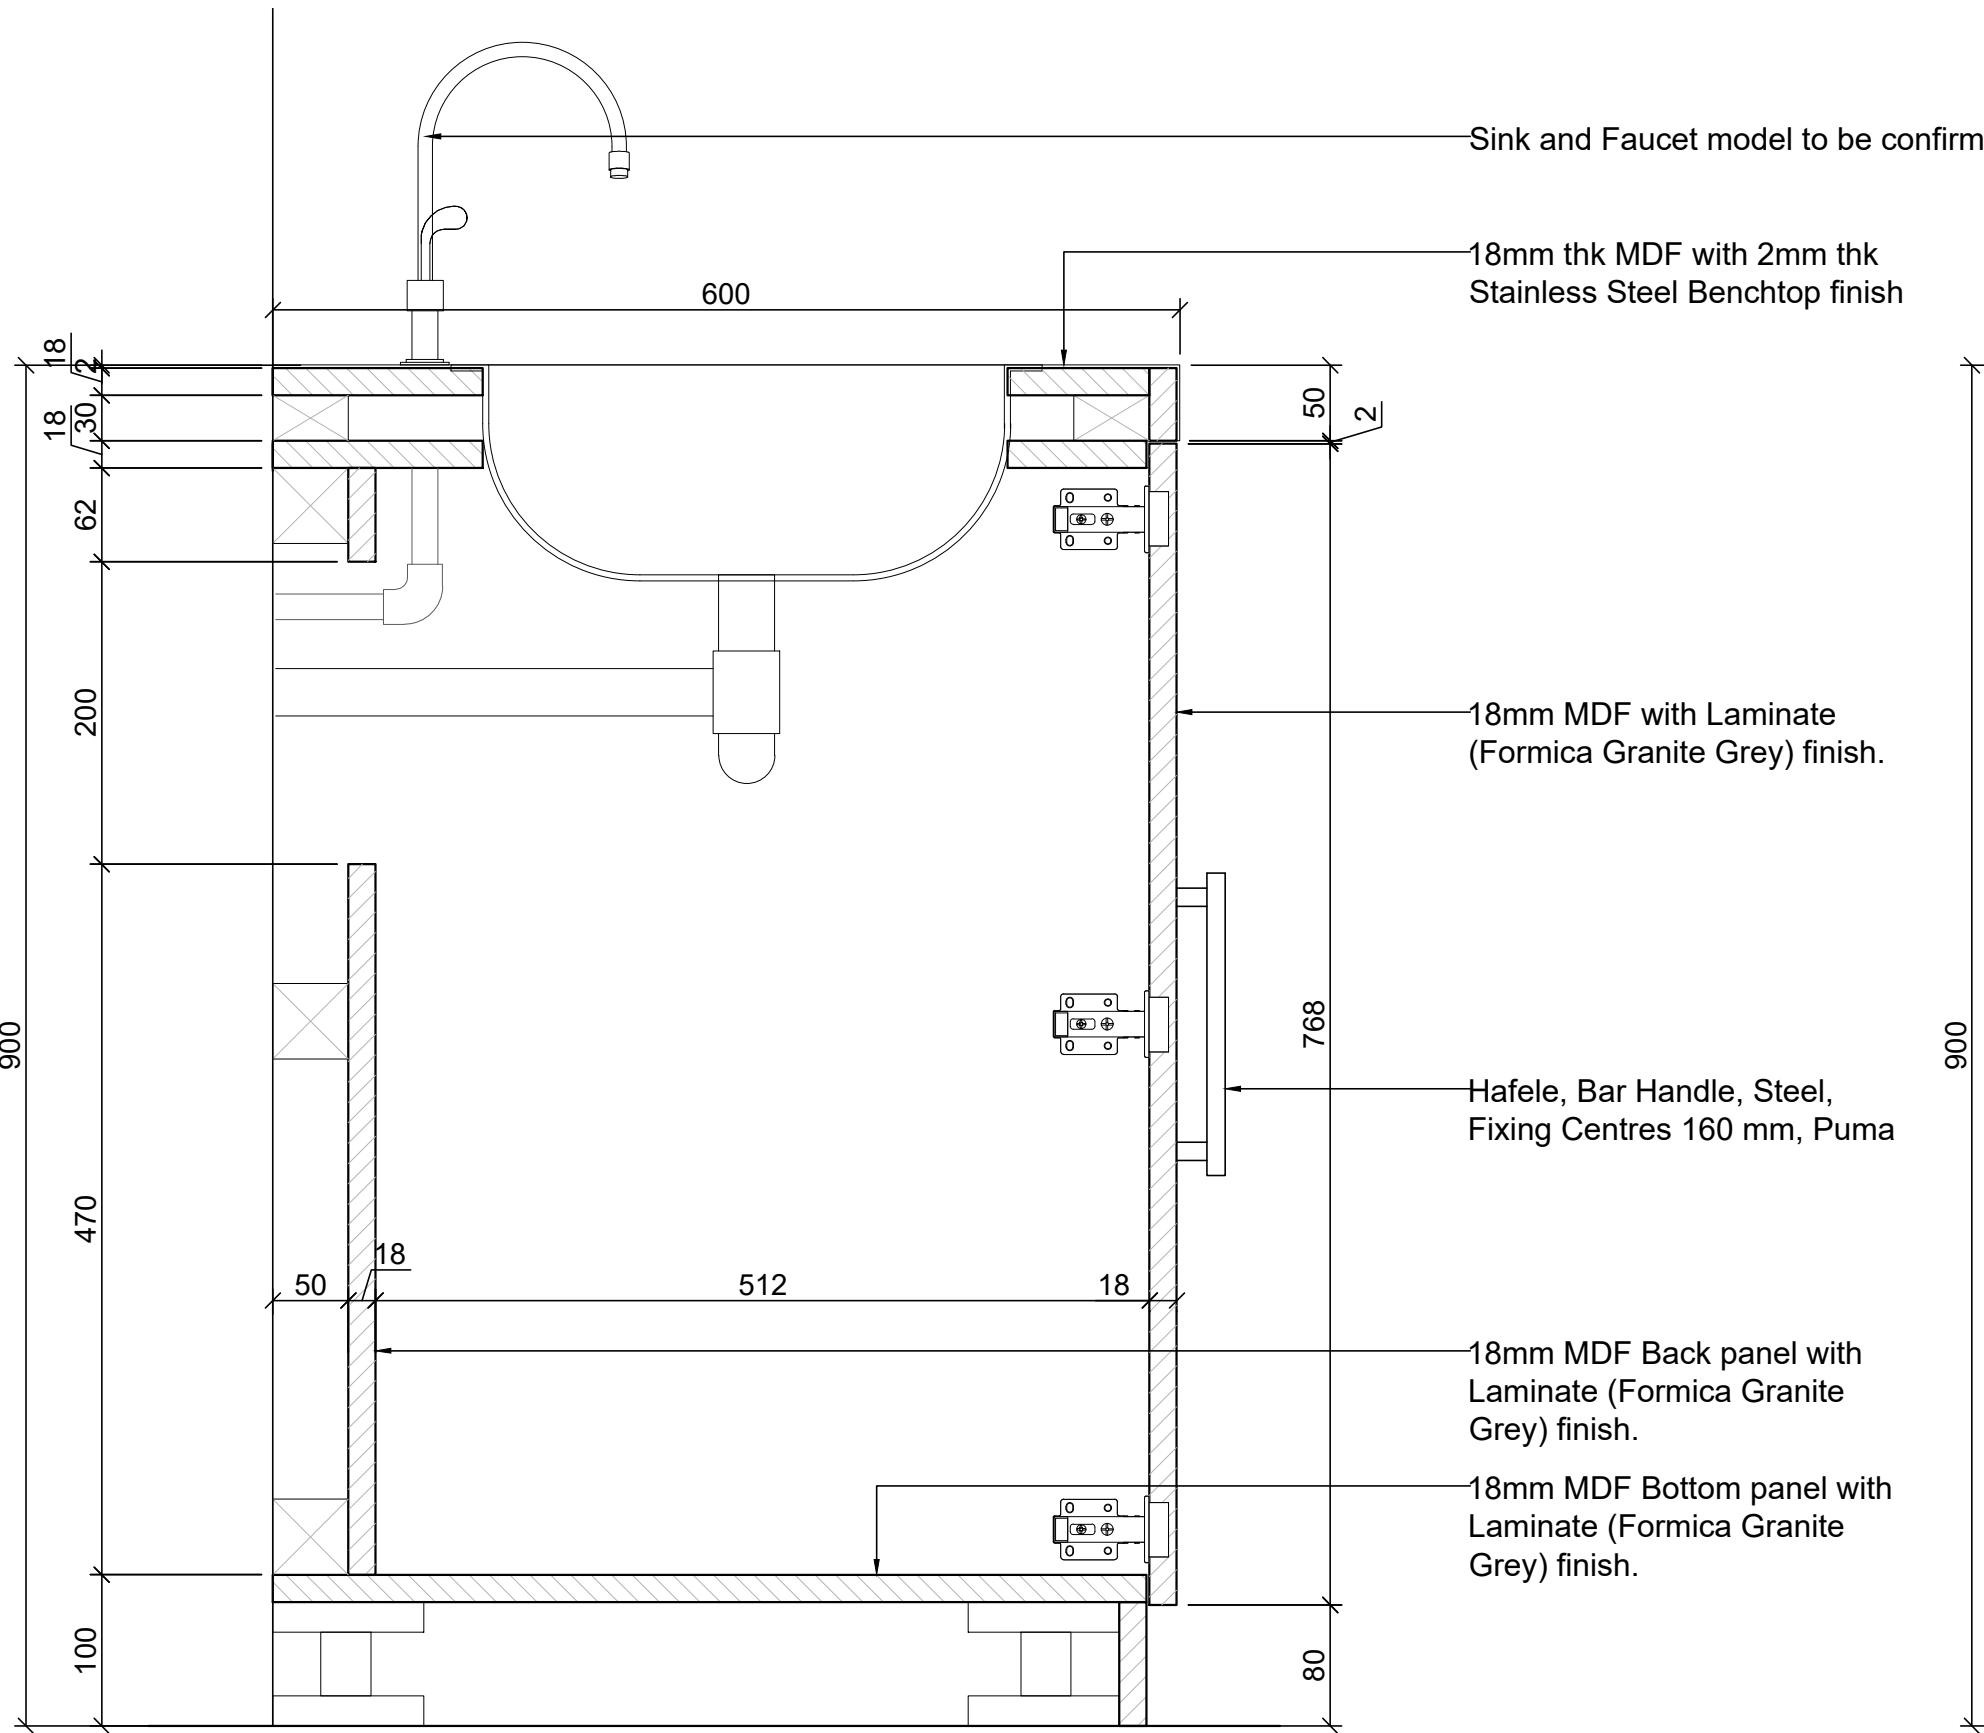


10 DETAIL
Scale: 1:5

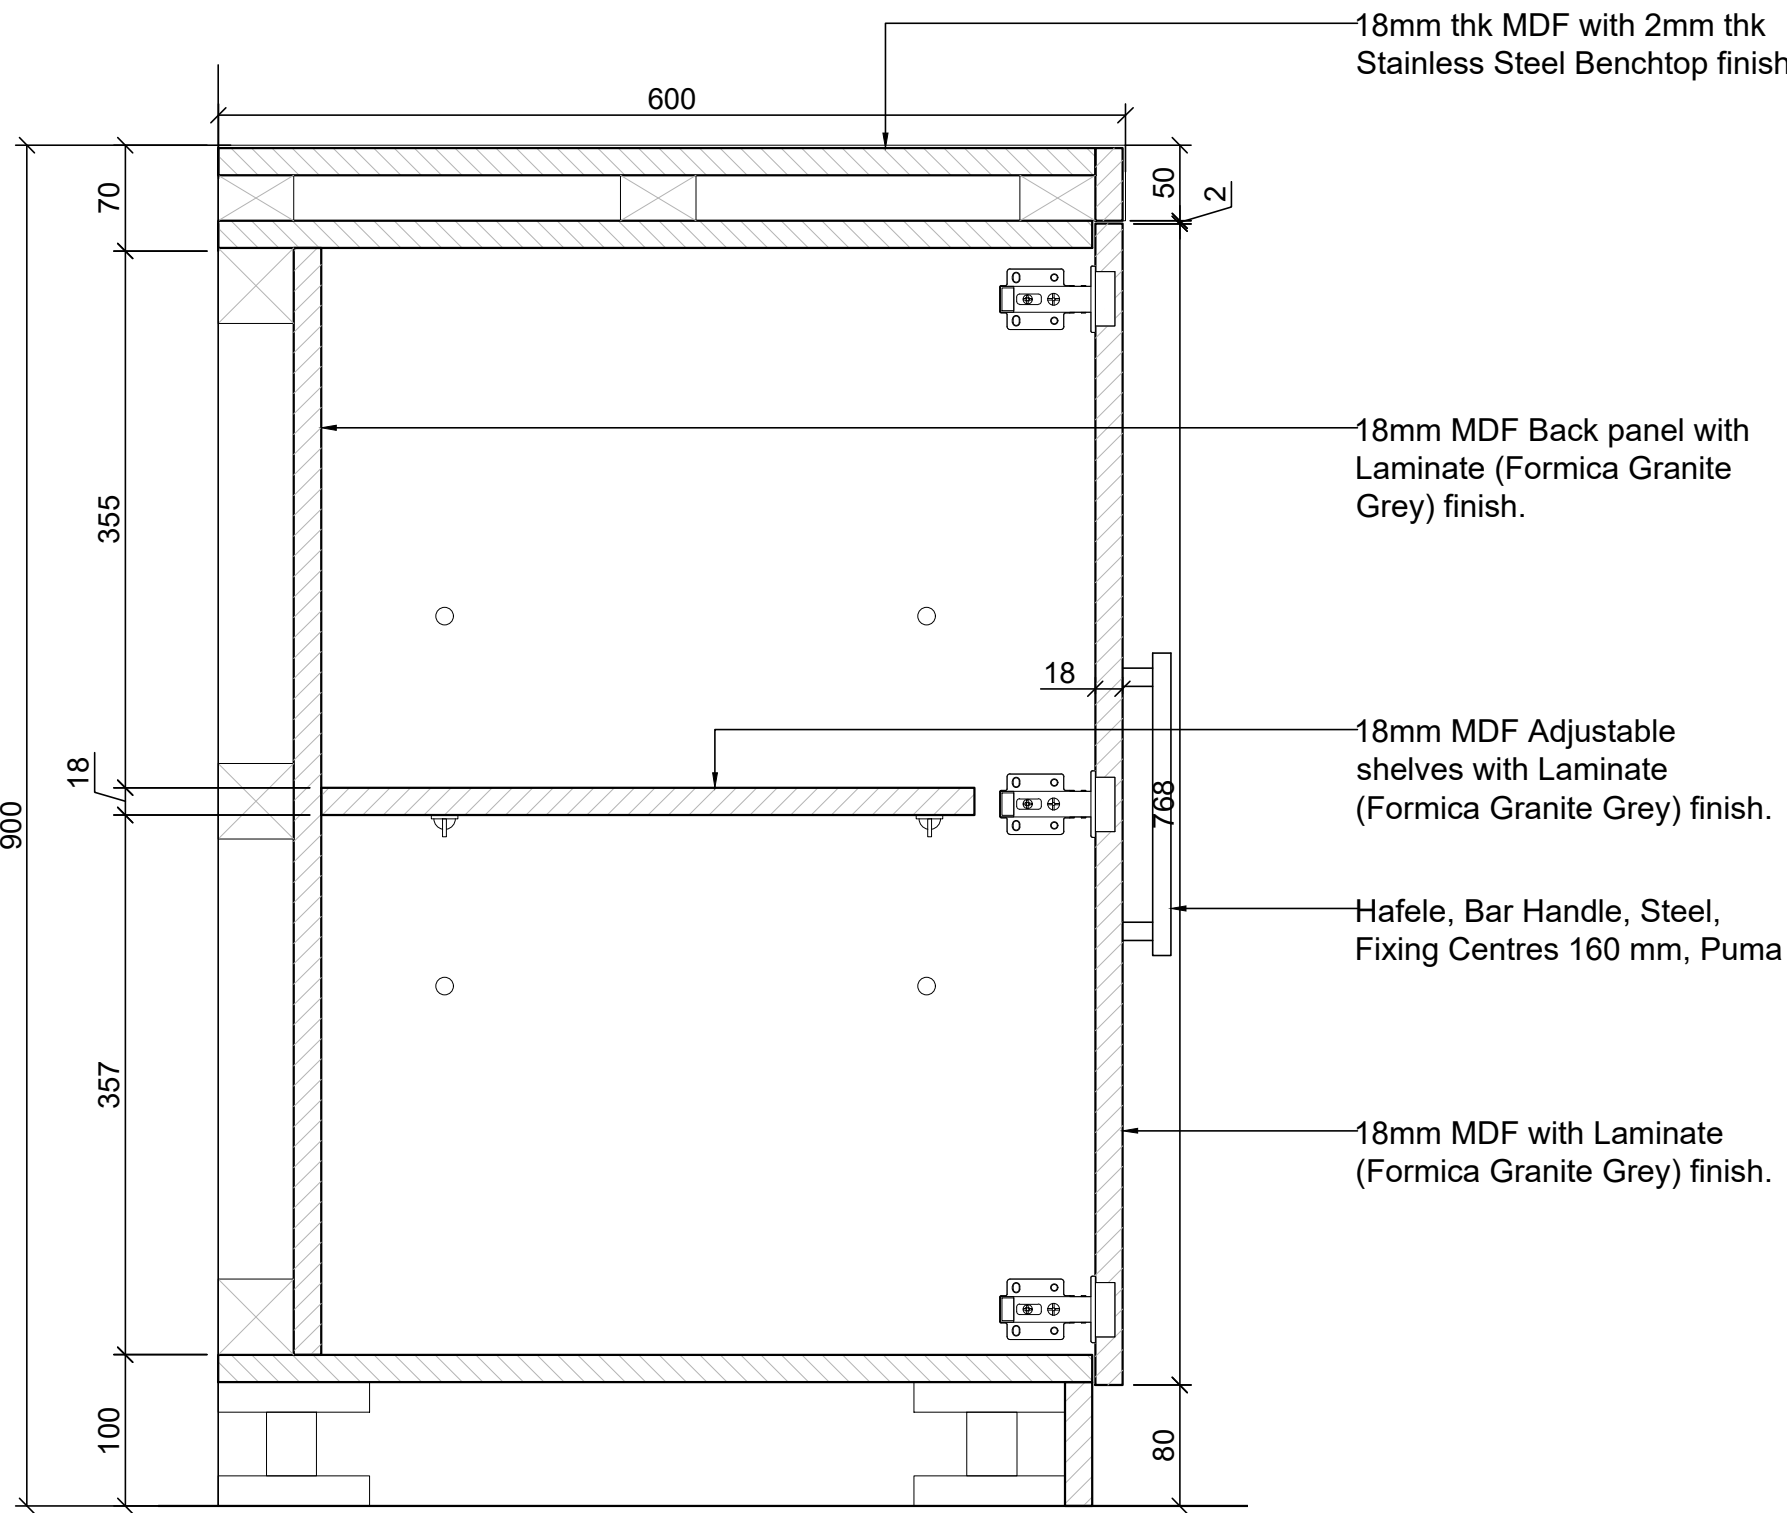


11 DETAIL
Scale: 1:5

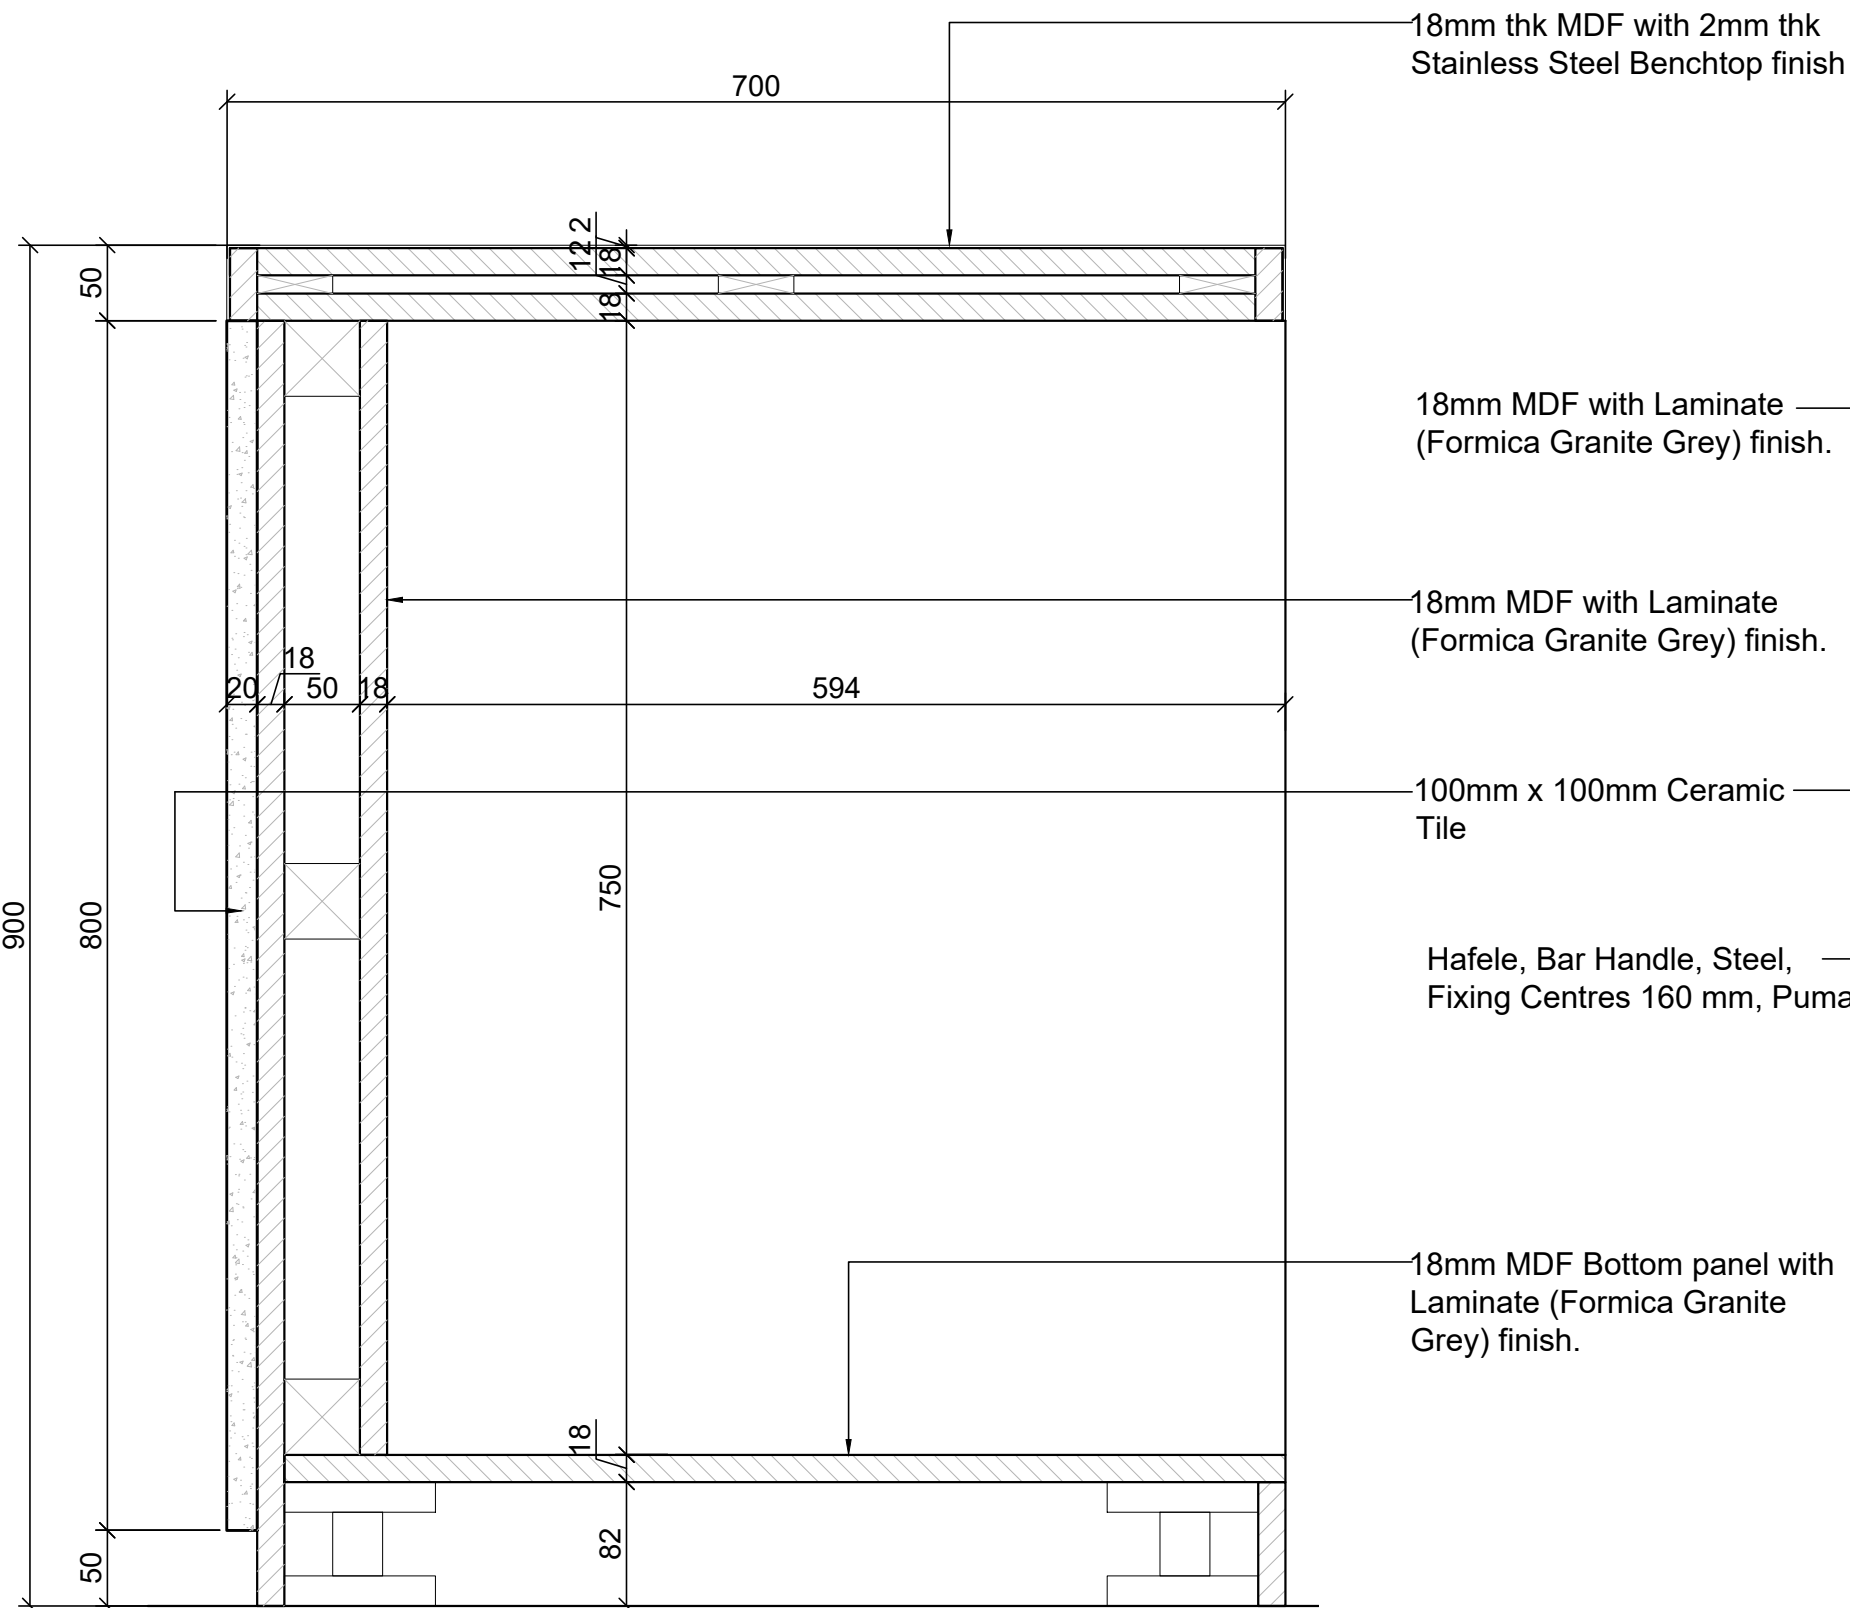

12 DETAIL
Scale: 1:5

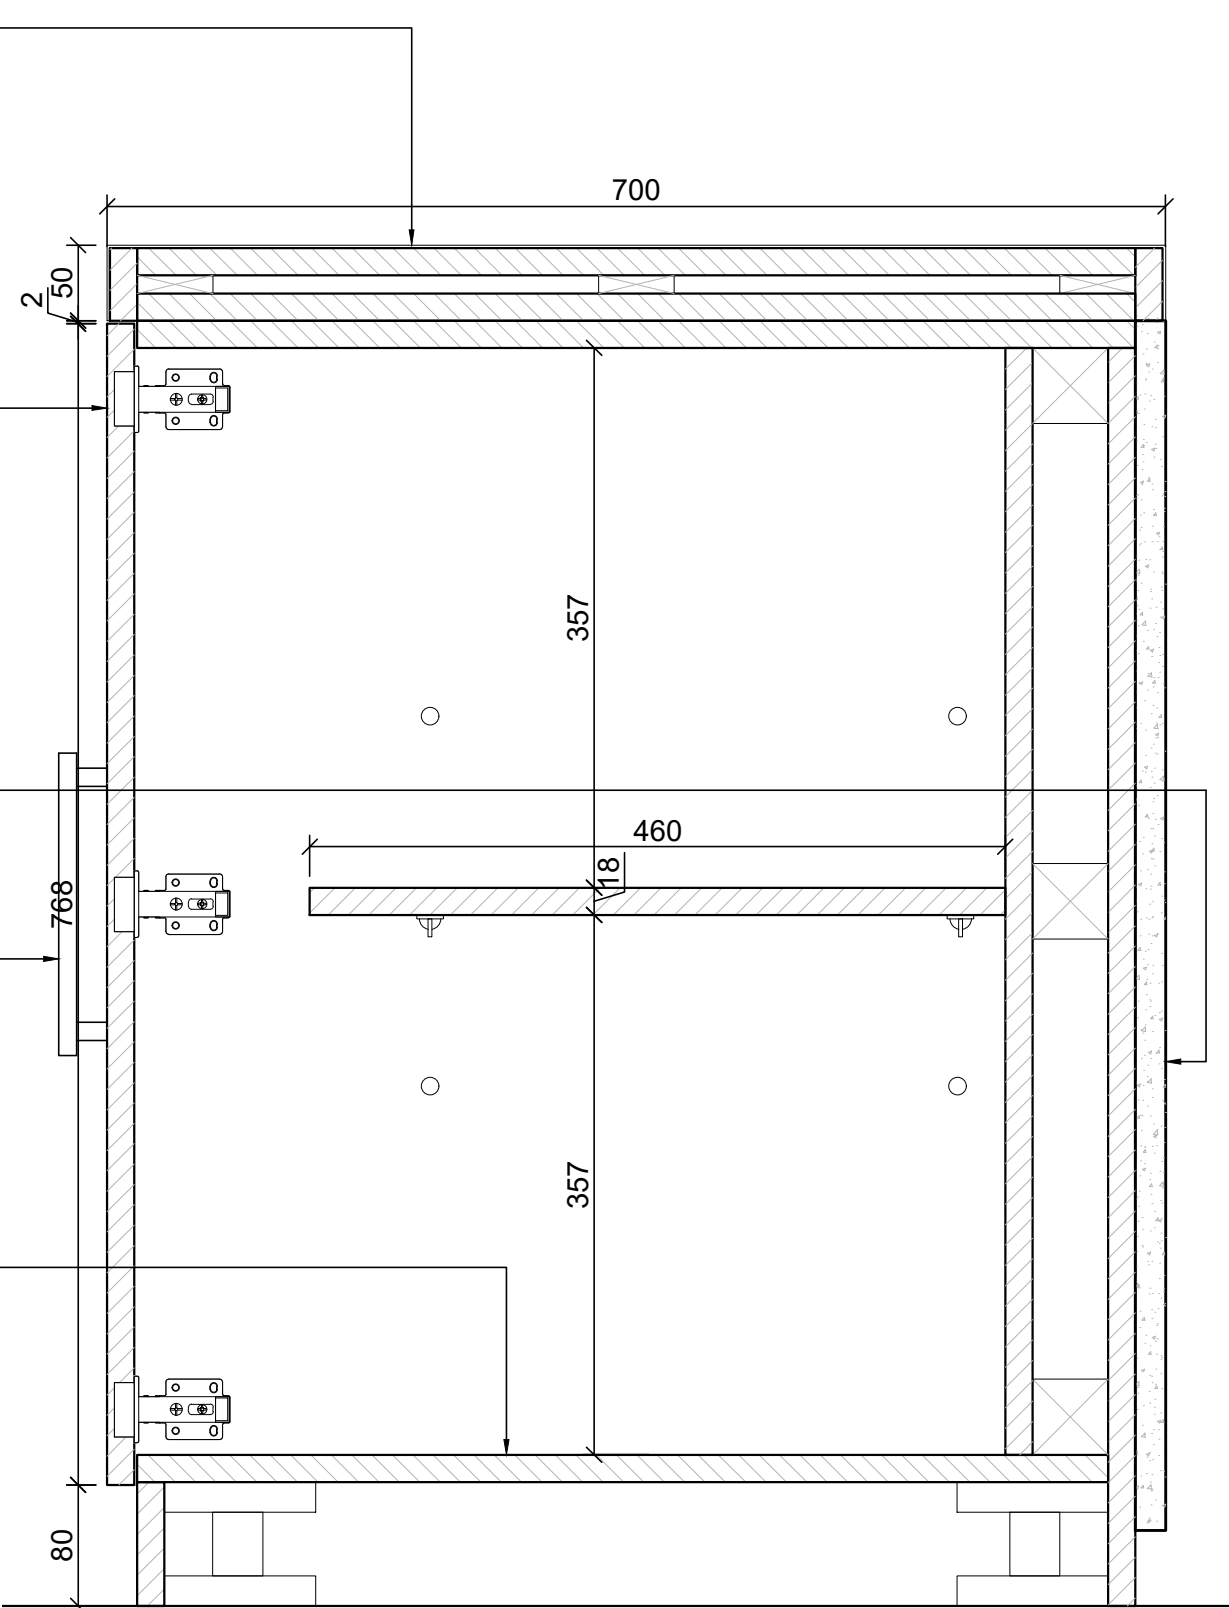

13 DETAIL
Scale: 1:5

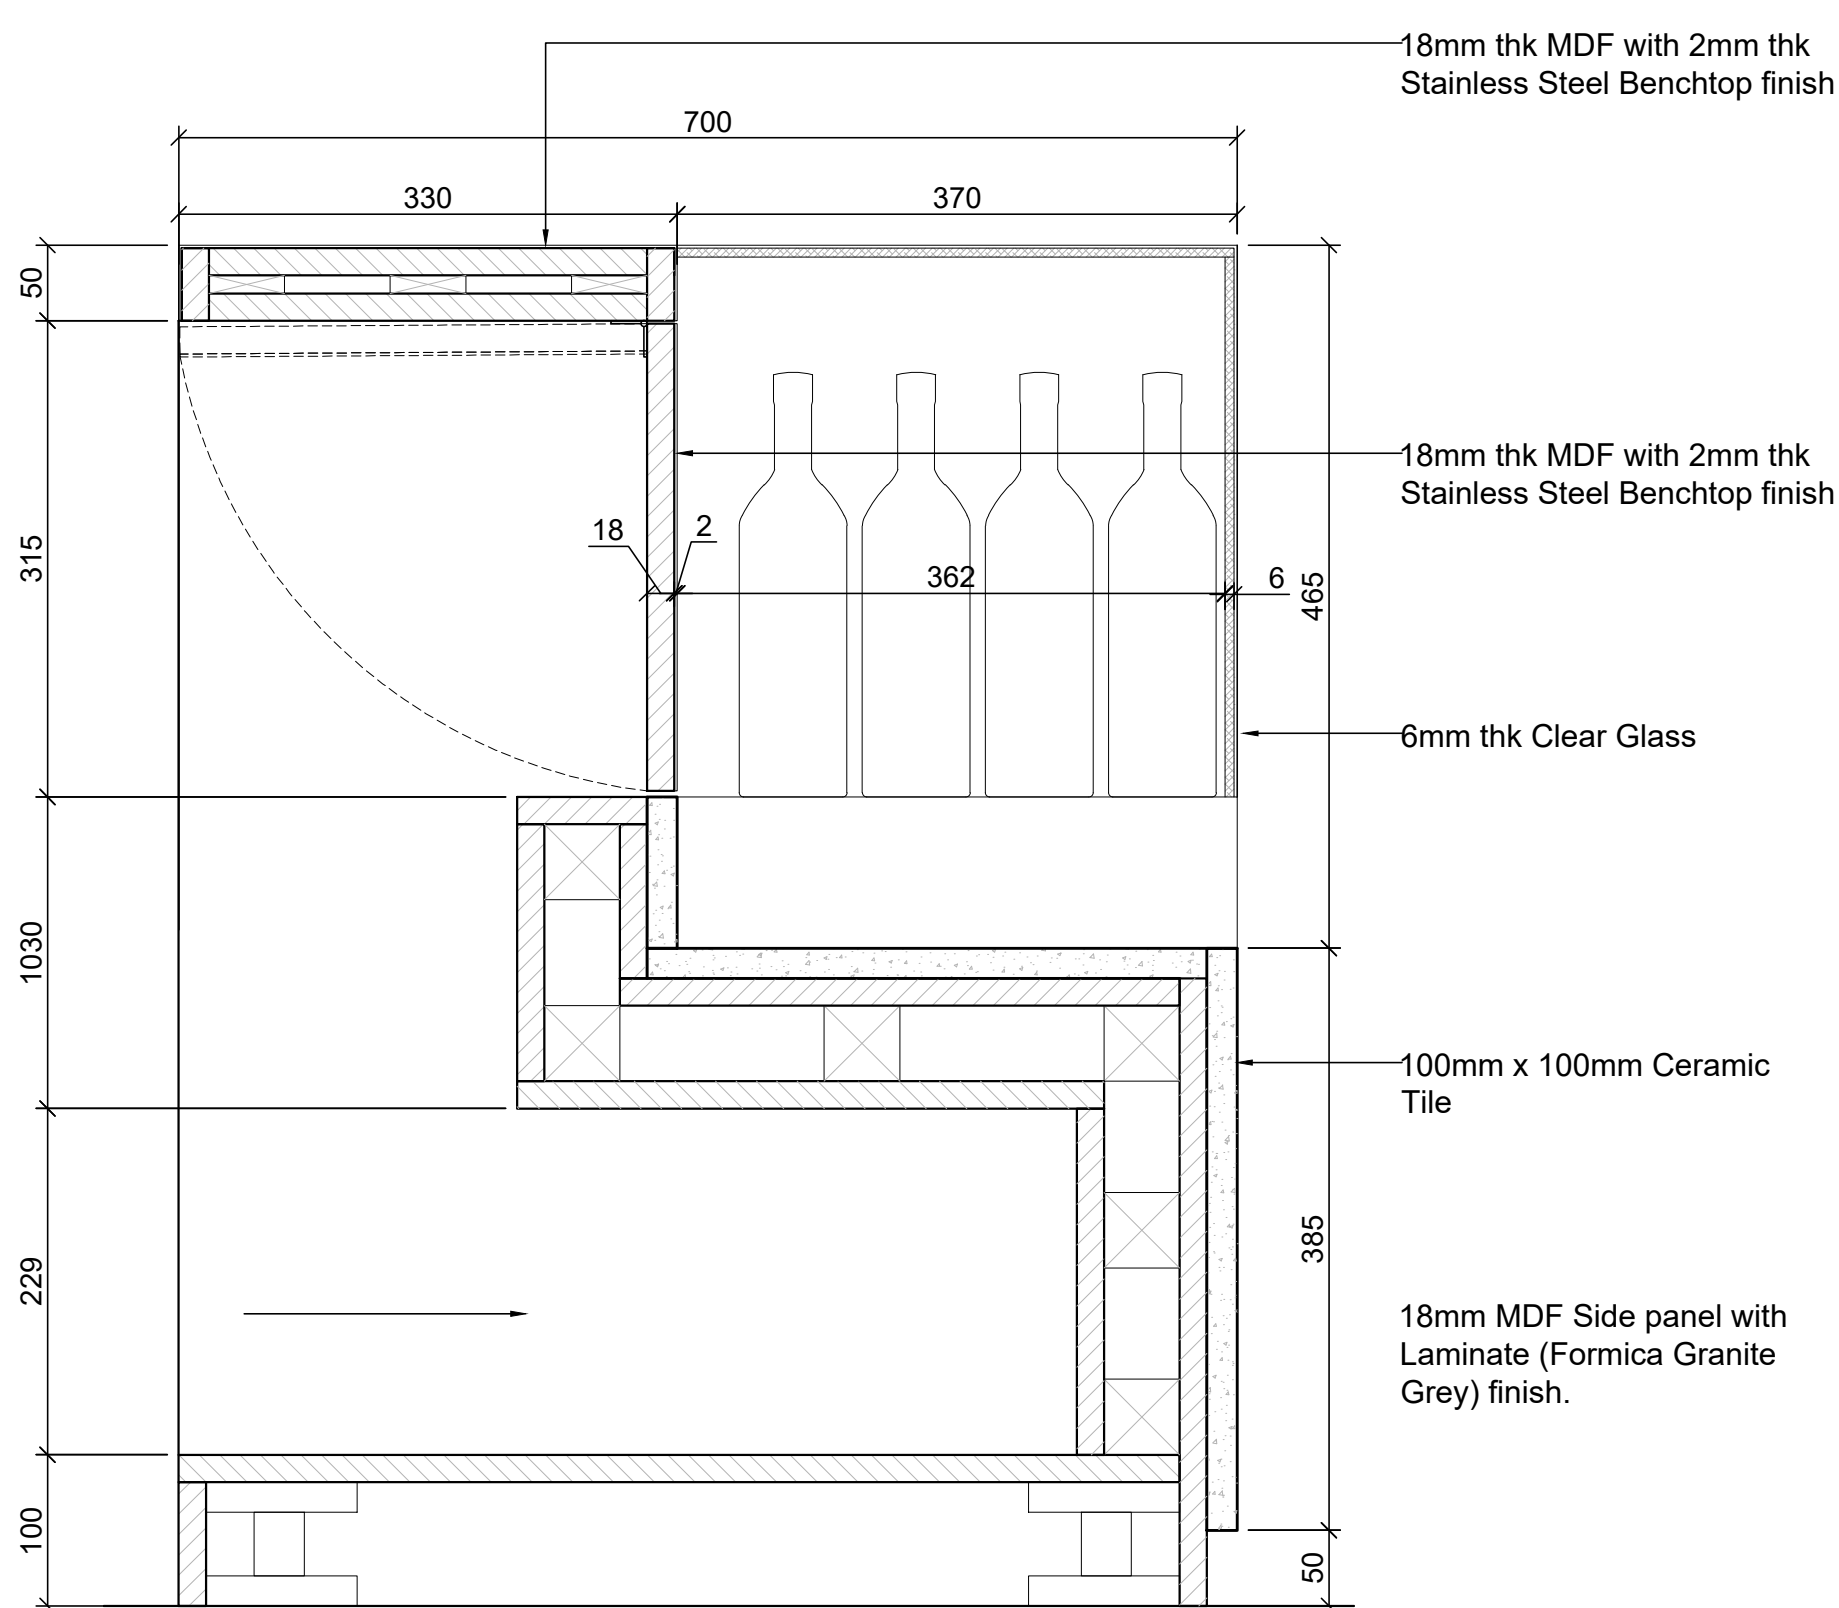

14 DETAIL
Scale: 1:5

FOR APPROVAL



PROJECT:	STW2872
TITLE:	JXX - CAFE BAR
DETAILS:	SECTION & DETAIL
DATE:	04/30/2026
SHEET:	5 OF 5
DRAWN:	JPO
CHECK:	ACA
SCALE:	AS SHOWN @ A1
DRAWING N°:	STW2872- JXX- 05
REVISION:	00