




REVISION HISTORY		
REV	DESCRIPTION	DATE
	FIRST ISSUE	04/30/2026

FOR APPROVAL	
PROJECT:	STW2872
TITLE:	JXX - CIRCULAR PLANTER & BENCH SEAT
DETAILS:	RENDERING
DATE:	04/30/2026
SHEET:	1 OF 4
DRAWN:	JPO
CHECK:	ACA
SCALE:	AS SHOWN @ A1
DRAWING N°:	REVISION:
STW2872– JXX– 01	00

REVISION HISTORY		
REV	DESCRIPTION	DATE
	FIRST ISSUE	04/30/2026

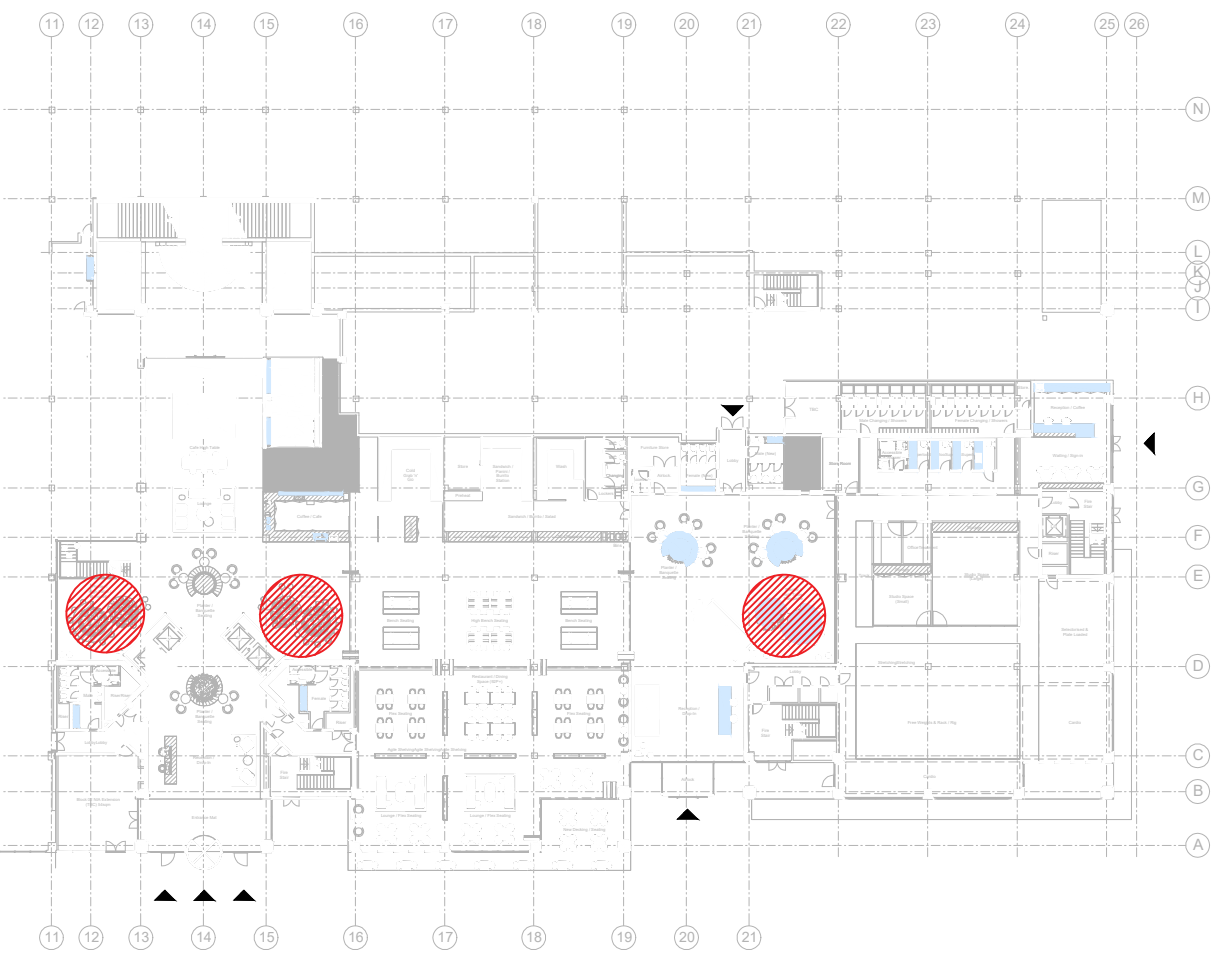

KEYPLAN



2x6mm (6mm x 2pcs bendy ply) build up construction for legs with 2mm Kronospan AL06 brushed bronze finished both sides.

3x6mm (6mm x 3pcs bendy ply) build up construction with 2mm Kronospan AL06 brushed bronze finished.

36mm (18mm x 2 pcs MDF) build up construction for circular bench seat with 2mm Egger H1367 ST40 Light Natural Casella oak finish

Site joint - pattern to be as consistent as possible

36mm (18mmx2 MDF) build up construction for bench legs in Egger H1367 ST40 Light Natural Casella oak finish

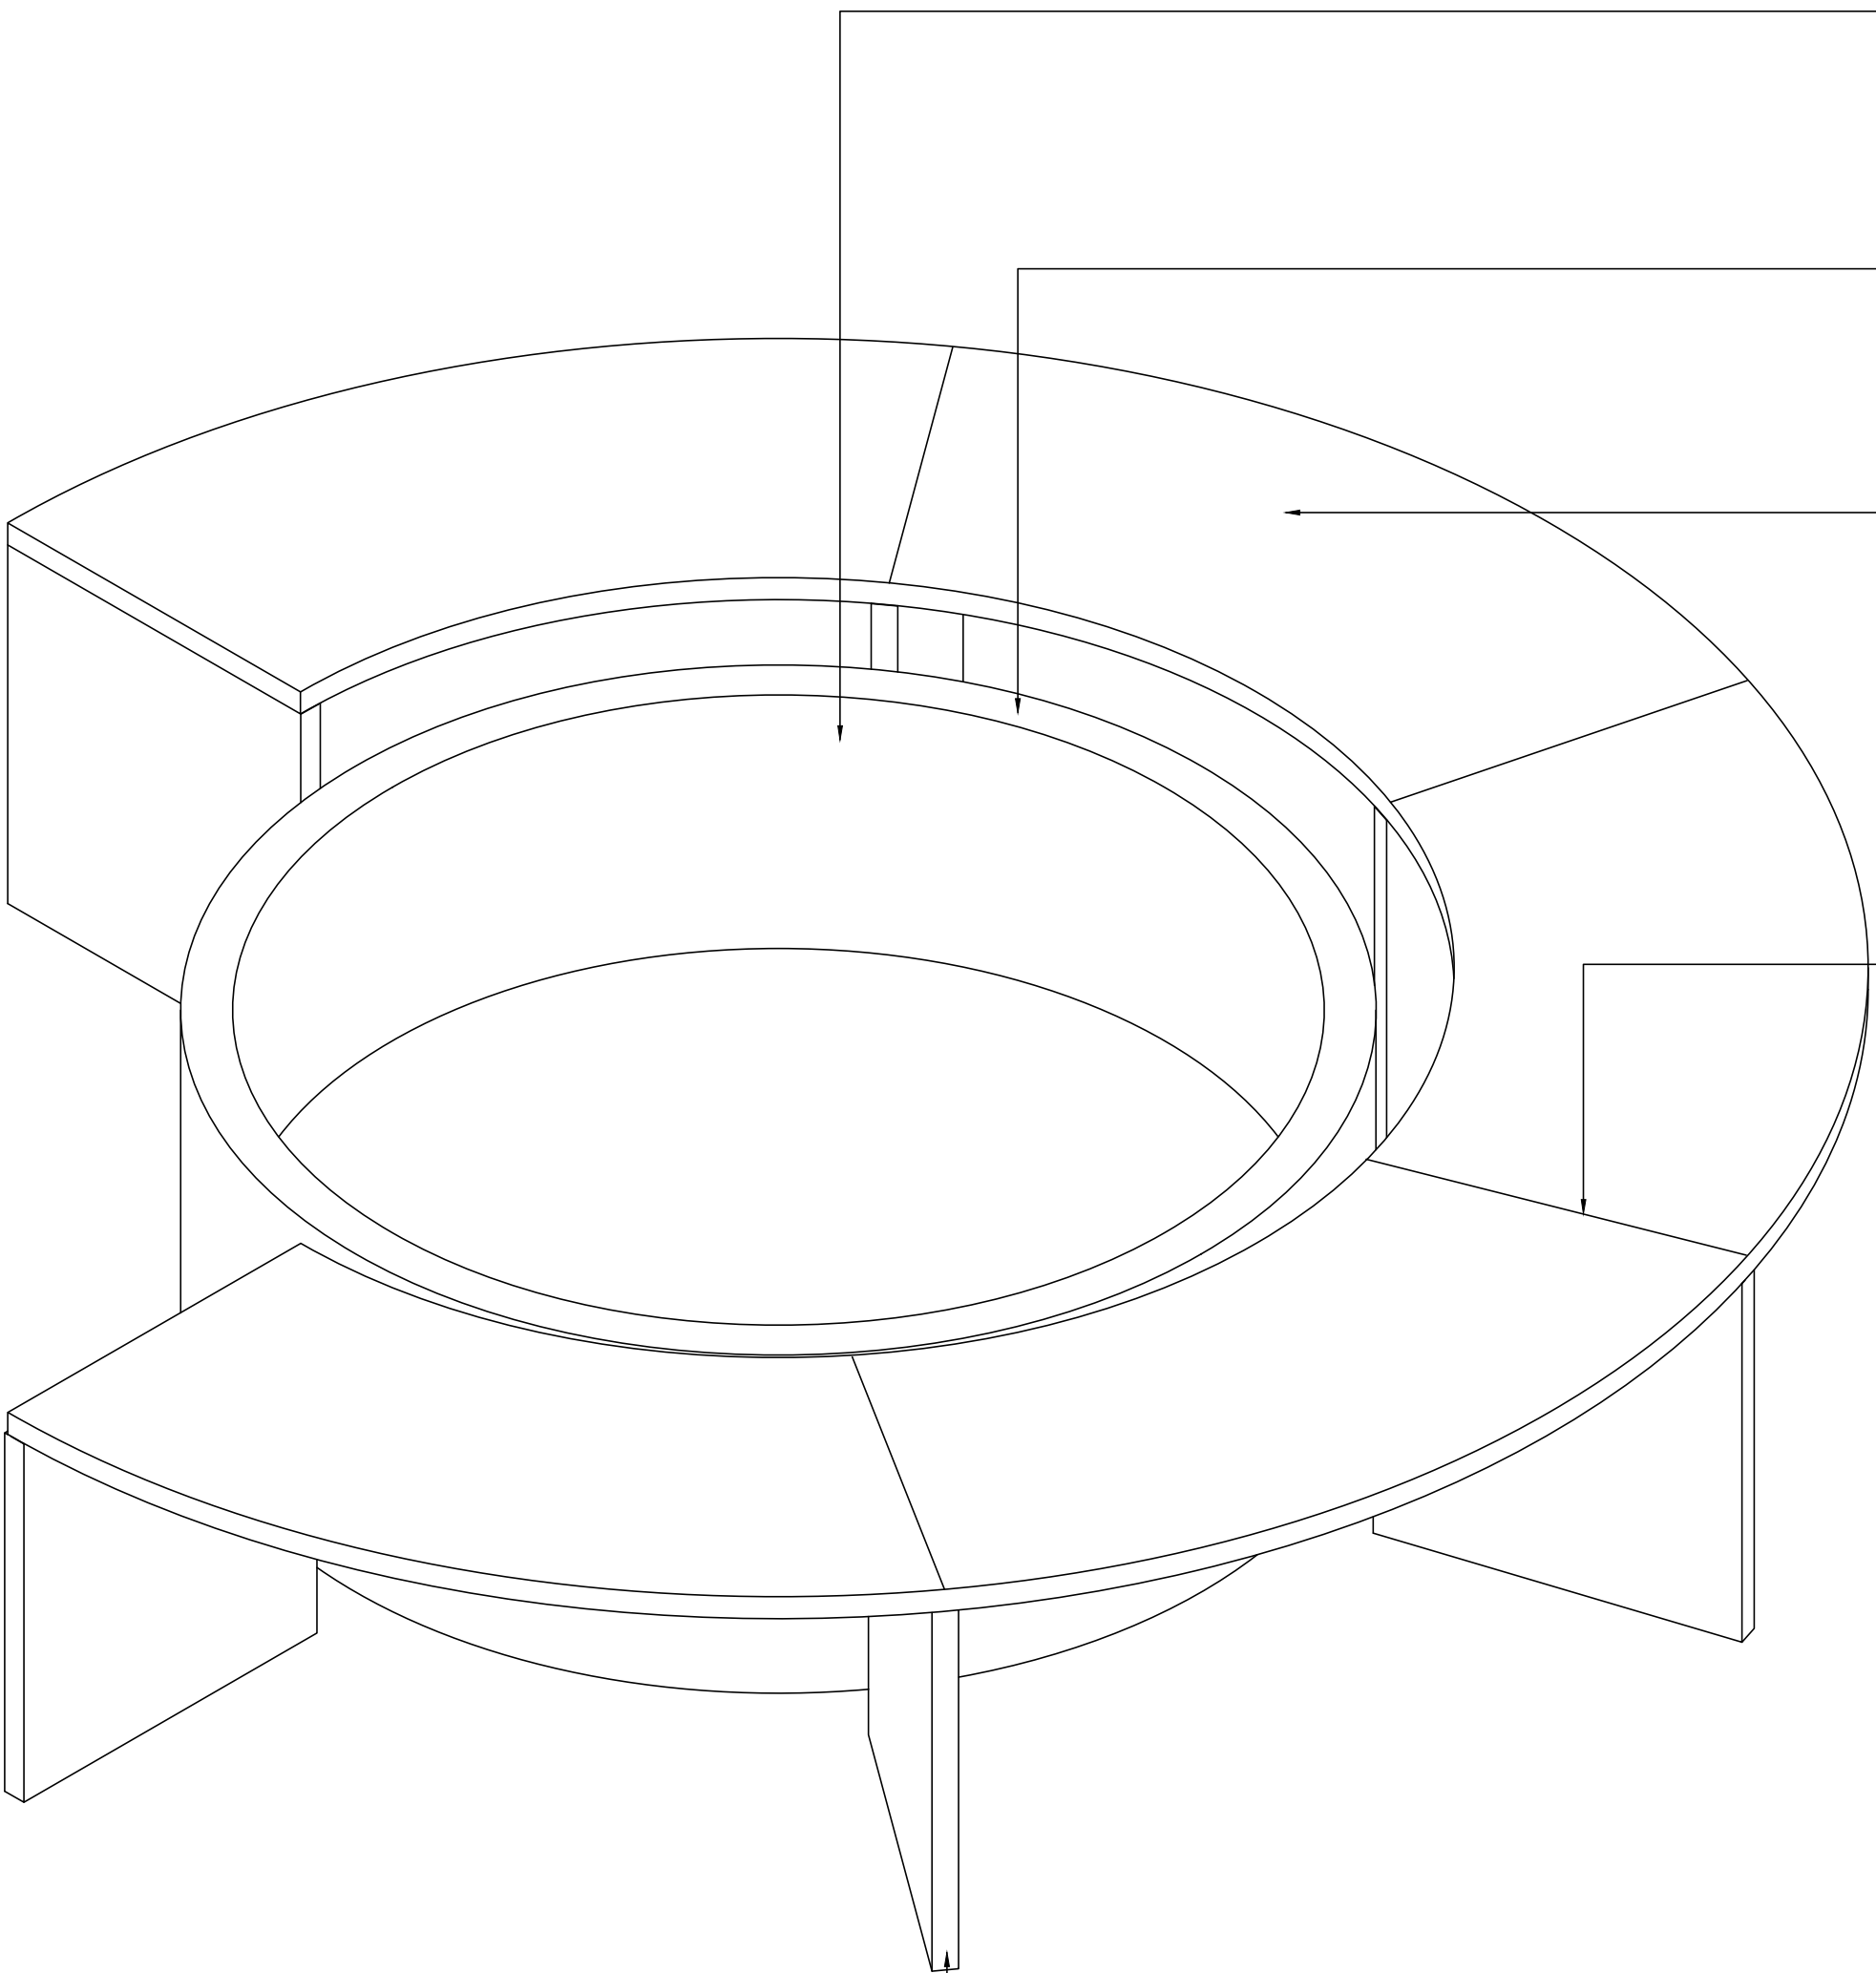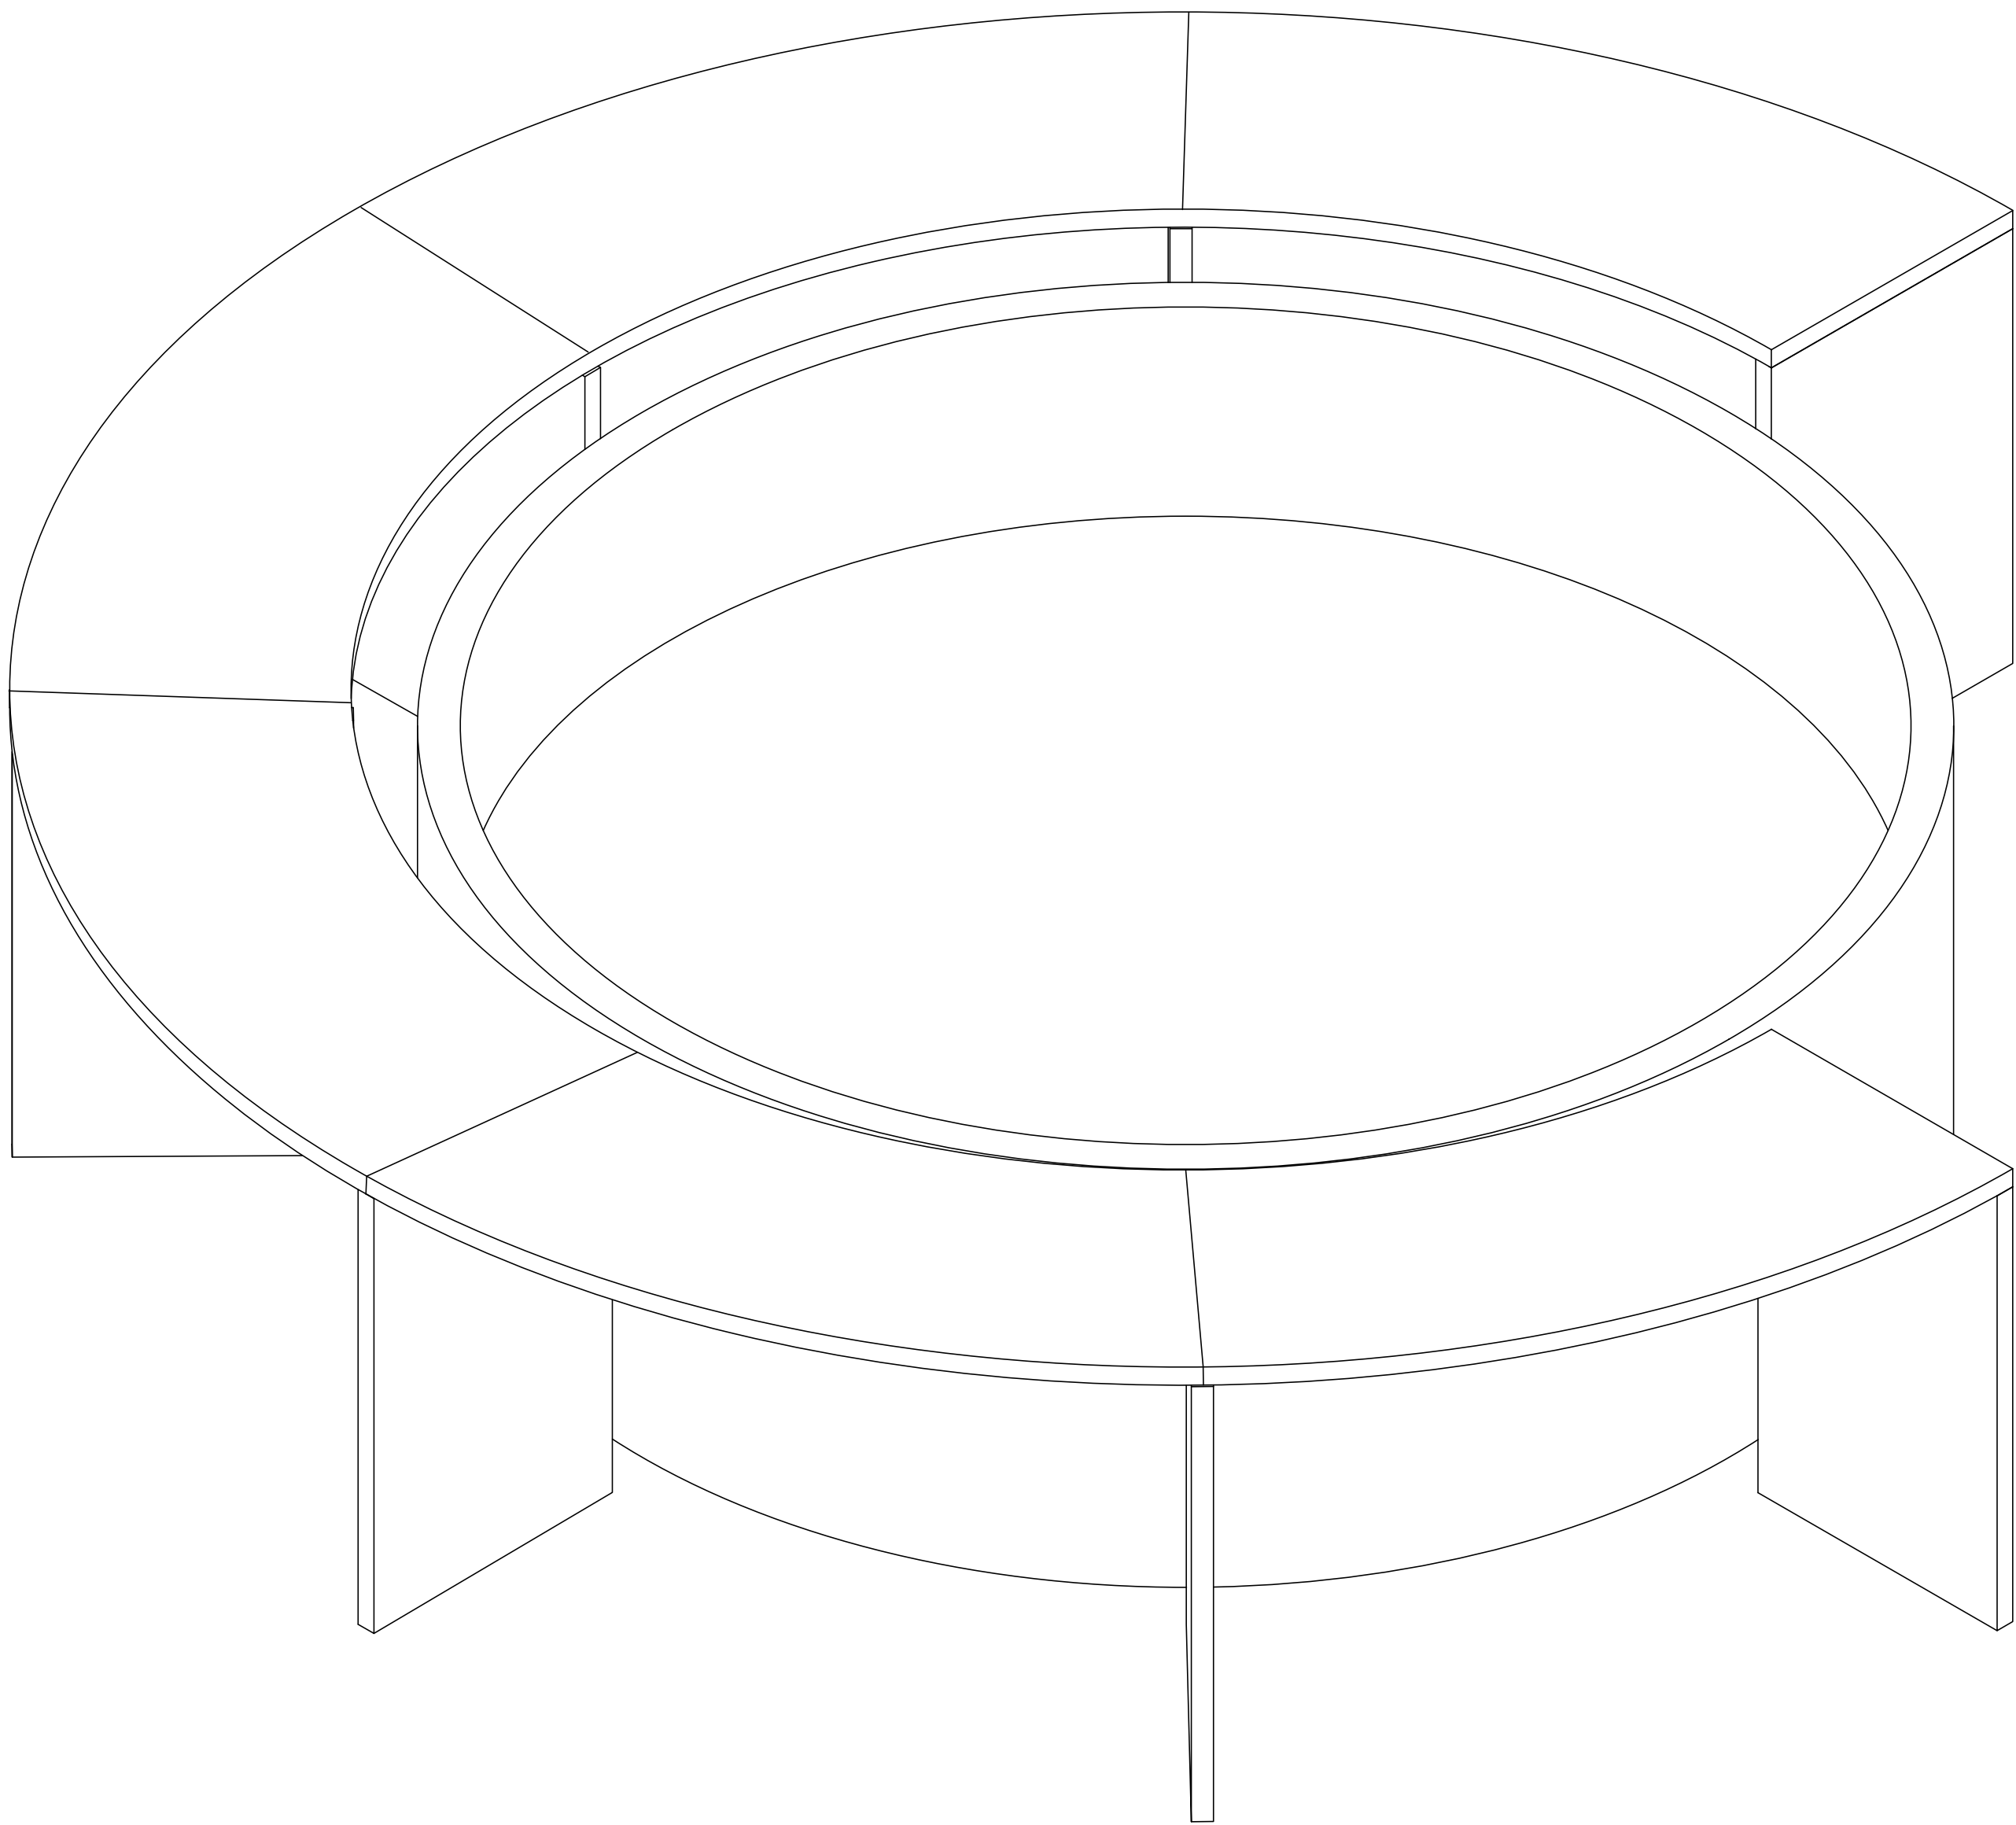


ISOMETRIC
Scale: NTS

FOR APPROVAL




PROJECT:	STW2872
TITLE:	JXX - CIRCULAR PLANTER & BENCH SEAT
DETAILS:	ISOMETRIC
DATE:	04/30/2026
SHEET:	2 OF 4
DRAWN:	JPO
CHECK:	ACA
SCALE:	AS SHOWN @ A1
DRAWING N°:	STW2872– JXX– 02
REVISION:	00

REVISION HISTORY		
REV	DESCRIPTION	DATE
	FIRST ISSUE	04/30/2026

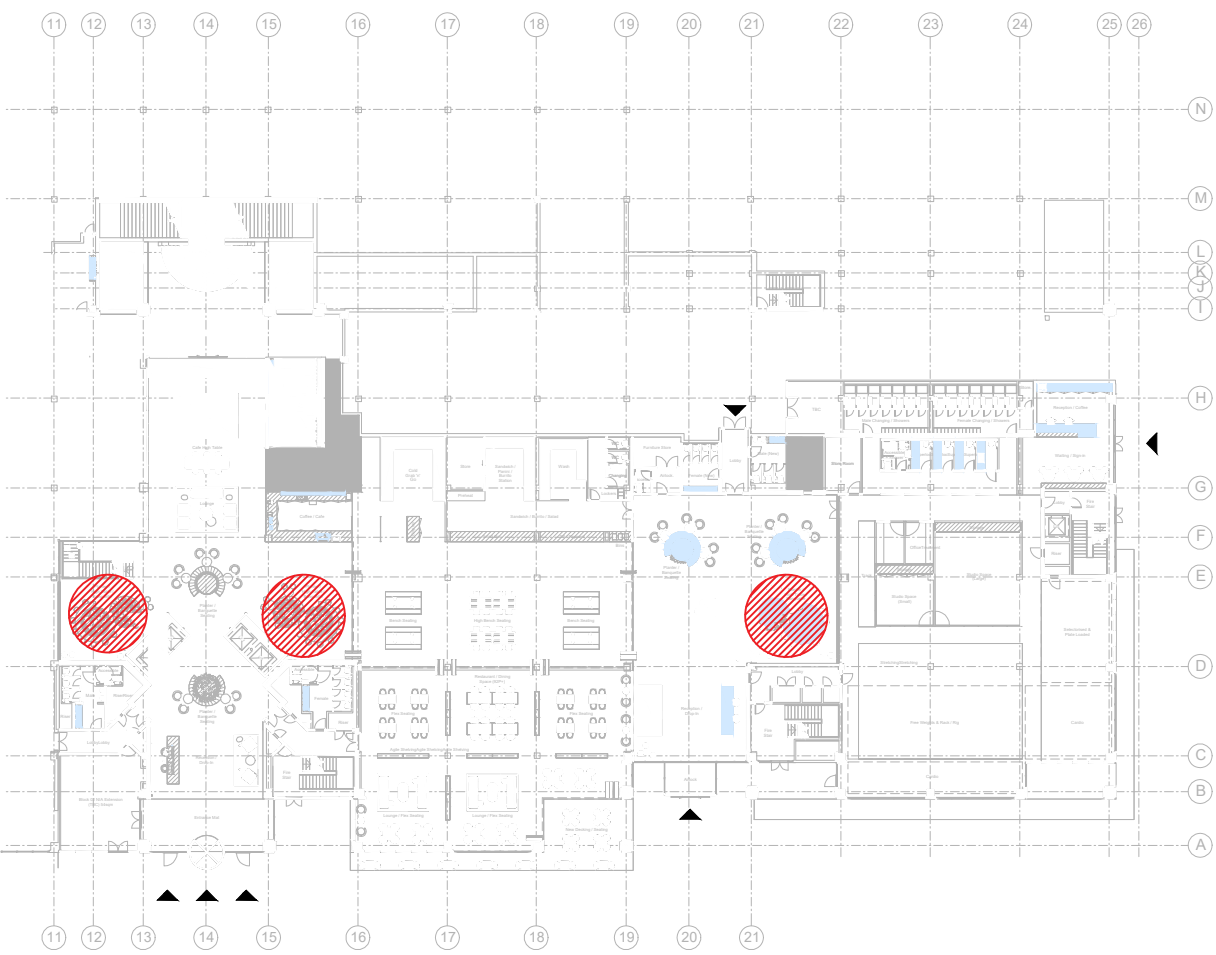


KEYPLAN

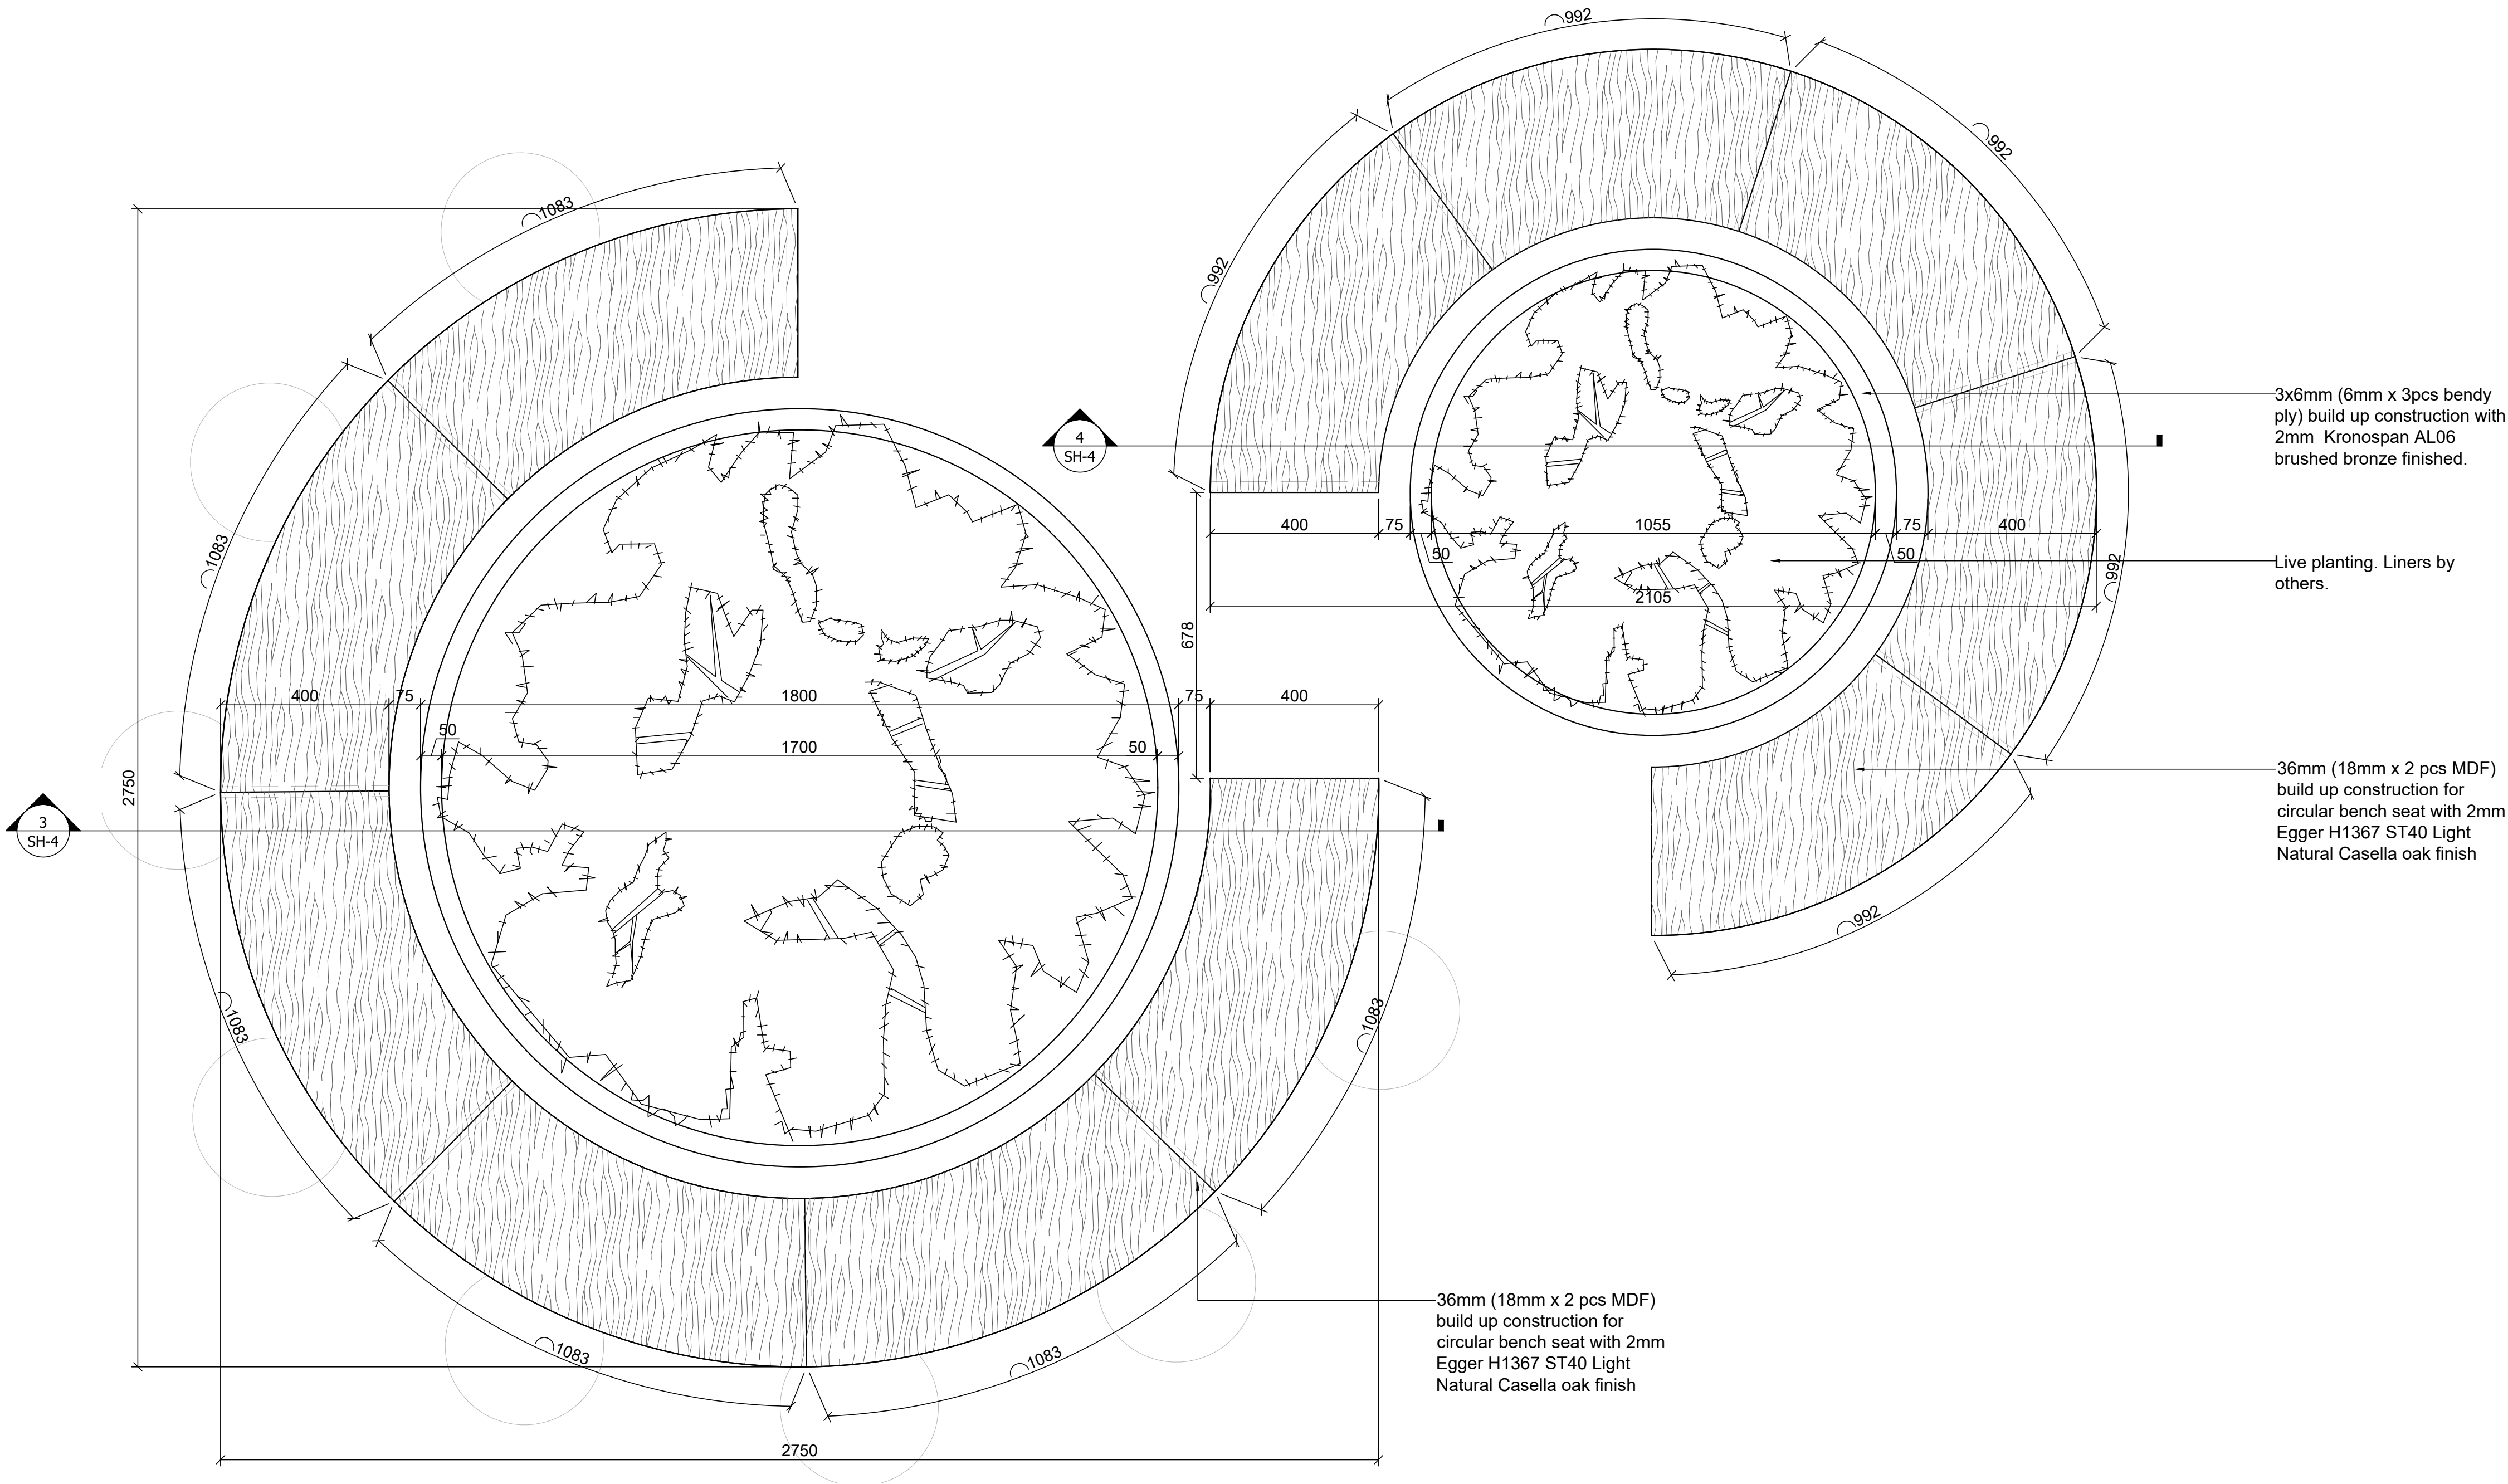

1 PLAN

Scale: 1:10

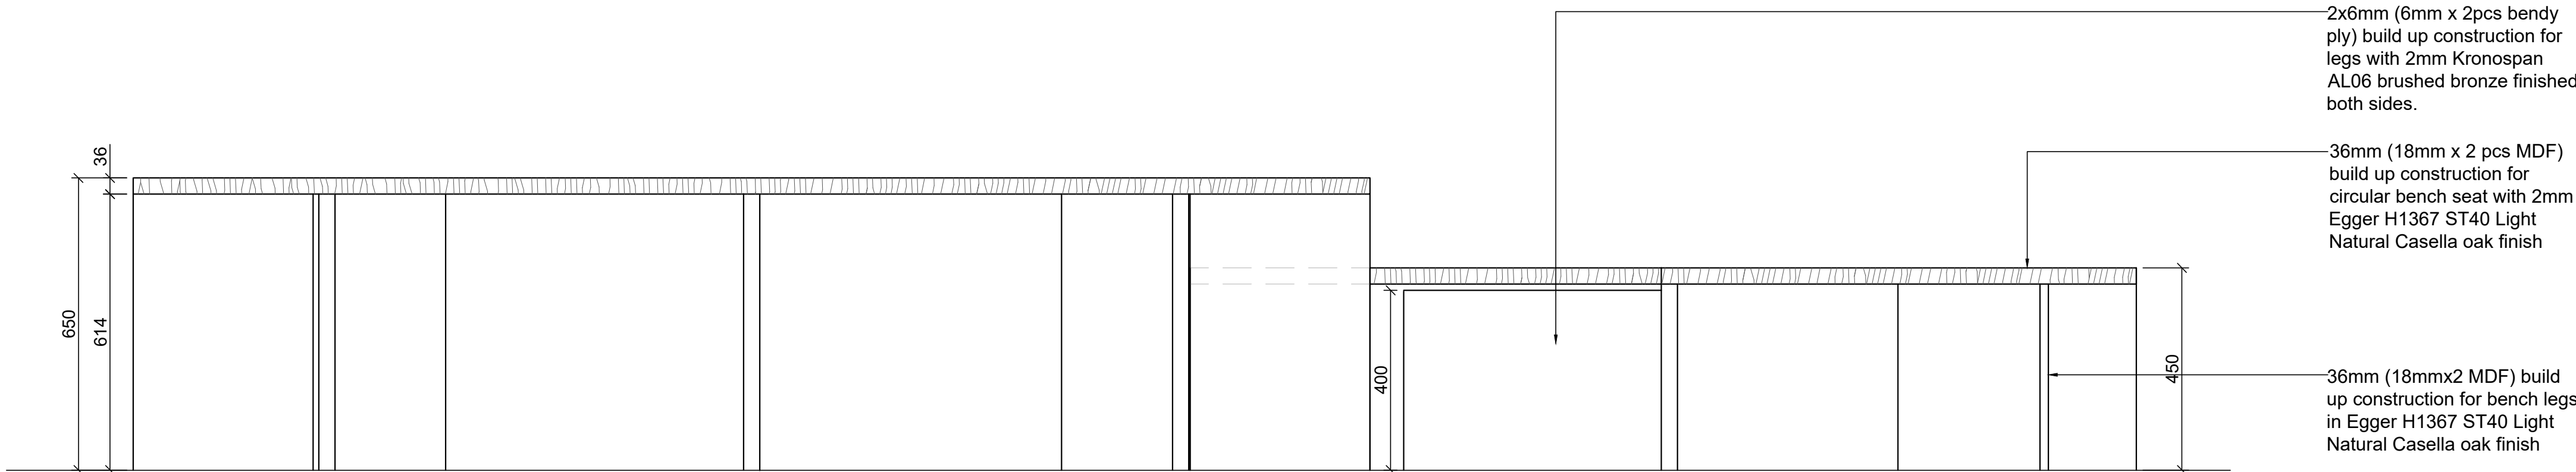

2 FRONT ELEVATION


Scale: 1:10

FOR APPROVAL






PROJECT:	STW2872
TITLE:	JXX - CIRCULAR PLANTER & BENCH SEAT
DETAILS:	PLAN & ELEVATION
DATE:	04/30/2026
SHEET:	3 OF 4
DRAWN:	JPO
CHECK:	ACA
SCALE:	AS SHOWN @ A1
DRAWING N°:	STW2872- JXX- 03
REVISION:	00

REVISION HISTORY		
REV	DESCRIPTION	DATE
	FIRST ISSUE	04/30/2026

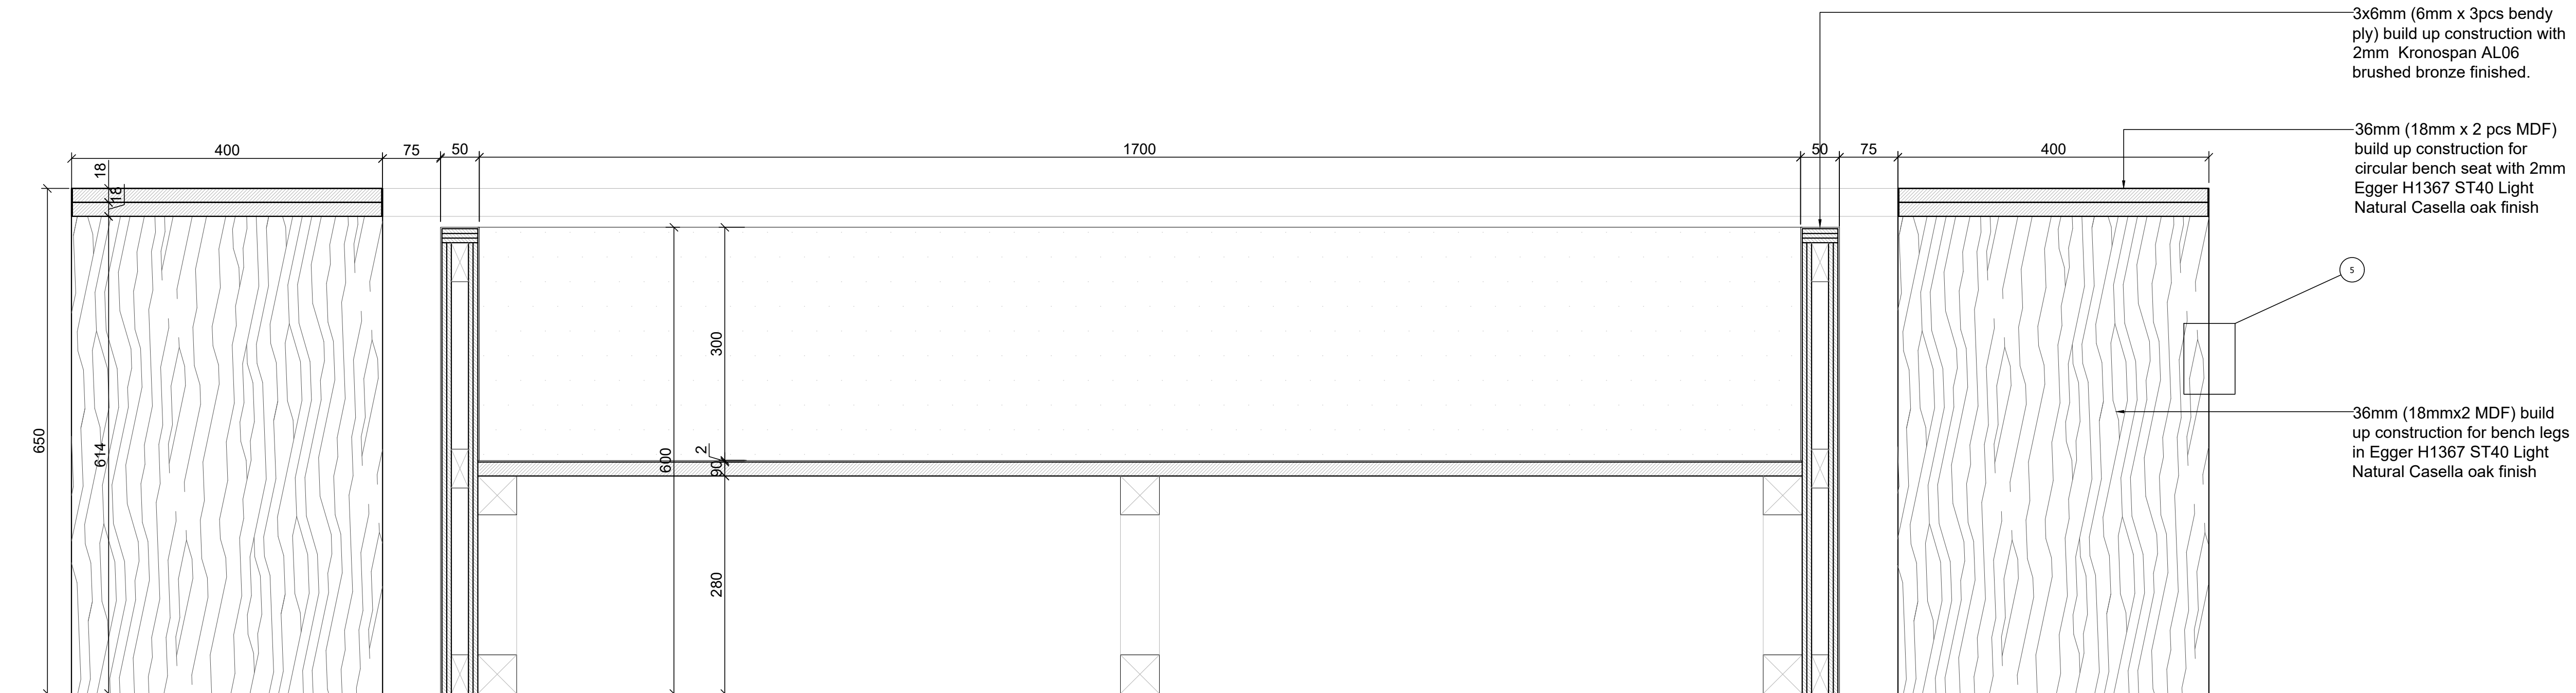

3 SECTION _____ Scale: 1:5

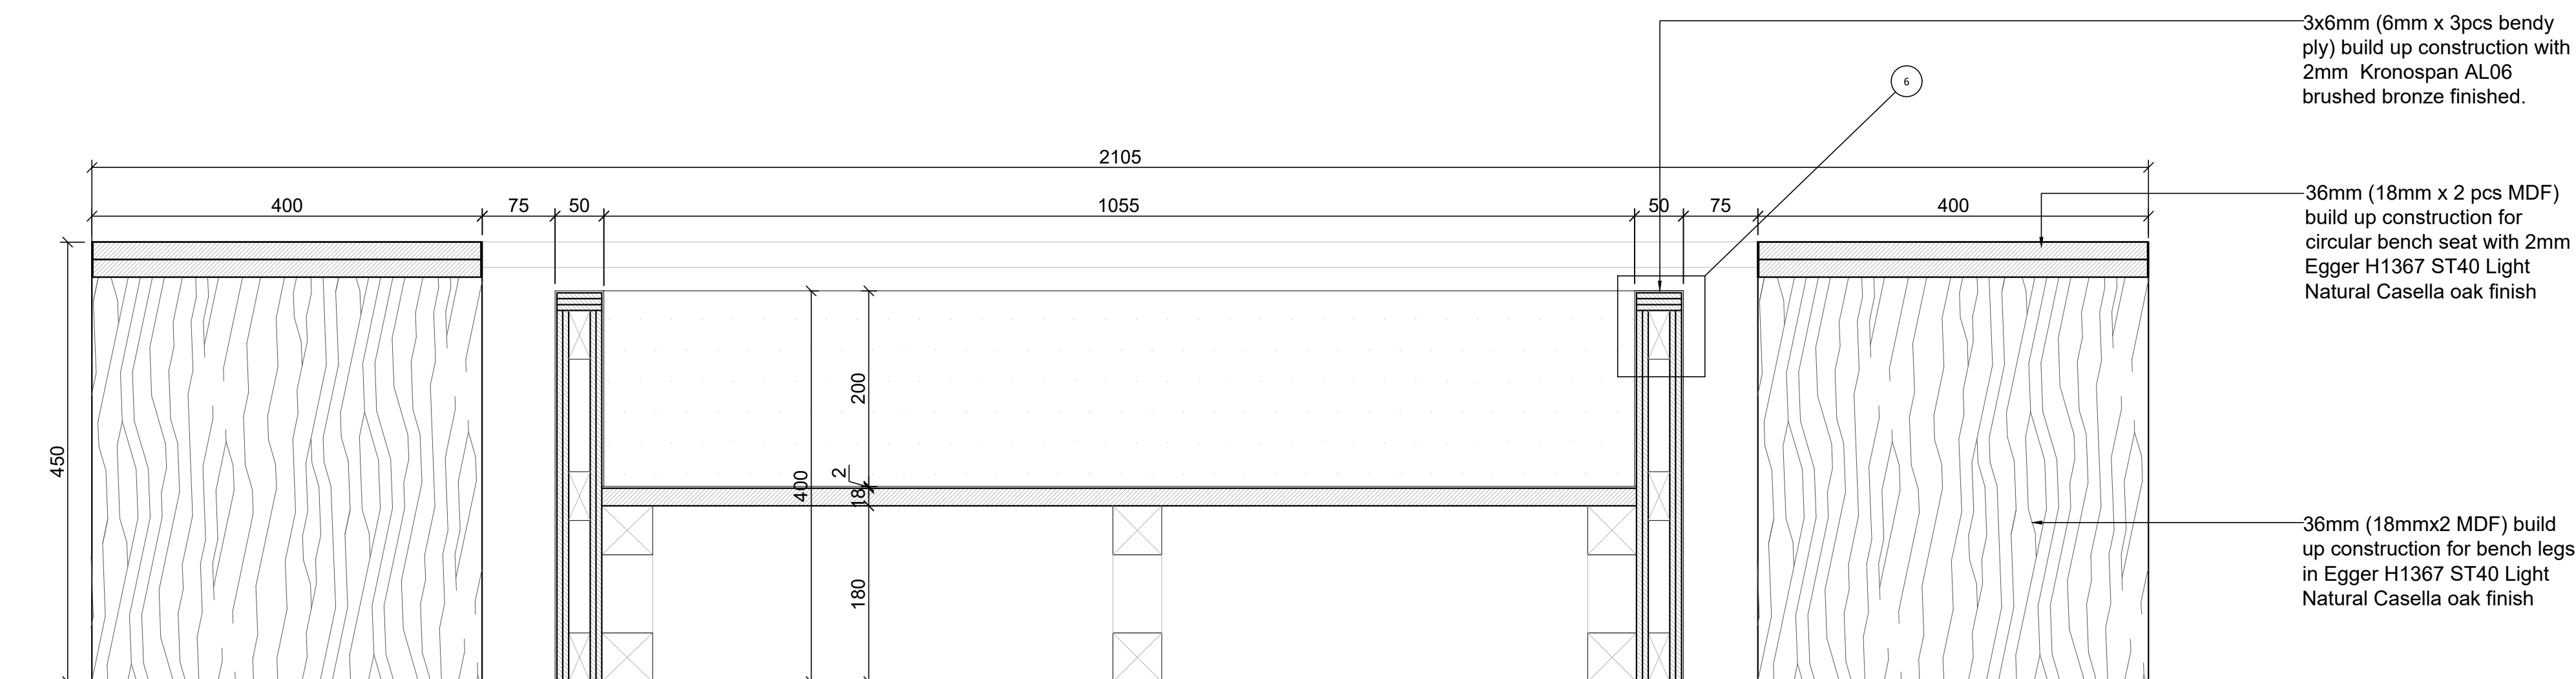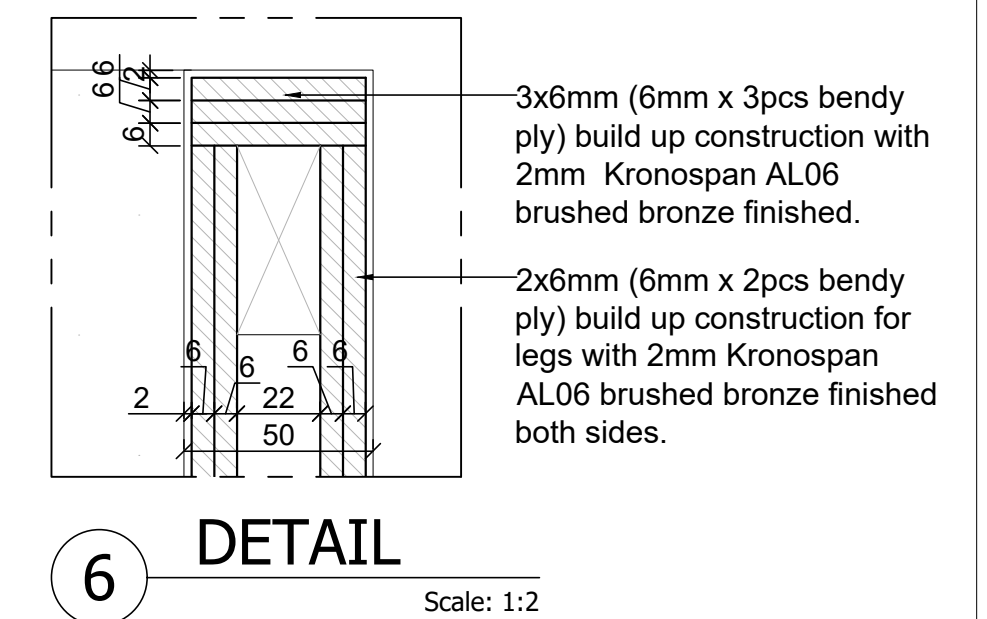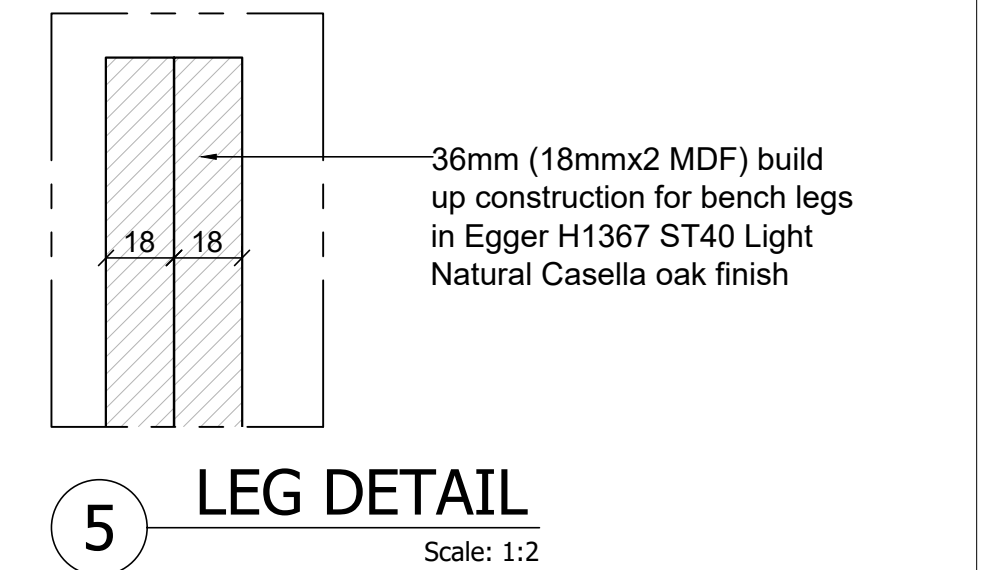

4 SECTION Scale: 1:5

FOR APPROVAL



PROJECT:	STW2872
TITLE:	JXX - CIRCULAR PLANTER & BENCH SEAT
DETAILS:	DETAILS
DATE:	04/30/2026
SHEET:	4 OF 4
DRAWN:	JPO
CHECK:	ACA
SCALE:	AS SHOWN @ A1
DRAWING N°:	REVISION:
STW2872– JXX– 04	00