









REVISION HISTORY		
REV	DESCRIPTION	DATE
	FIRST ISSUE	03/23/2026

FOR APPROVAL



PROJECT:	STW2732		
TITLE:	JXX - L SHAPED WALL PANEL		
DETAILS:	RENDERING		
DATE:	03/23/2026		
SHEET:	1 OF 3		
DRAWN:	JPO		
CHECK:	ACA		
SCALE:	AS SHOWN @ A1		
DRAWING N°:			REVISION:
STW2732– JXX– 01			00

REVISION HISTORY		
REV	DESCRIPTION	DATE
	FIRST ISSUE	03/23/2026

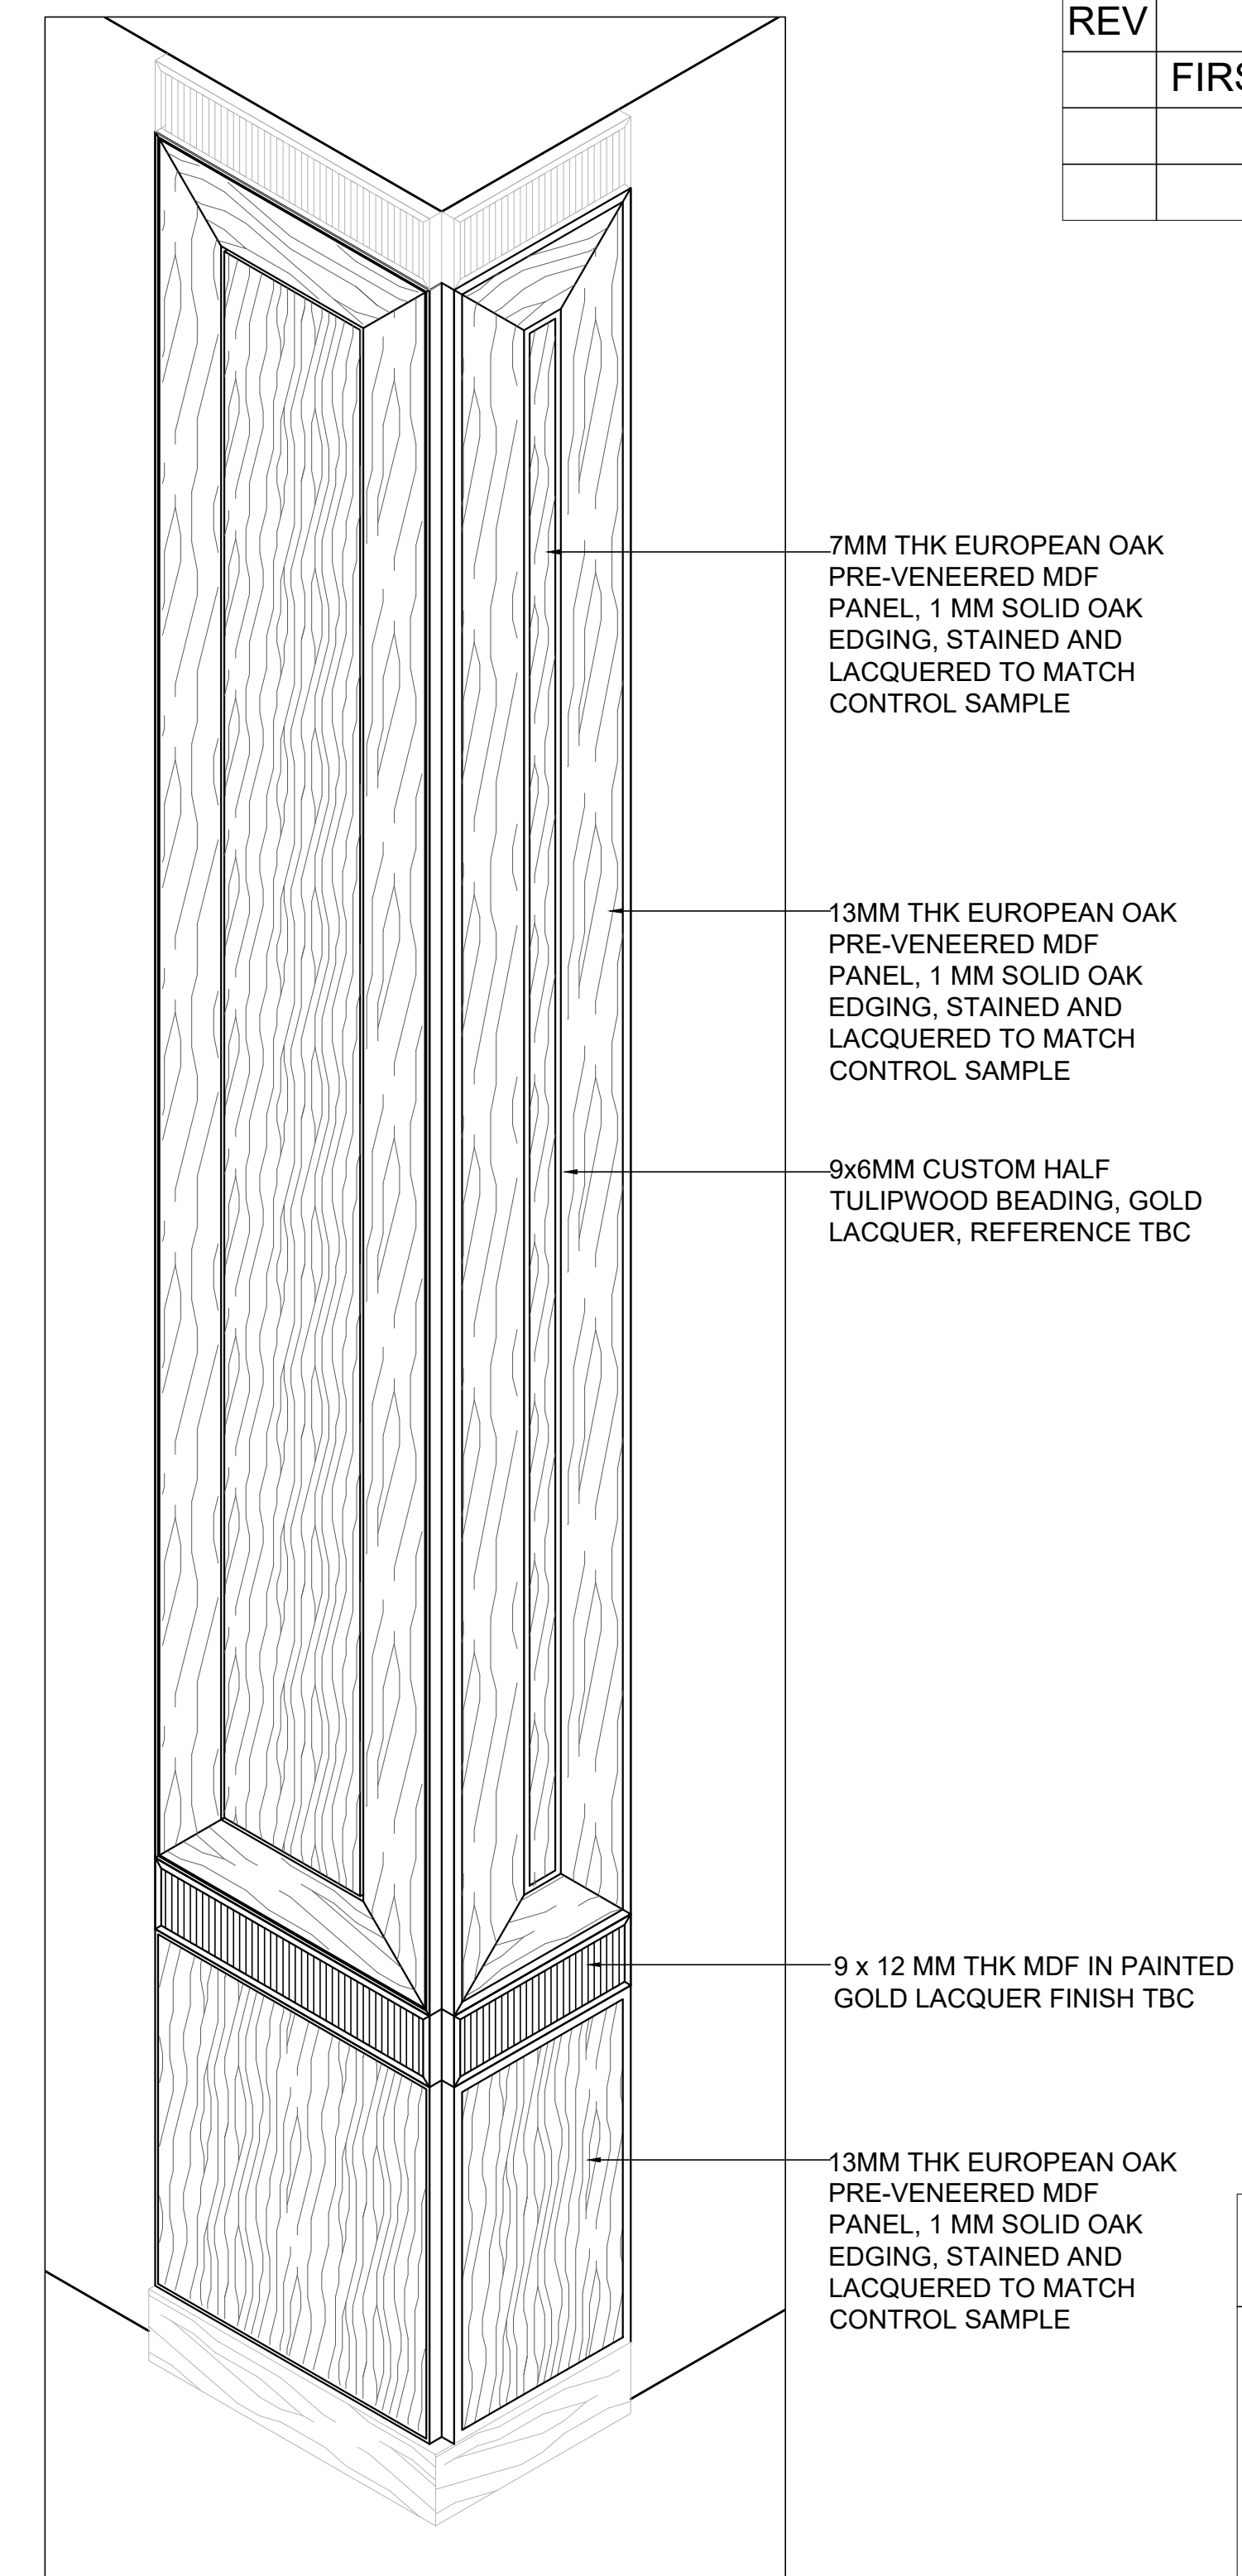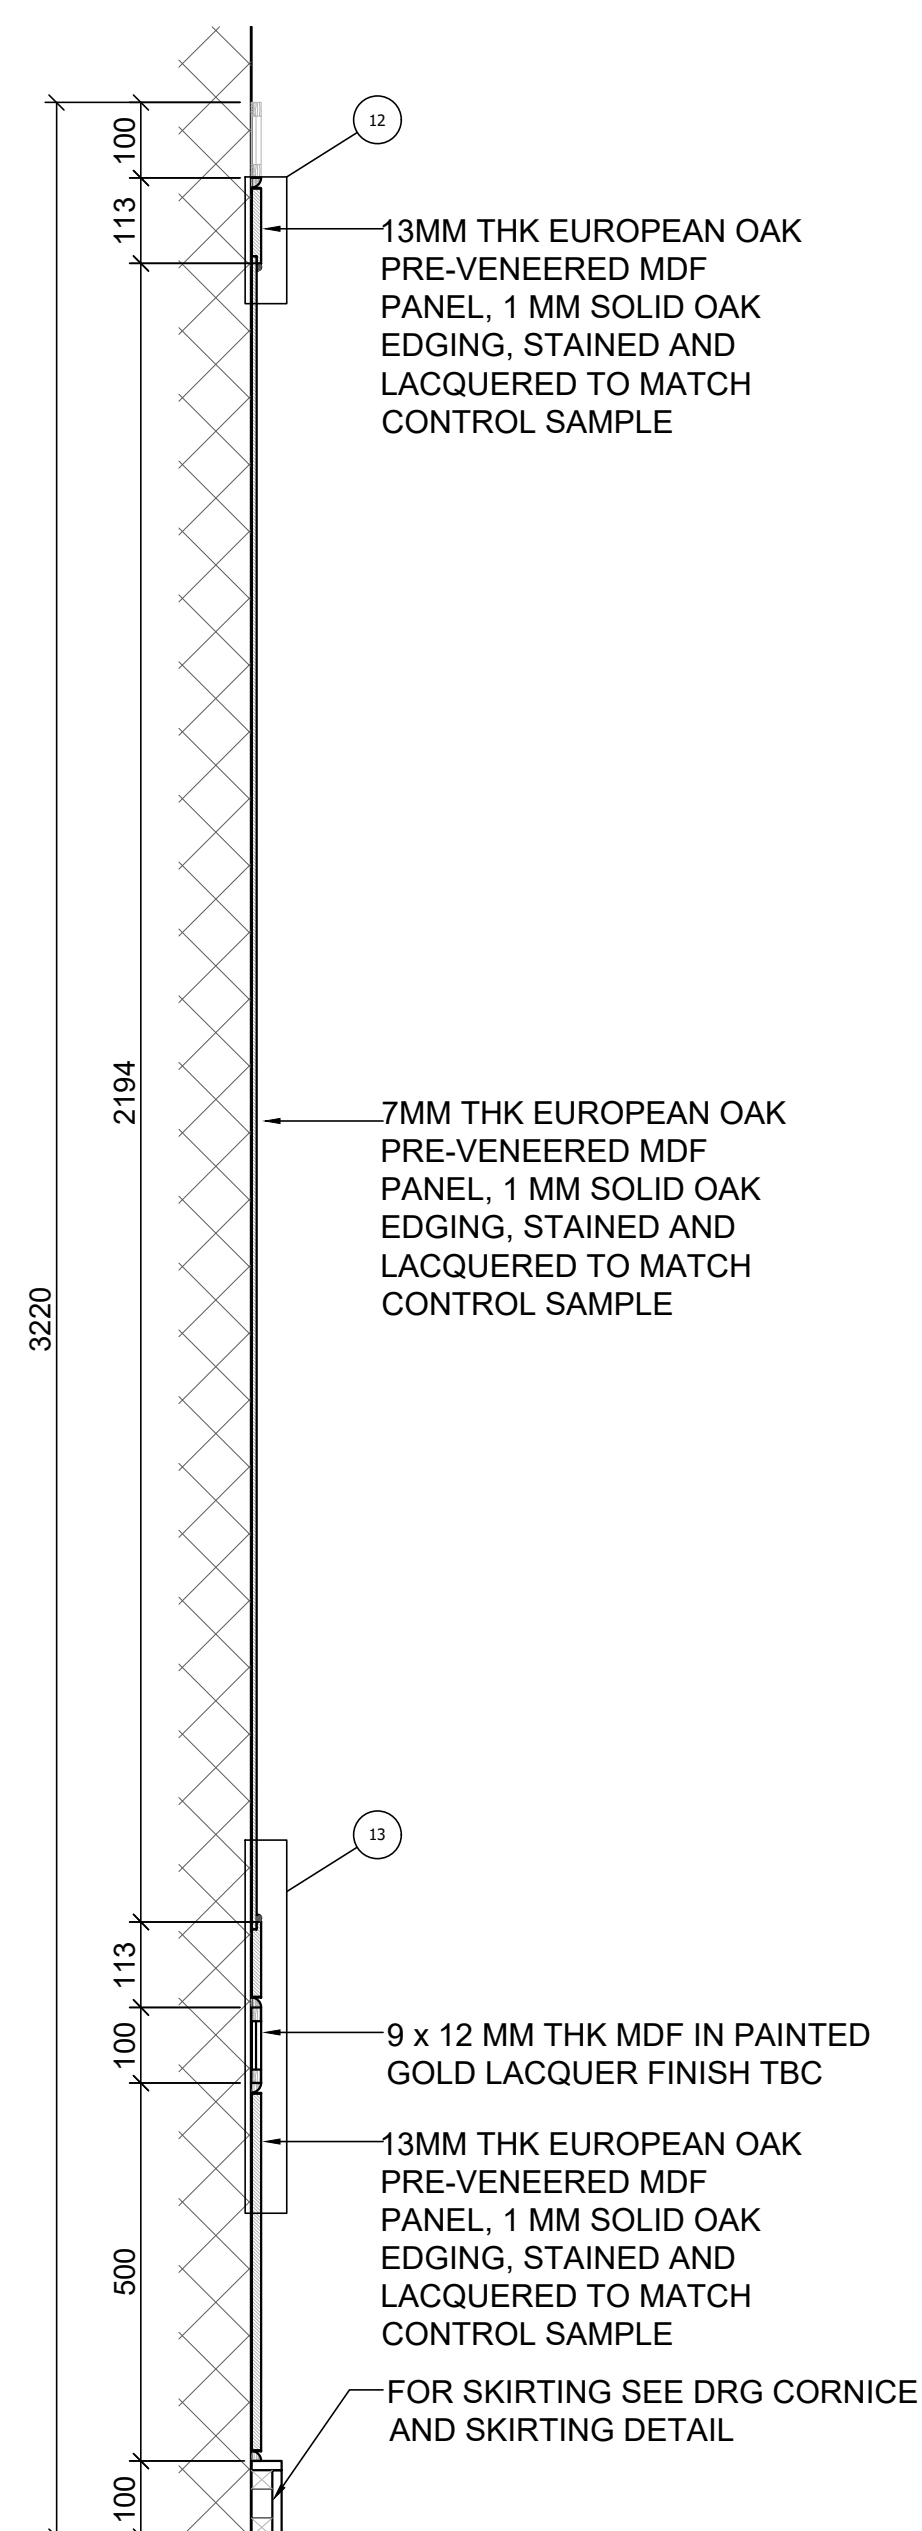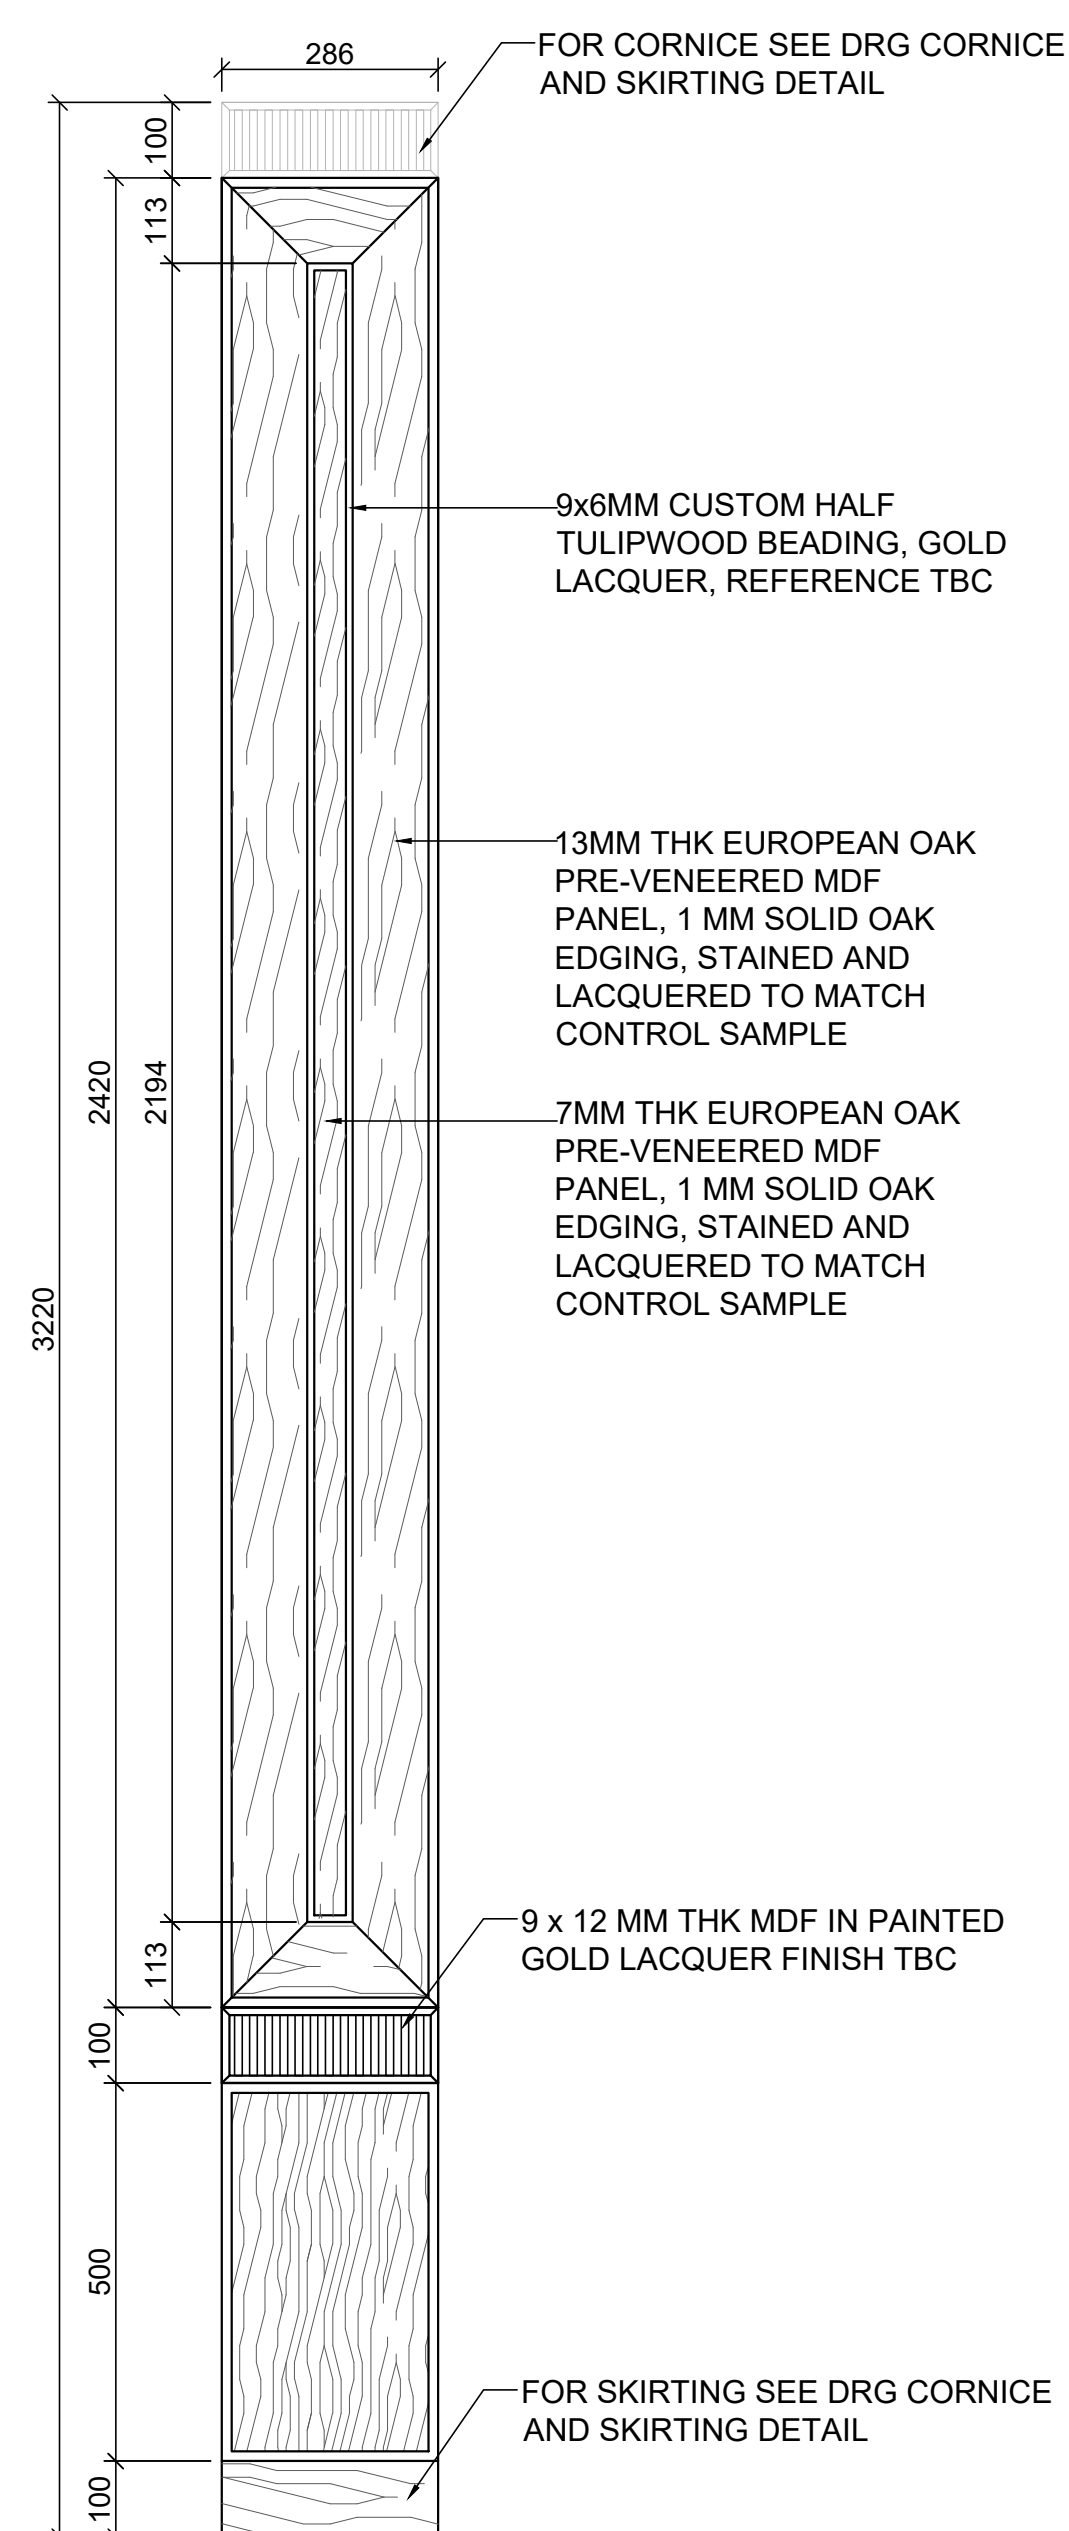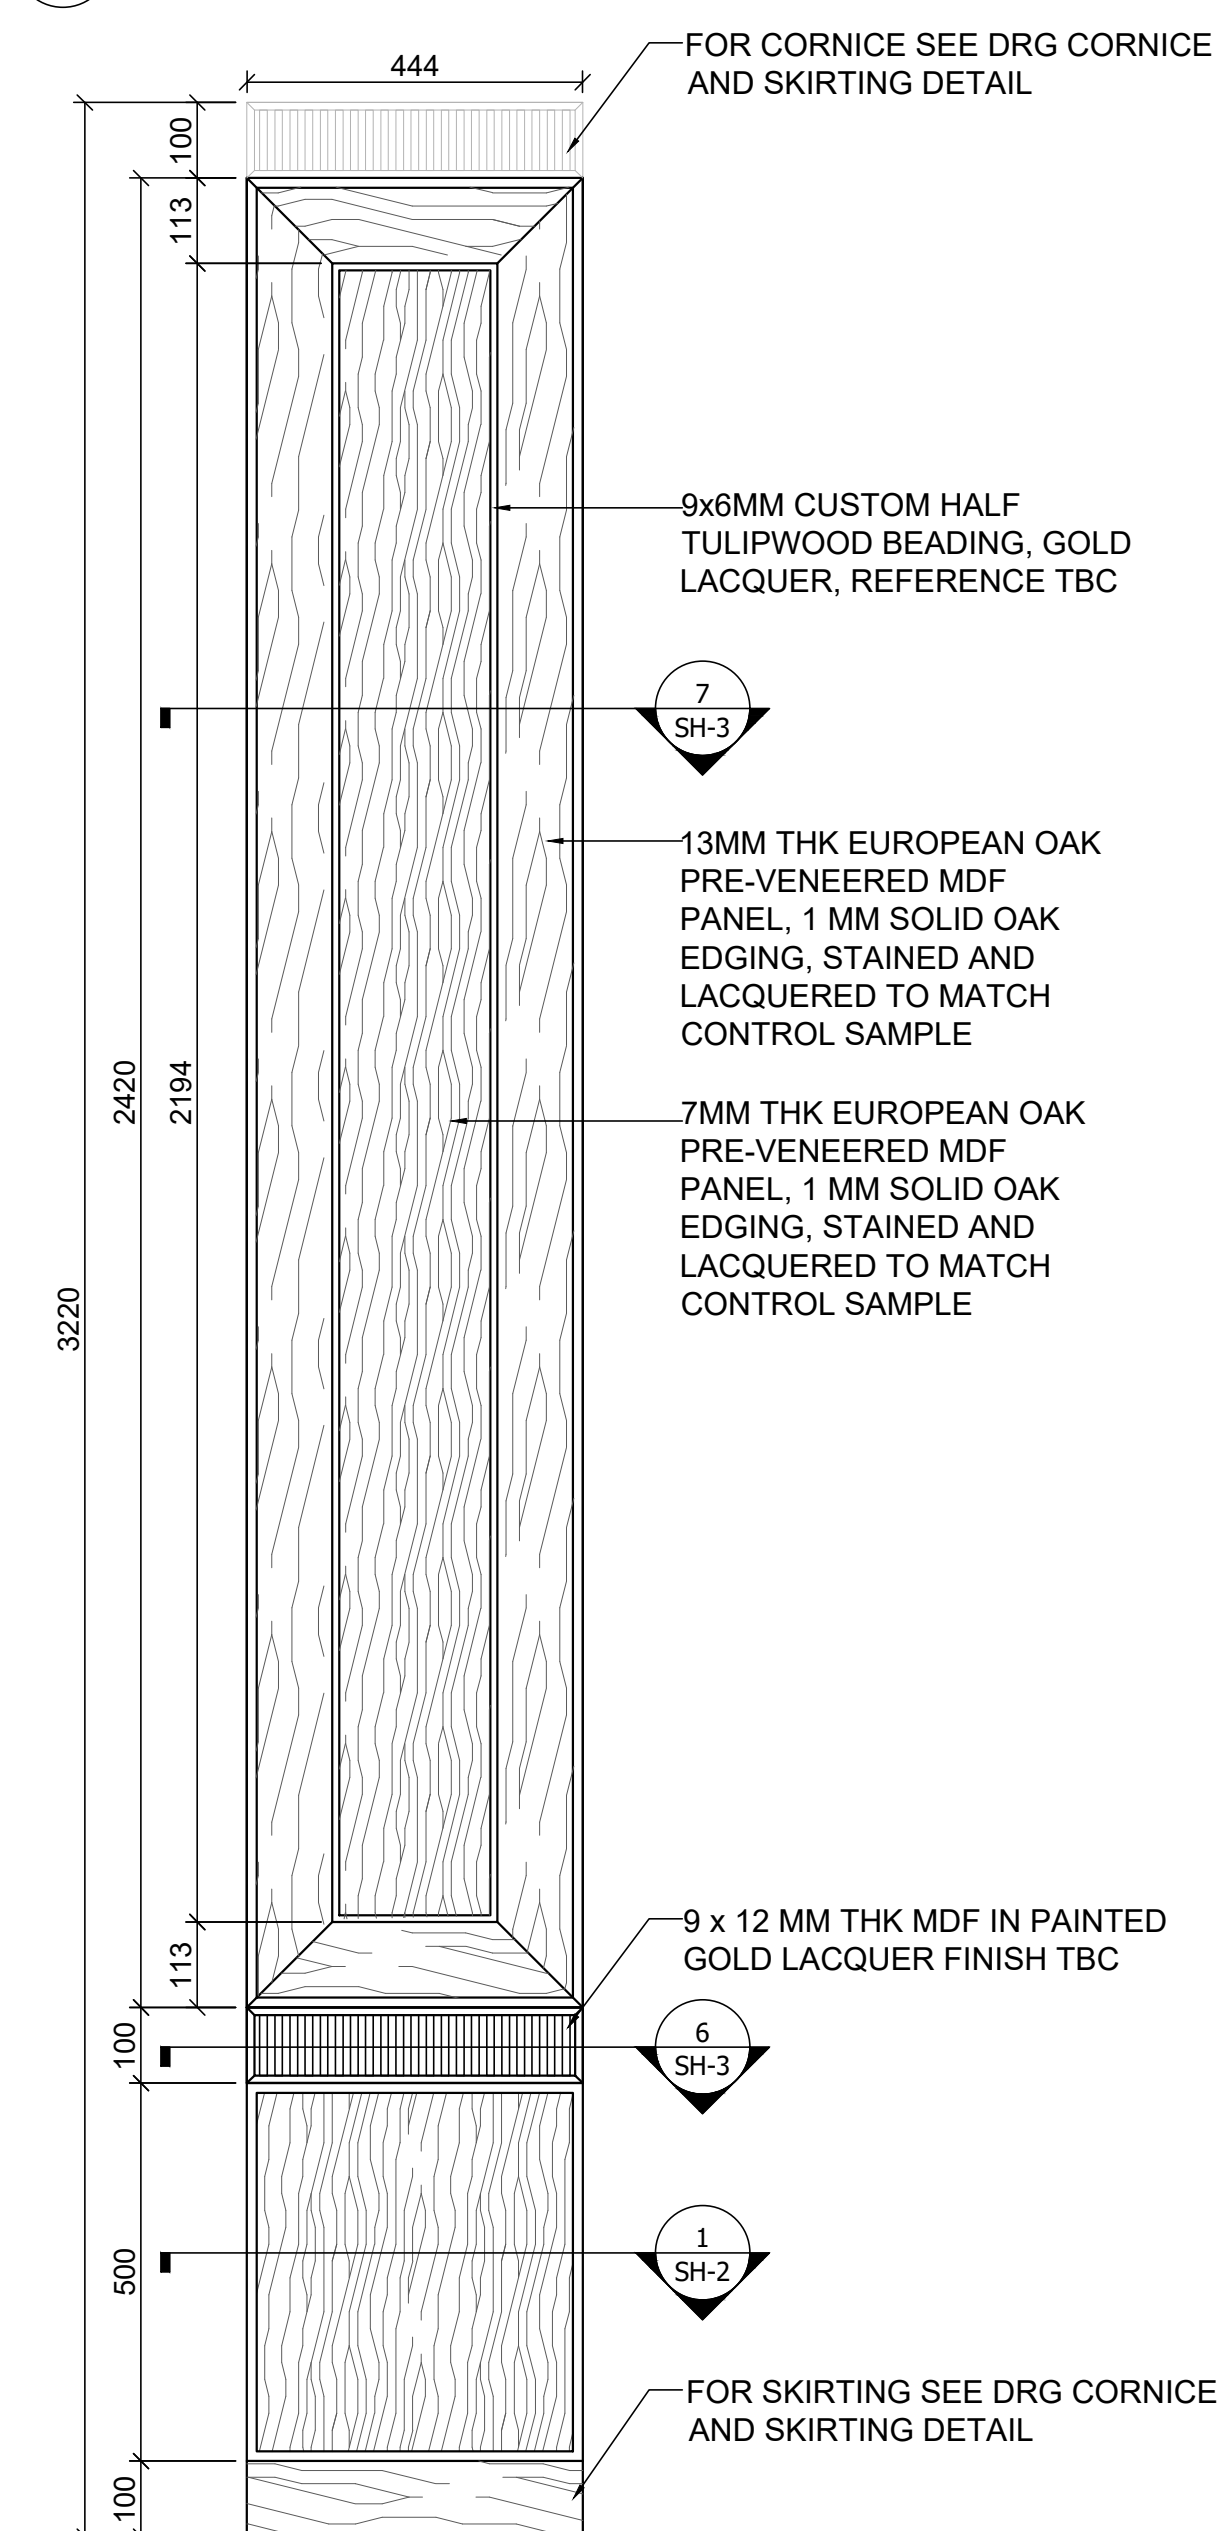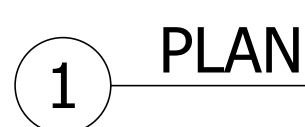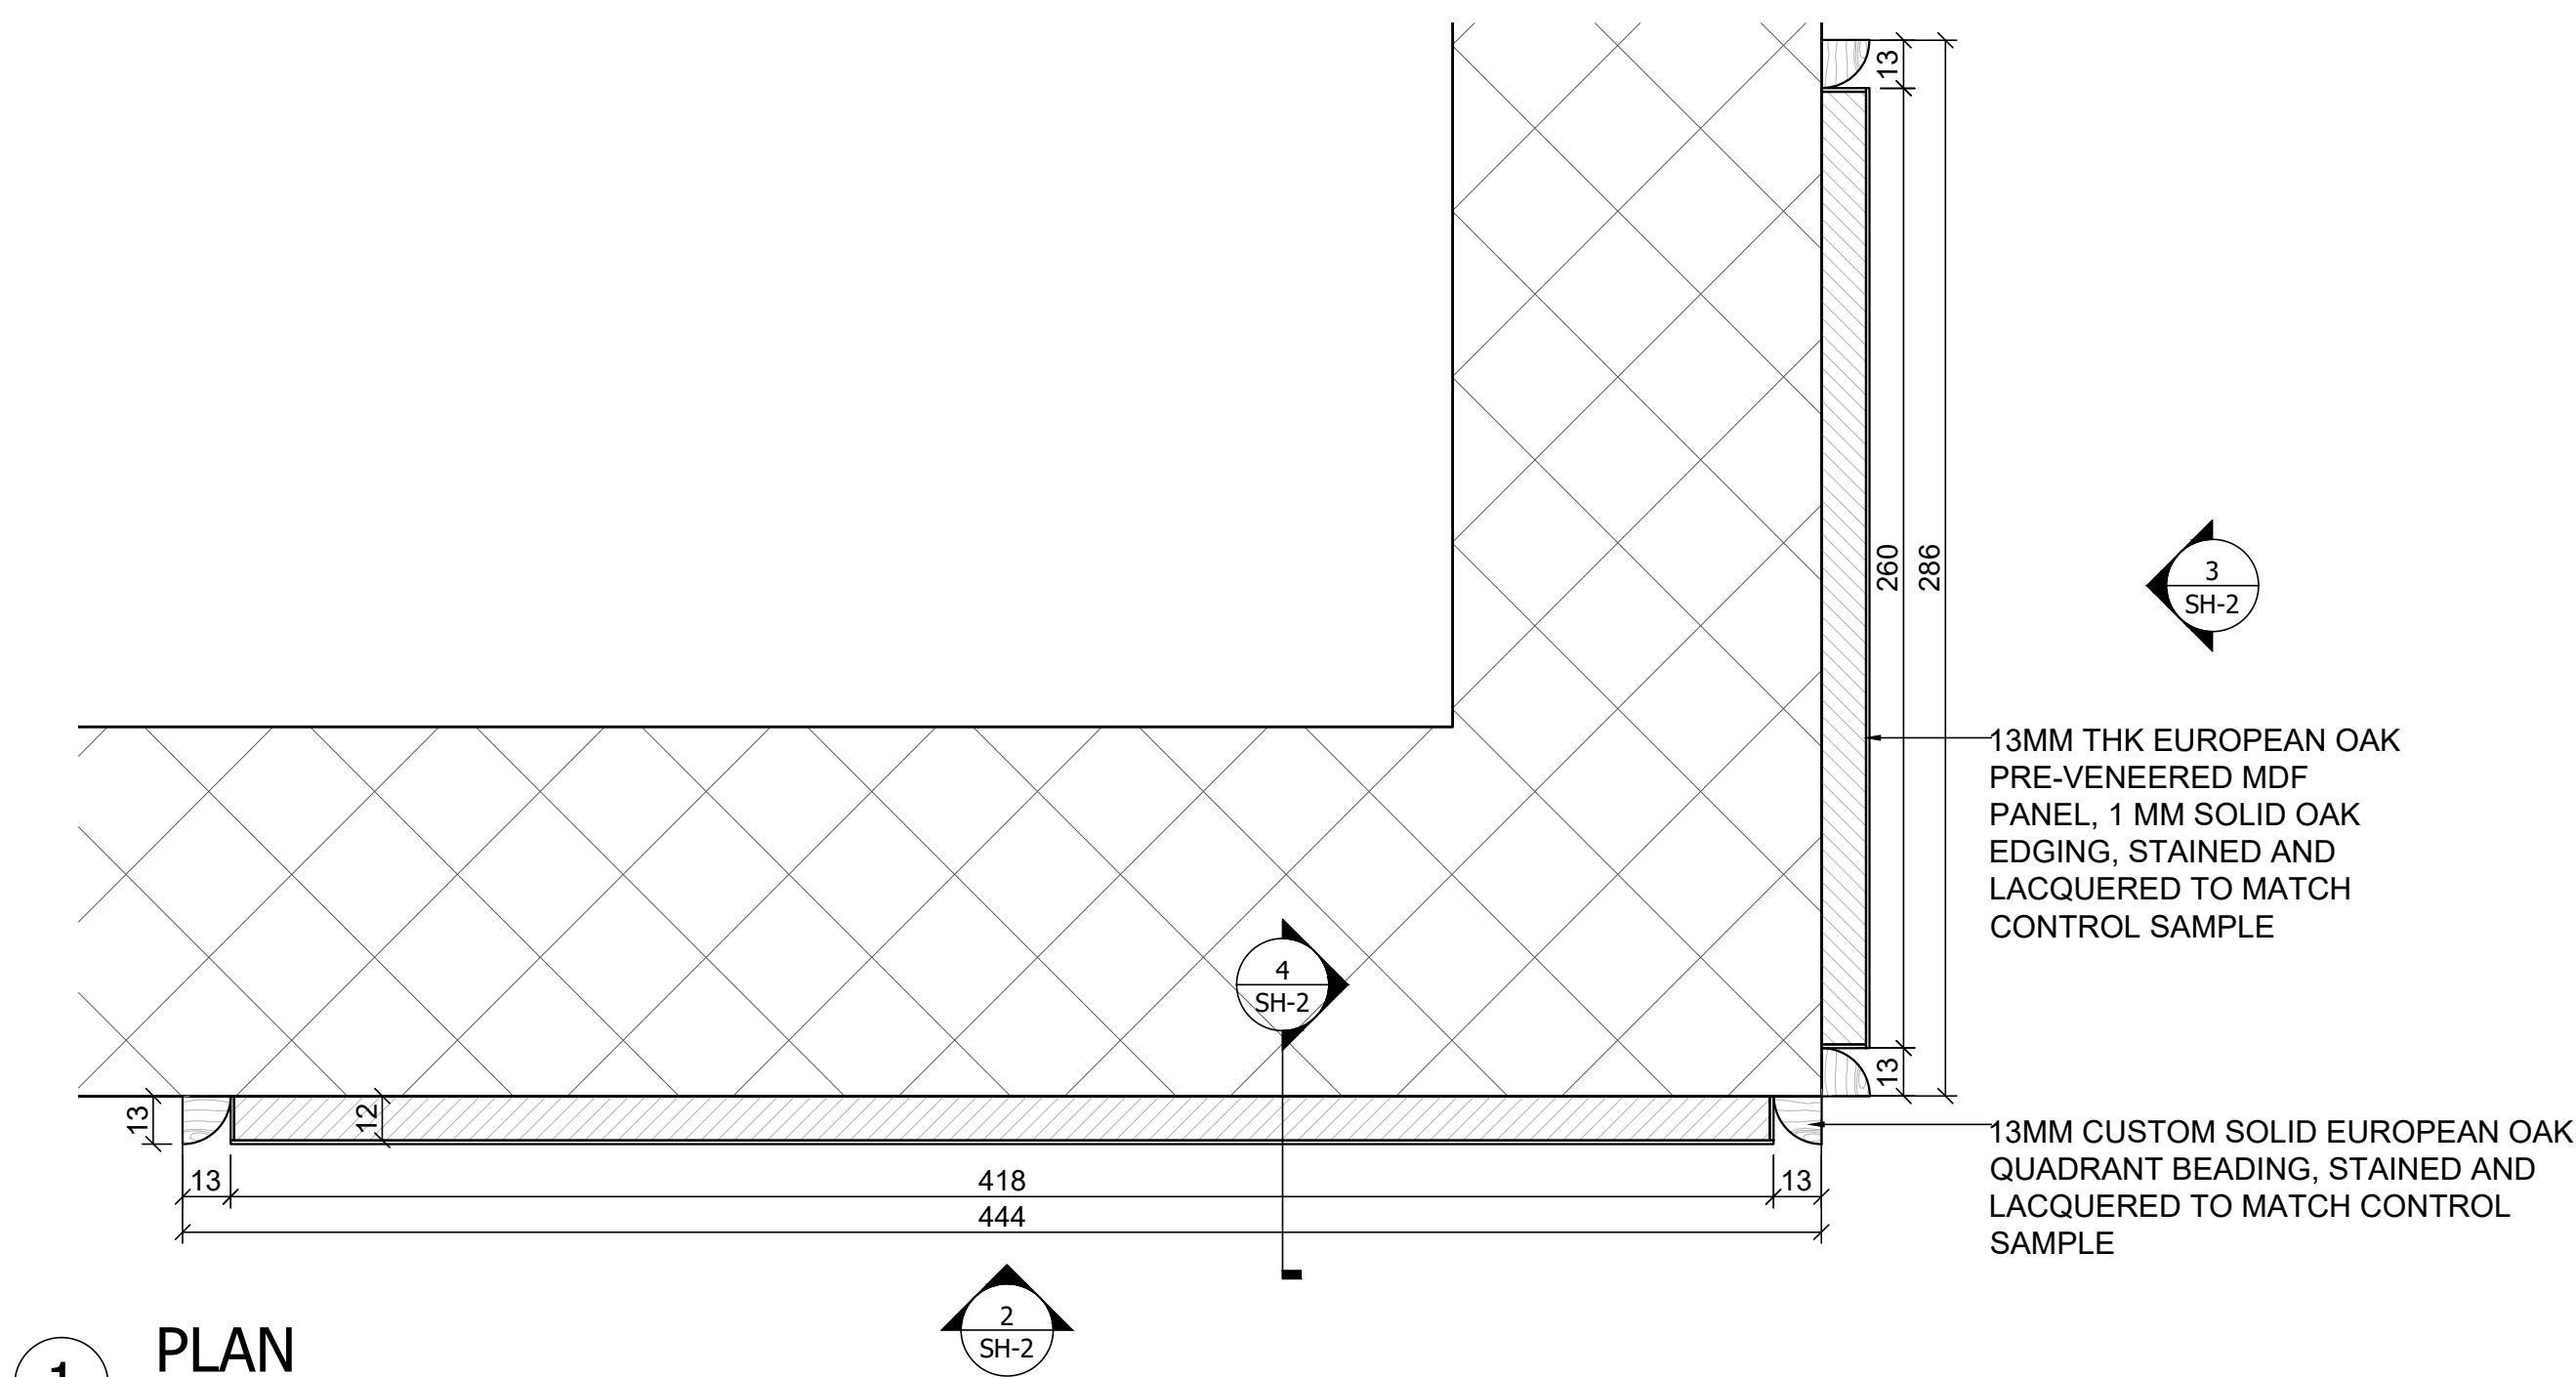


FOR APPROVAL	
	
PROJECT:	STW2732
TITLE:	JXX - L SHAPED WALL PANEL
DETAILS:	PLAN, ELEVATION AND SECTION
DATE:	03/23/2026
SHEET:	2 OF 3
DRAWN:	JPO
CHECK:	ACA
SCALE:	AS SHOWN @ A1
DRAWING N°:	REVISION:
STW2732– JXX– 02	
00	




PROJECT:	STW2732	
TITLE:	JXX - L SHAPED WALL PANEL	
DETAILS:	PLAN, ELEVATION AND SECTION	
DATE:	03/23/2026	
SHEET:	2 OF 3	
DRAWN:	JPO	
CHECK:	ACA	
SCALE:	AS SHOWN @ A1	
DRAWING N°:	REVISION:	
STW2732– JXX– 02		00


REVISION HISTORY		
REV	DESCRIPTION	DATE
	FIRST ISSUE	03/23/2026

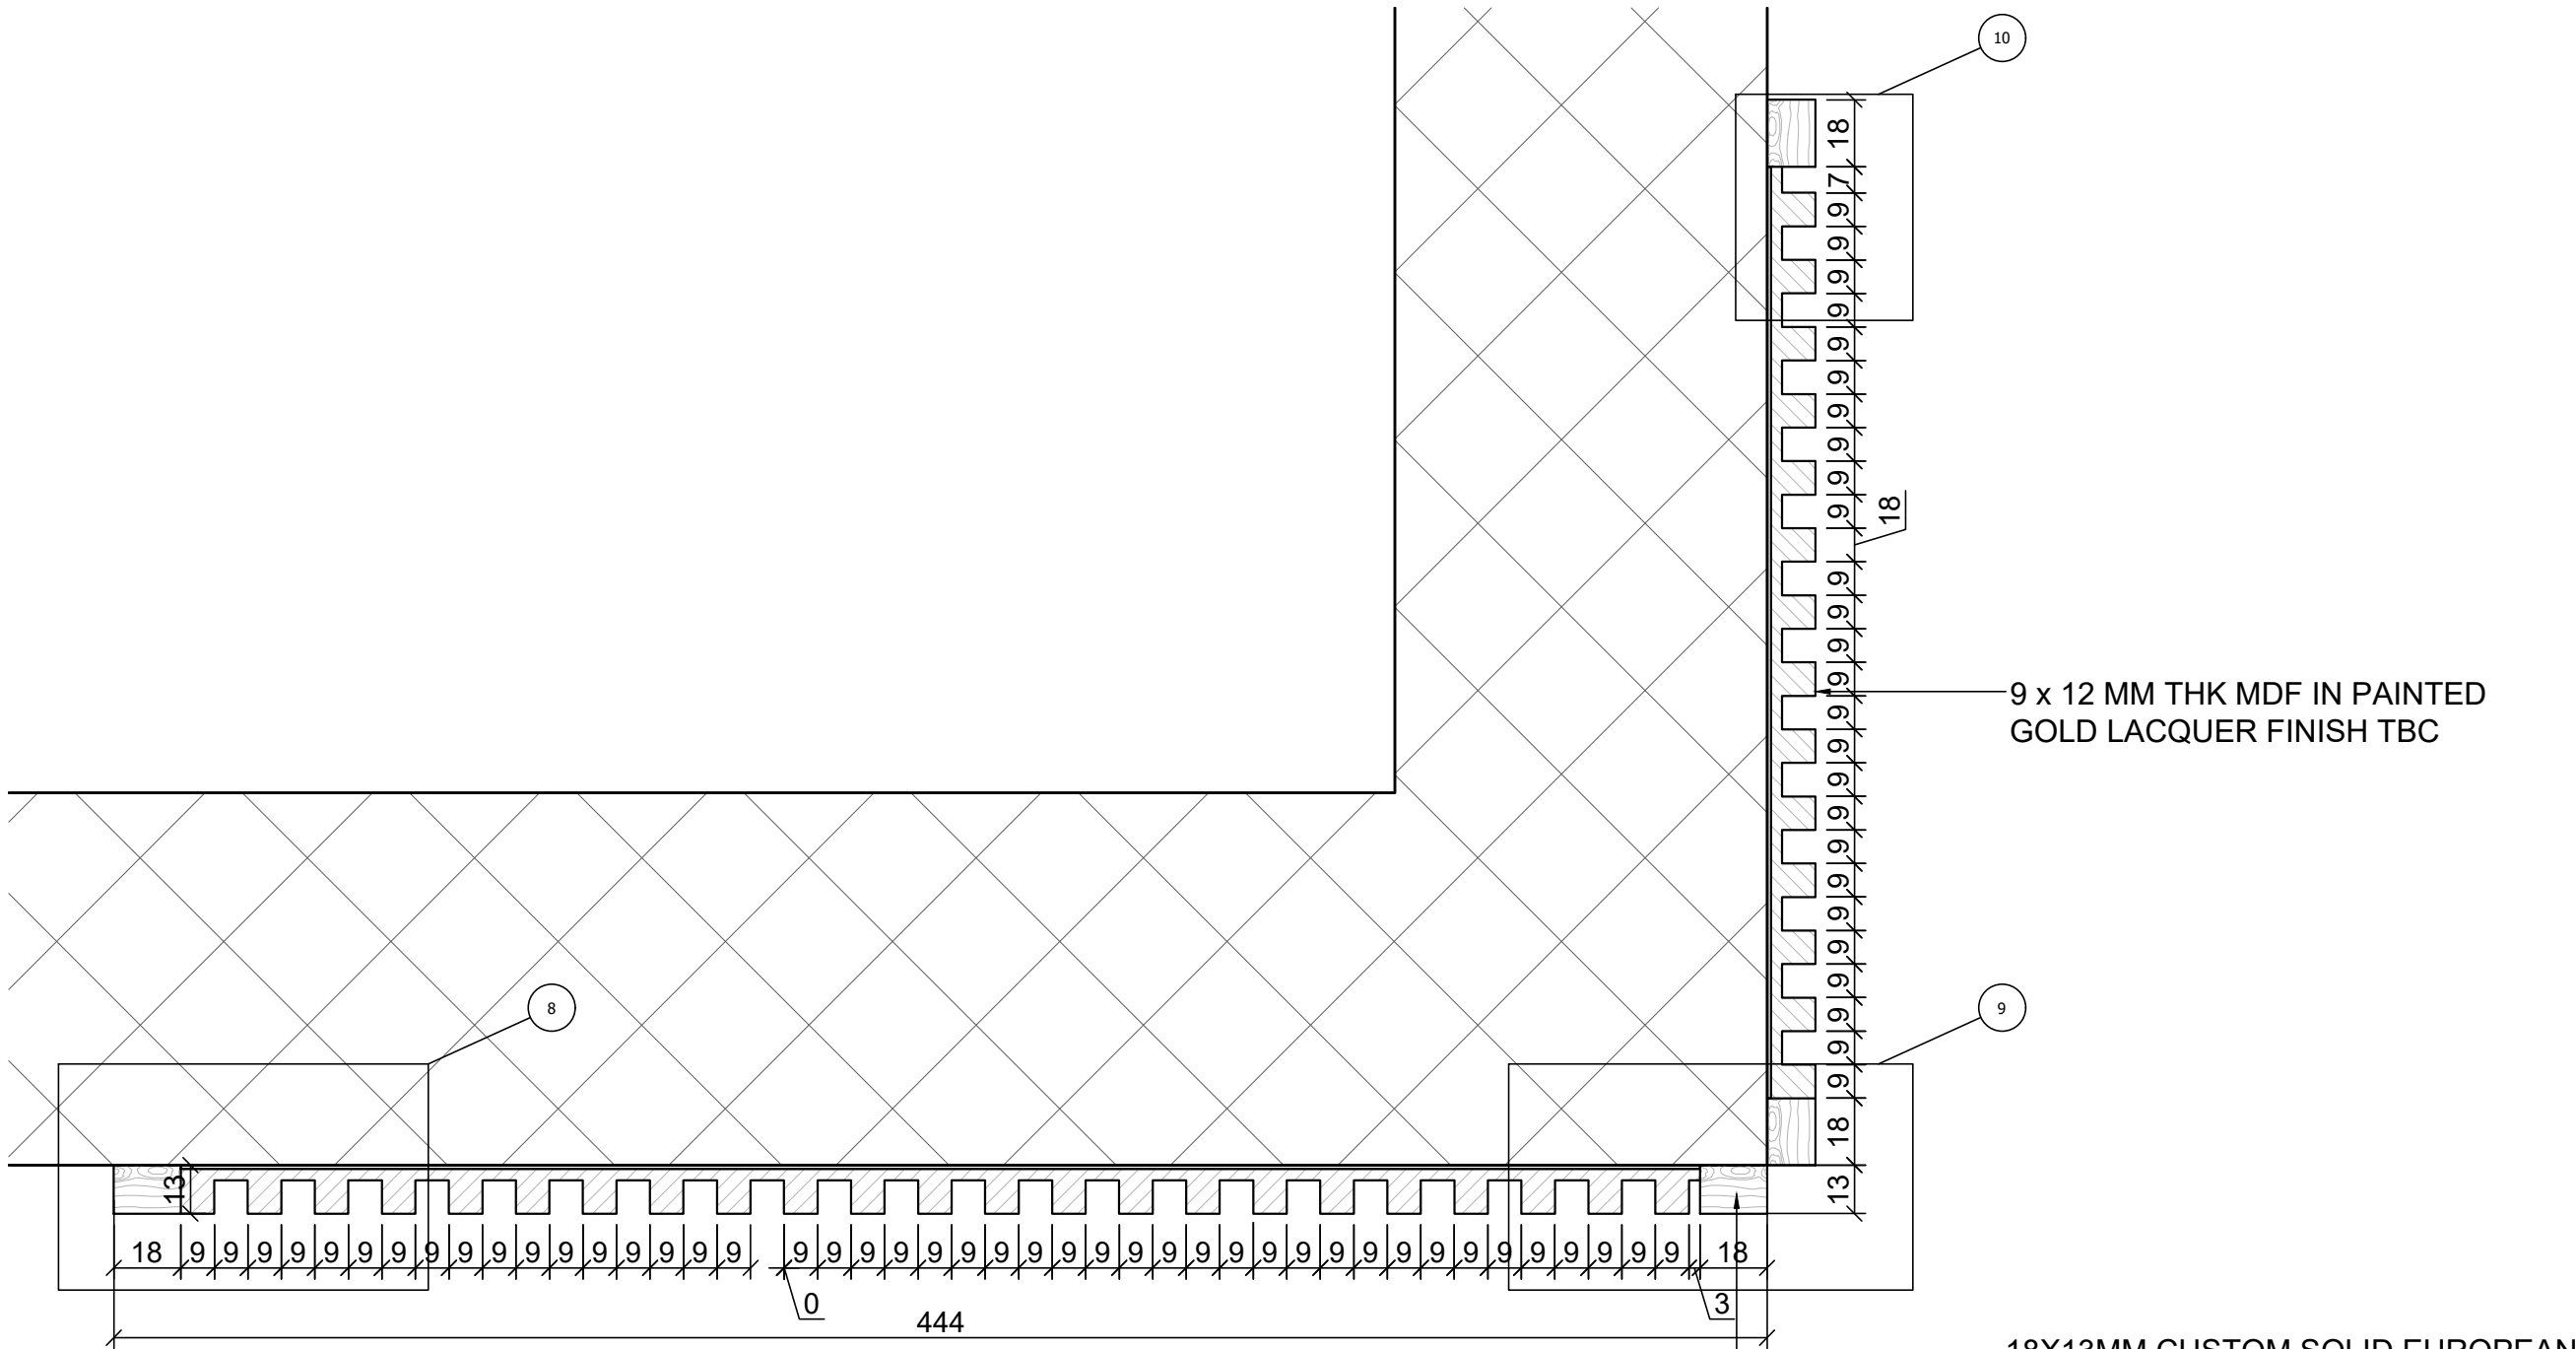


6 PLAN DETAILS
Scale: 1:2

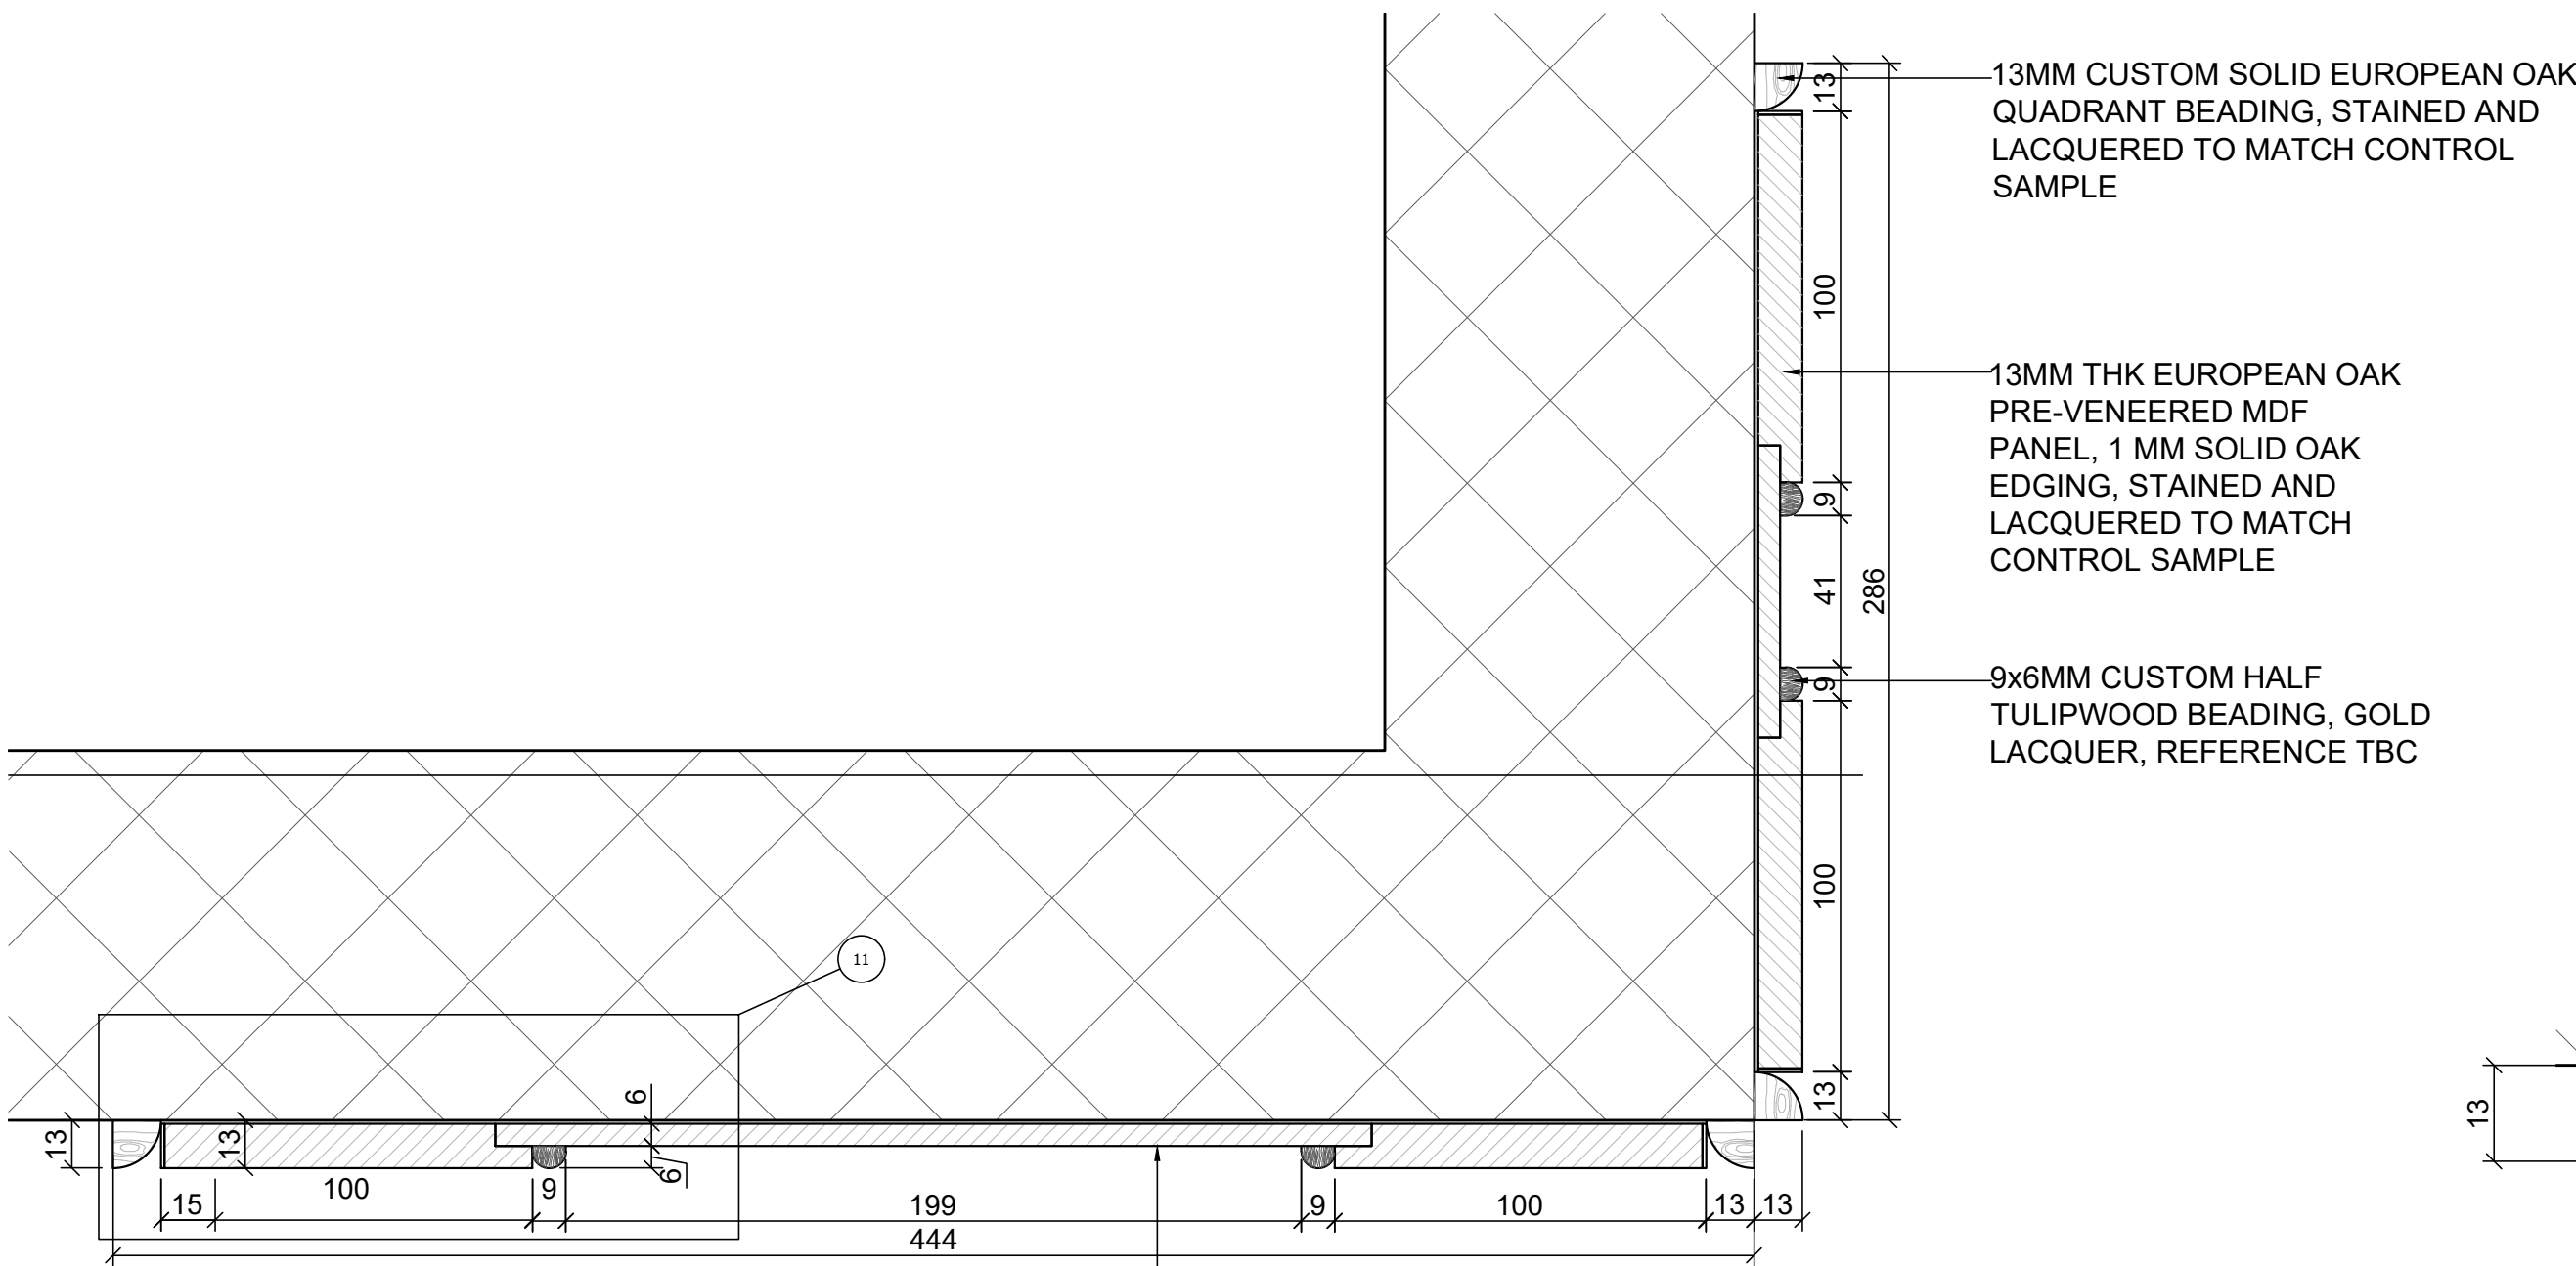


7 PLAN DETAILS
Scale: 1:2

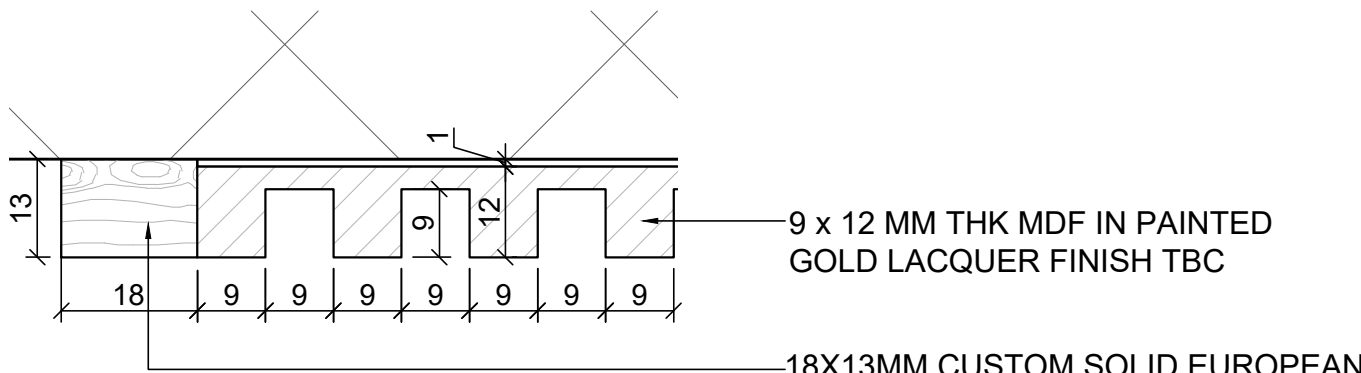


8 DETAILS
Scale: 1:1

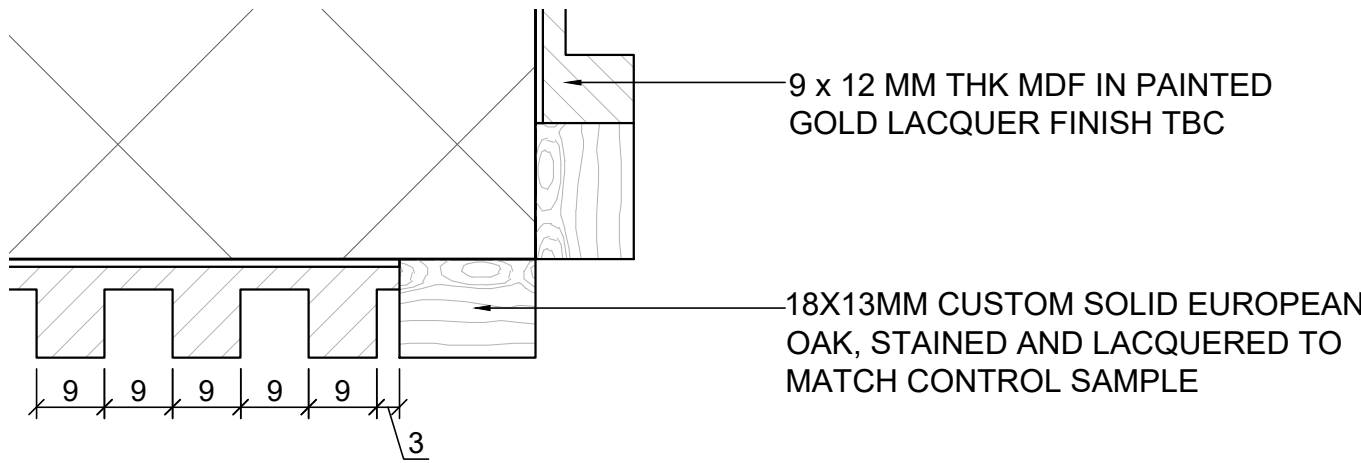


9 DETAILS
Scale: 1:1

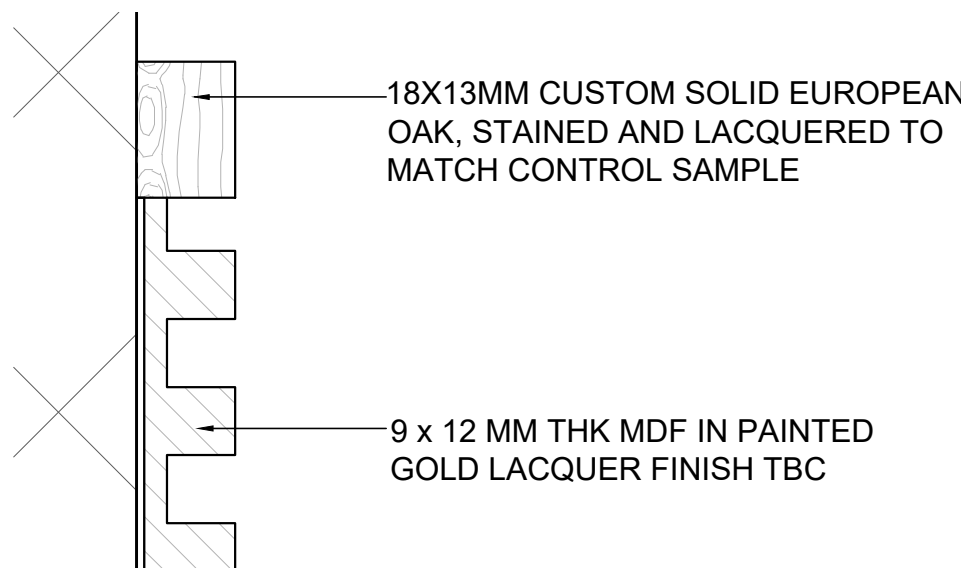


10 DETAILS
Scale: 1:1

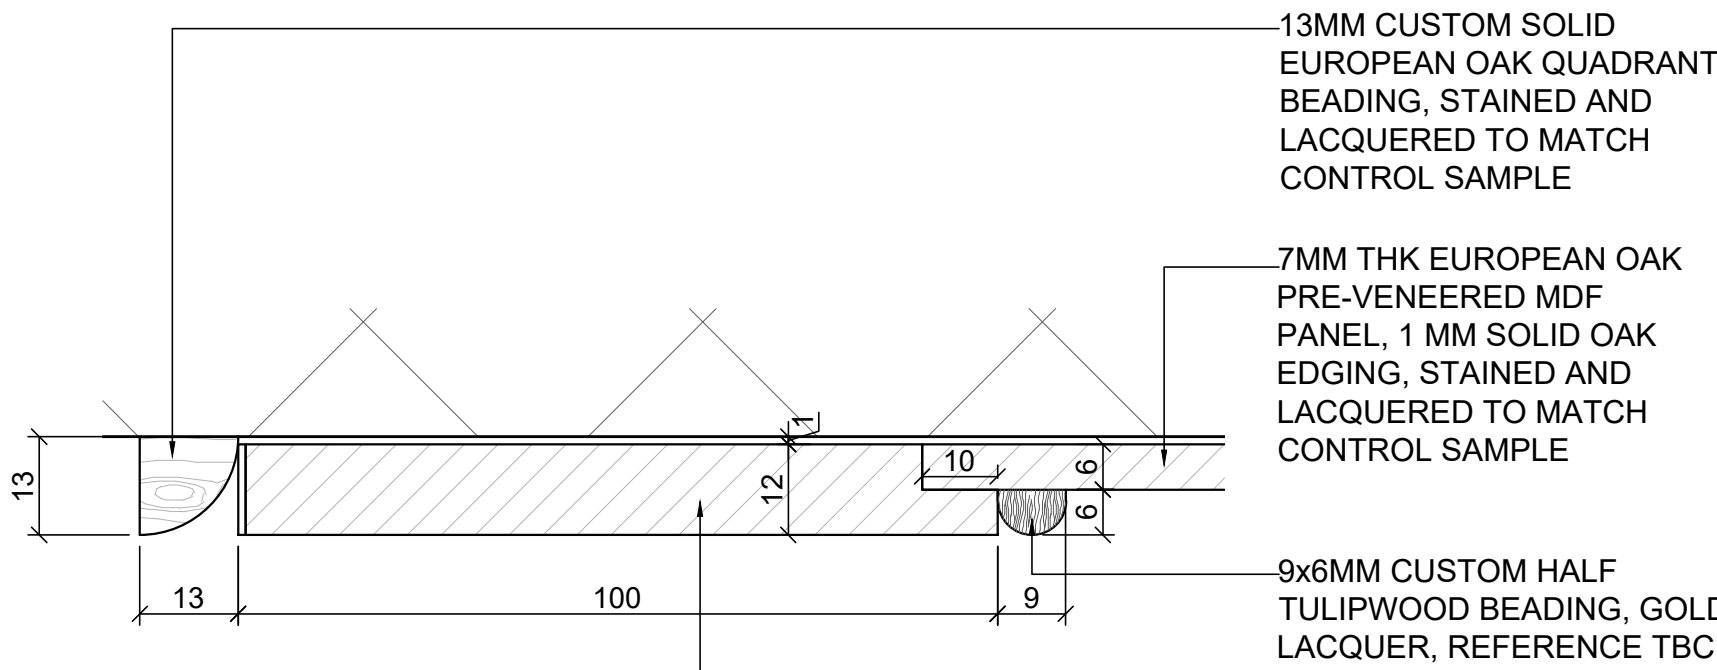

11 DETAILS
Scale: 1:1

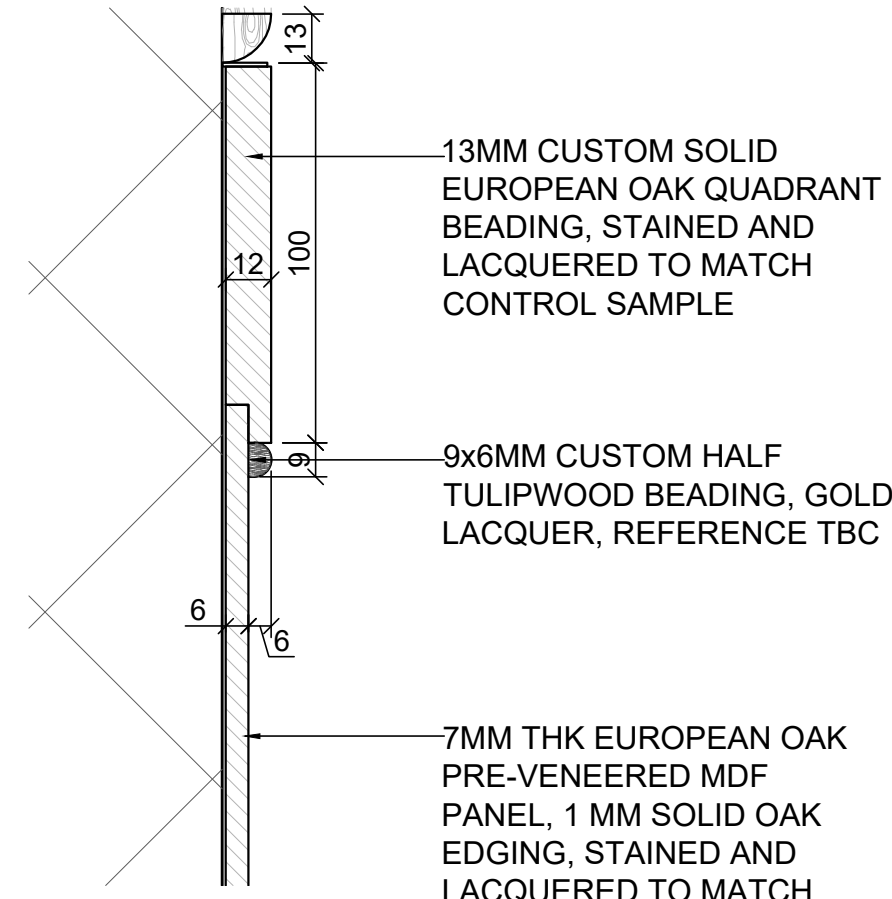

12 DETAILS
Scale: 1:2

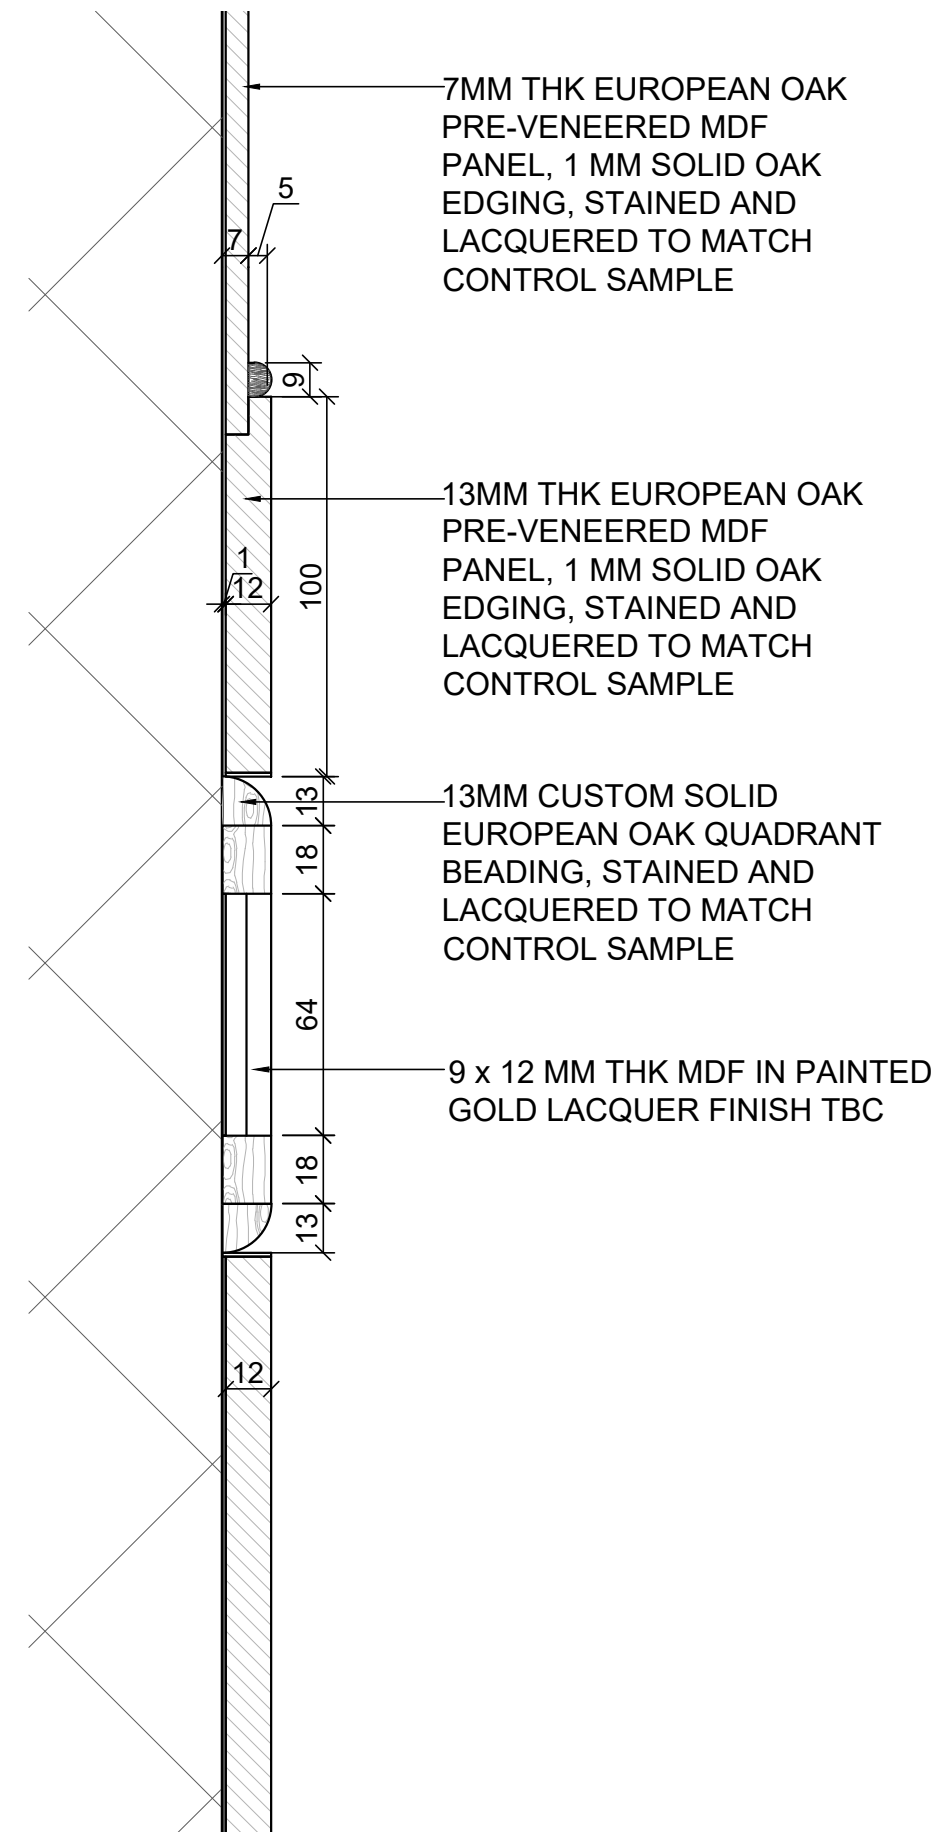

13 DETAILS
Scale: 1:2

FOR APPROVAL



PROJECT:	STW2732
TITLE:	JXX - L SHAPED WALL PANEL
DETAILS:	DETAILS
DATE:	03/23/2026
SHEET:	3 OF 3
DRAWN:	JPO
CHECK:	ACA
SCALE:	AS SHOWN @ A1
DRAWING N°:	REVISION:
STW2732– JXX– 03	00