

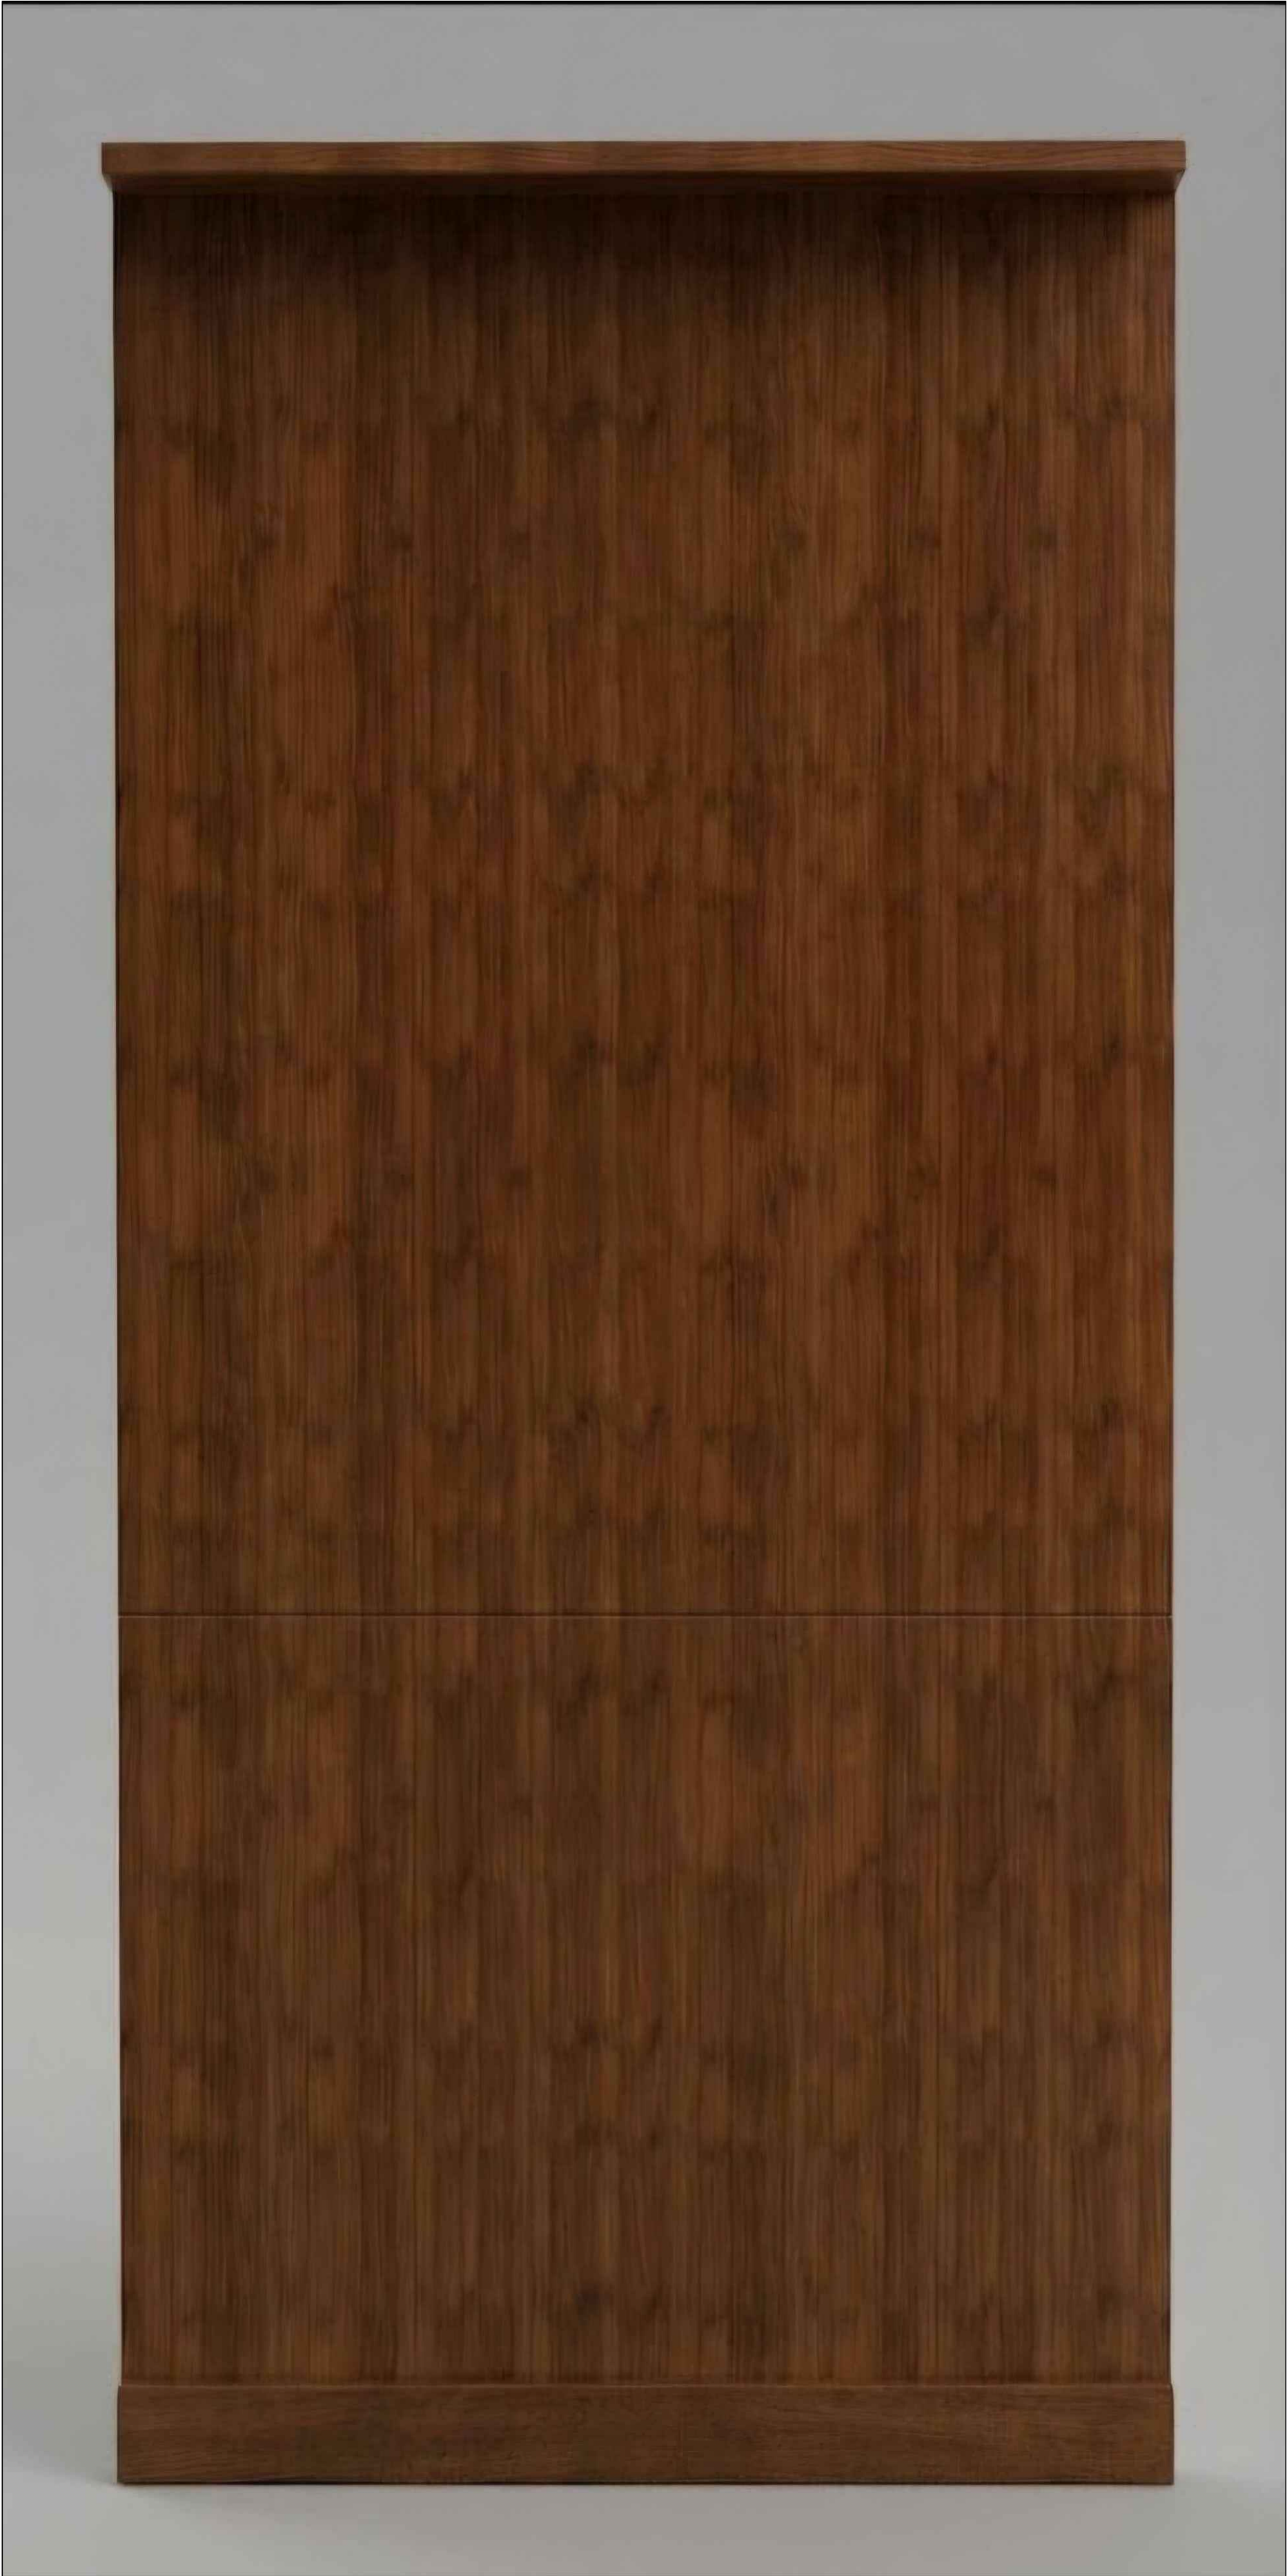


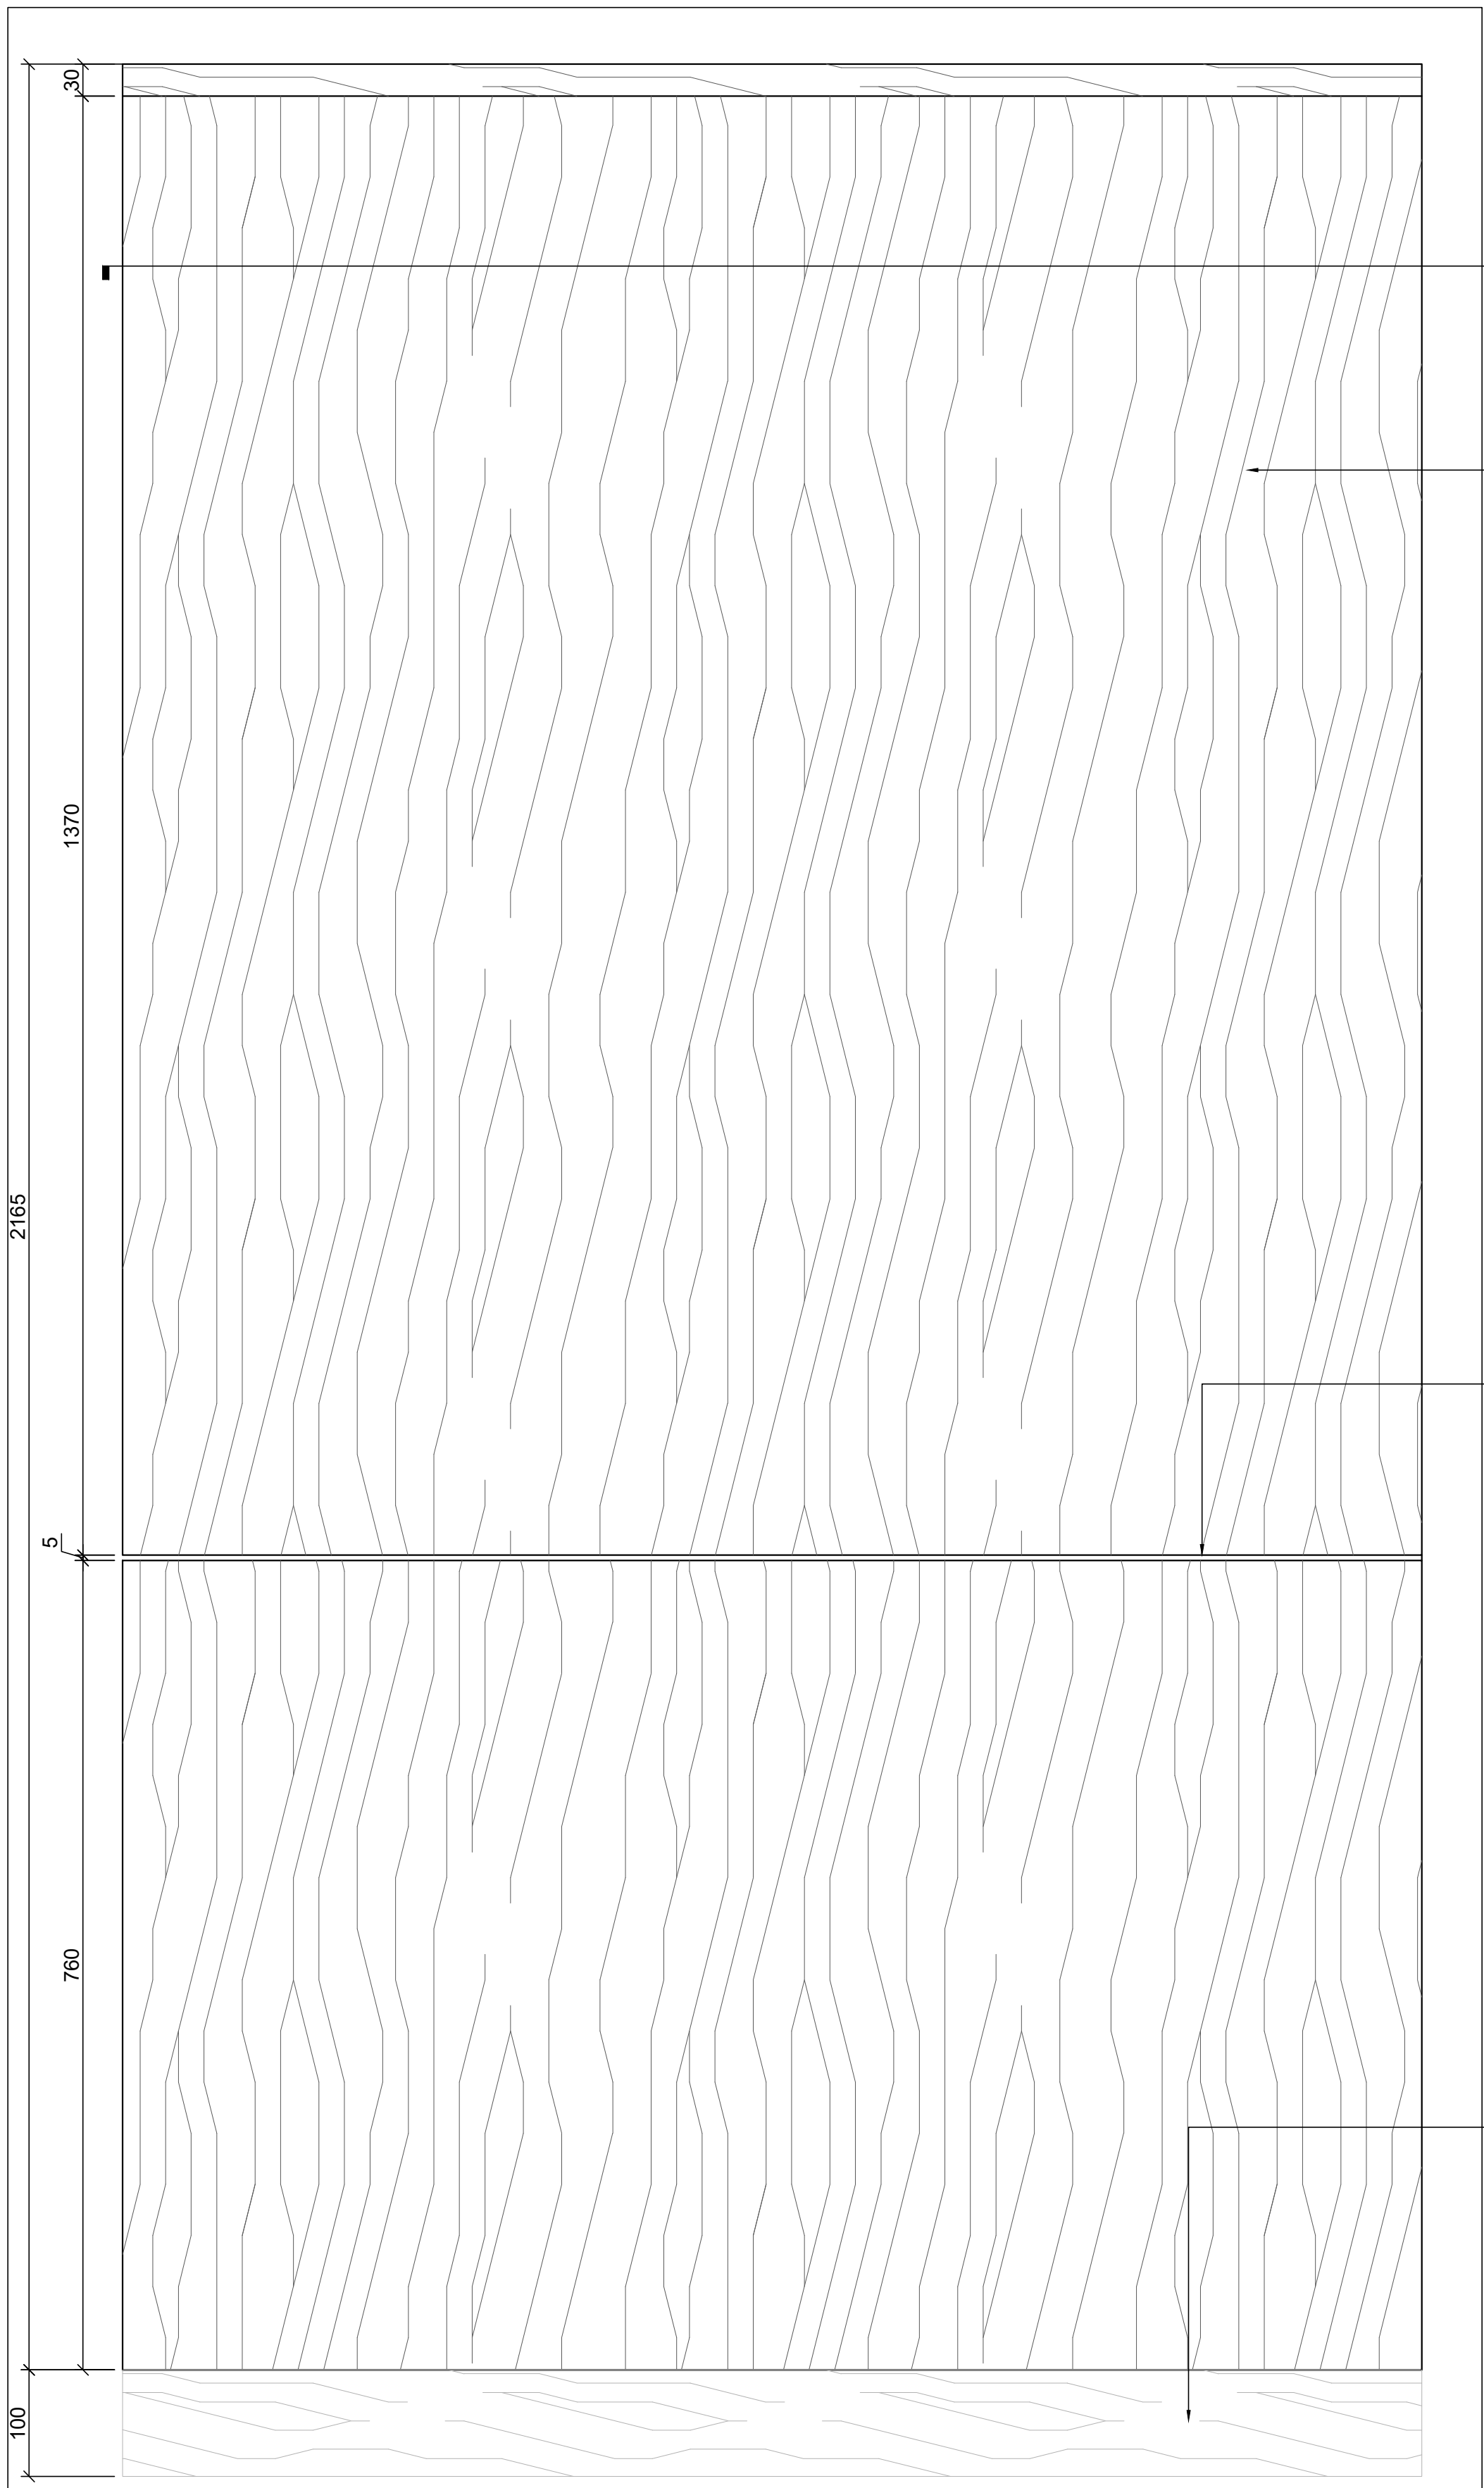

FOR APPROVAL	
	
PROJECT:	STW2732
TITLE:	JXX - STRAIGHT WALL PANEL
DETAILS:	RENDERING
DATE:	03/23/2026
SHEET:	1 OF 2
DRAWN:	JPO
CHECK:	ACA
SCALE:	AS SHOWN @ A1
DRAWING N°:	REVISION:
STW2732– JXX– 01	00

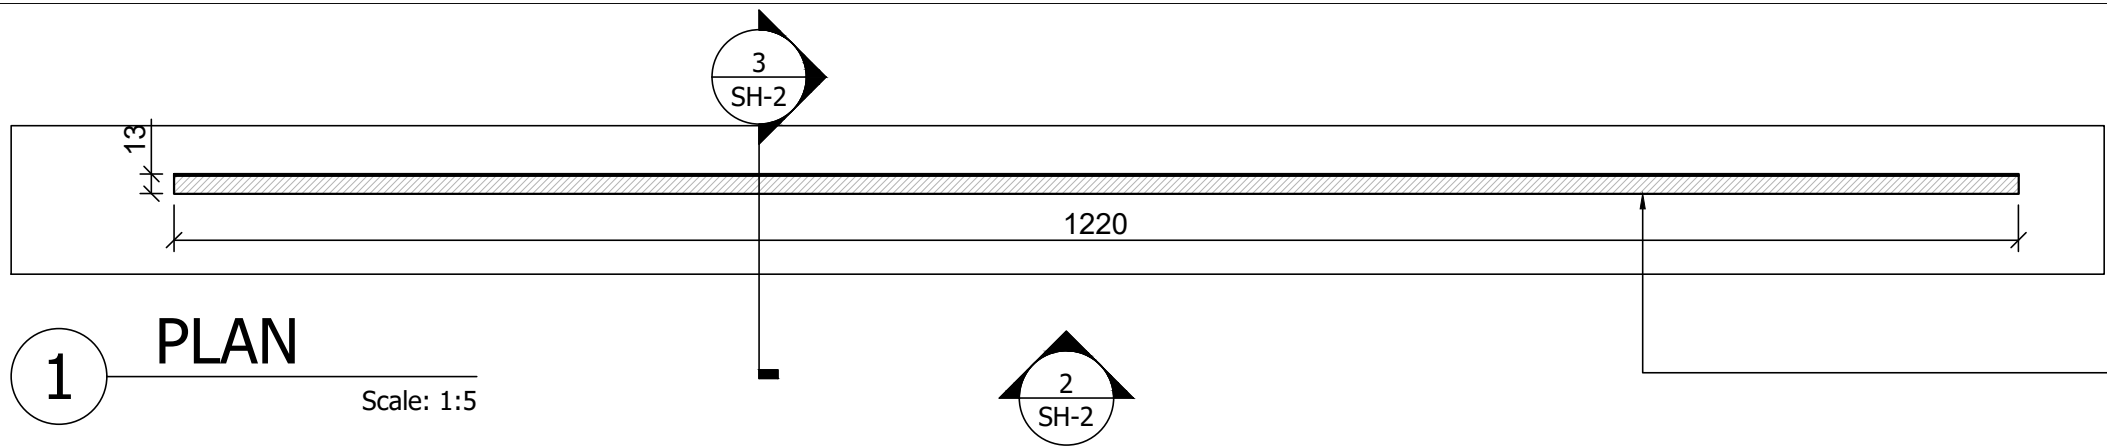


2 ELEVATION
Scale: 1:5

13MM THK EUROPEAN OAK
PRE-VENEERED MDF
PANEL, 1 MM SOLID OAK
EDGING, STAINED AND
LACQUERED TO MATCH
CONTROL SAMPLE

13MM THK EUROPEAN OAK
PRE-VENEERED MDF
PANEL, 1 MM SOLID OAK
EDGING, STAINED AND
LACQUERED TO MATCH
CONTROL SAMPLE

5X5MM GROOVE

FOR SKIRTING SEE DRG
CORNICE AND SKIRTING
DETAIL

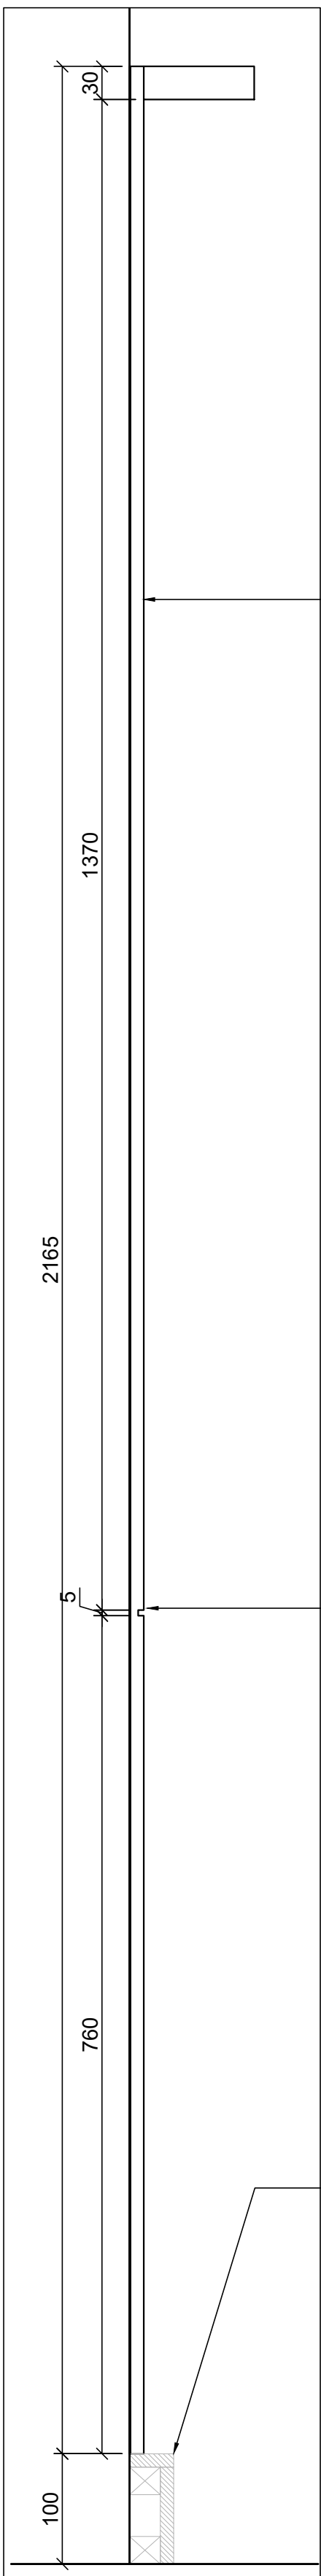


3 SECTION
Scale: 1:5

13MM THK EUROPEAN OAK
PRE-VENEERED MDF
PANEL, 1 MM SOLID OAK
EDGING, STAINED AND
LACQUERED TO MATCH
CONTROL SAMPLE

5X5MM GROOVE

FOR SKIRTING SEE DRG
CORNICE AND SKIRTING
DETAIL

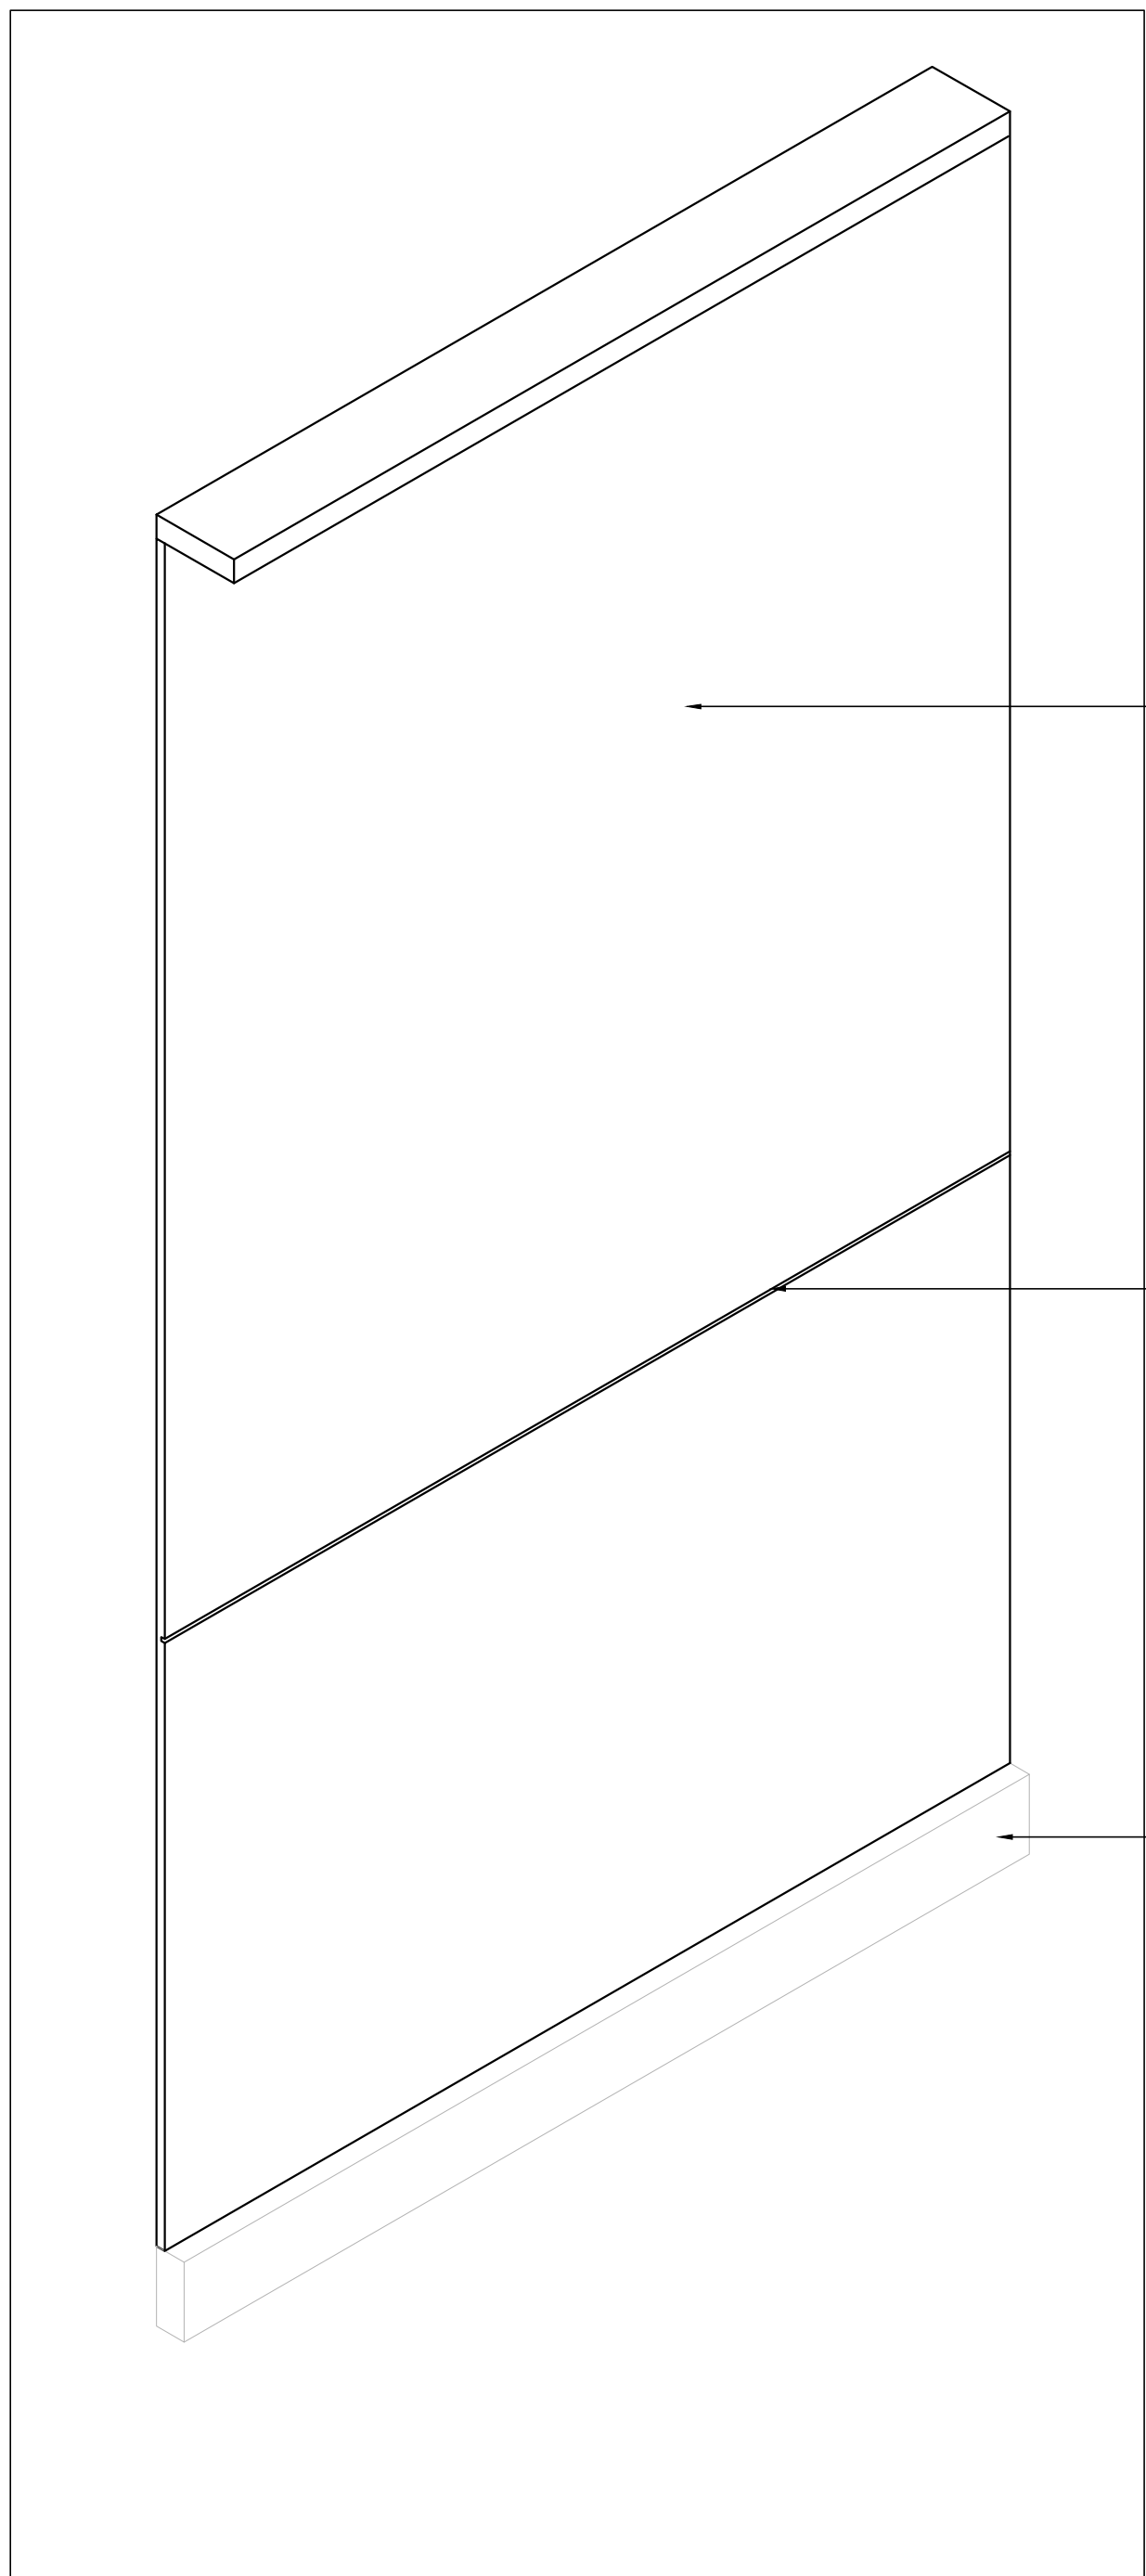

4 ISOMETRIC
Scale: NTS

REVISION HISTORY

REV	DESCRIPTION	DATE
	FIRST ISSUE	03/23/2026

13MM THK EUROPEAN OAK
PRE-VENEERED MDF
PANEL, 1 MM SOLID OAK
EDGING, STAINED AND
LACQUERED TO MATCH
CONTROL SAMPLE

5X5MM GROOVE

FOR SKIRTING SEE DRG
CORNICE AND SKIRTING
DETAIL

FOR APPROVAL



PROJECT:	STW2732
TITLE:	JXX - STRAIGHT WALL PANEL
DETAILS:	PLAN, ELEV. AND DETAILS
DATE:	03/23/2026
SHEET:	2 OF 2
DRAWN:	JPO
CHECK:	ACA
SCALE:	AS SHOWN @ A1
DRAWING N°:	STW2732- JXX- 02
REVISION:	00